




Müşteri	: BEŞİKTAŞ TERSANE A.Ş.	Proje Notları :	
Proje adı	: DÜZGİT TERSANE İDARİ BİNA		
İş adı	: DP-2 (1.KAT DAĞITIM PANOSU-1)		
Üretici firma	: GÜL PANO ELEKTRİK SAN.TİC.LTD.ŞTİ.		
İş no	: -		
Pano voltajı	: 220/380V 50Hz		
Pano Tipi / Ebat	: DAHİLİ DUVAR TİP PANO / 1300x650x200mm.		
Pano rengi	: RAL-		
Tarih (Başlangıç)	: 30.12.2022		
Rev 1	:		Rev 5
Rev 2	:	Rev 6	:
Rev 3	:	Rev 7	:
Rev 4	:	Rev 8	:

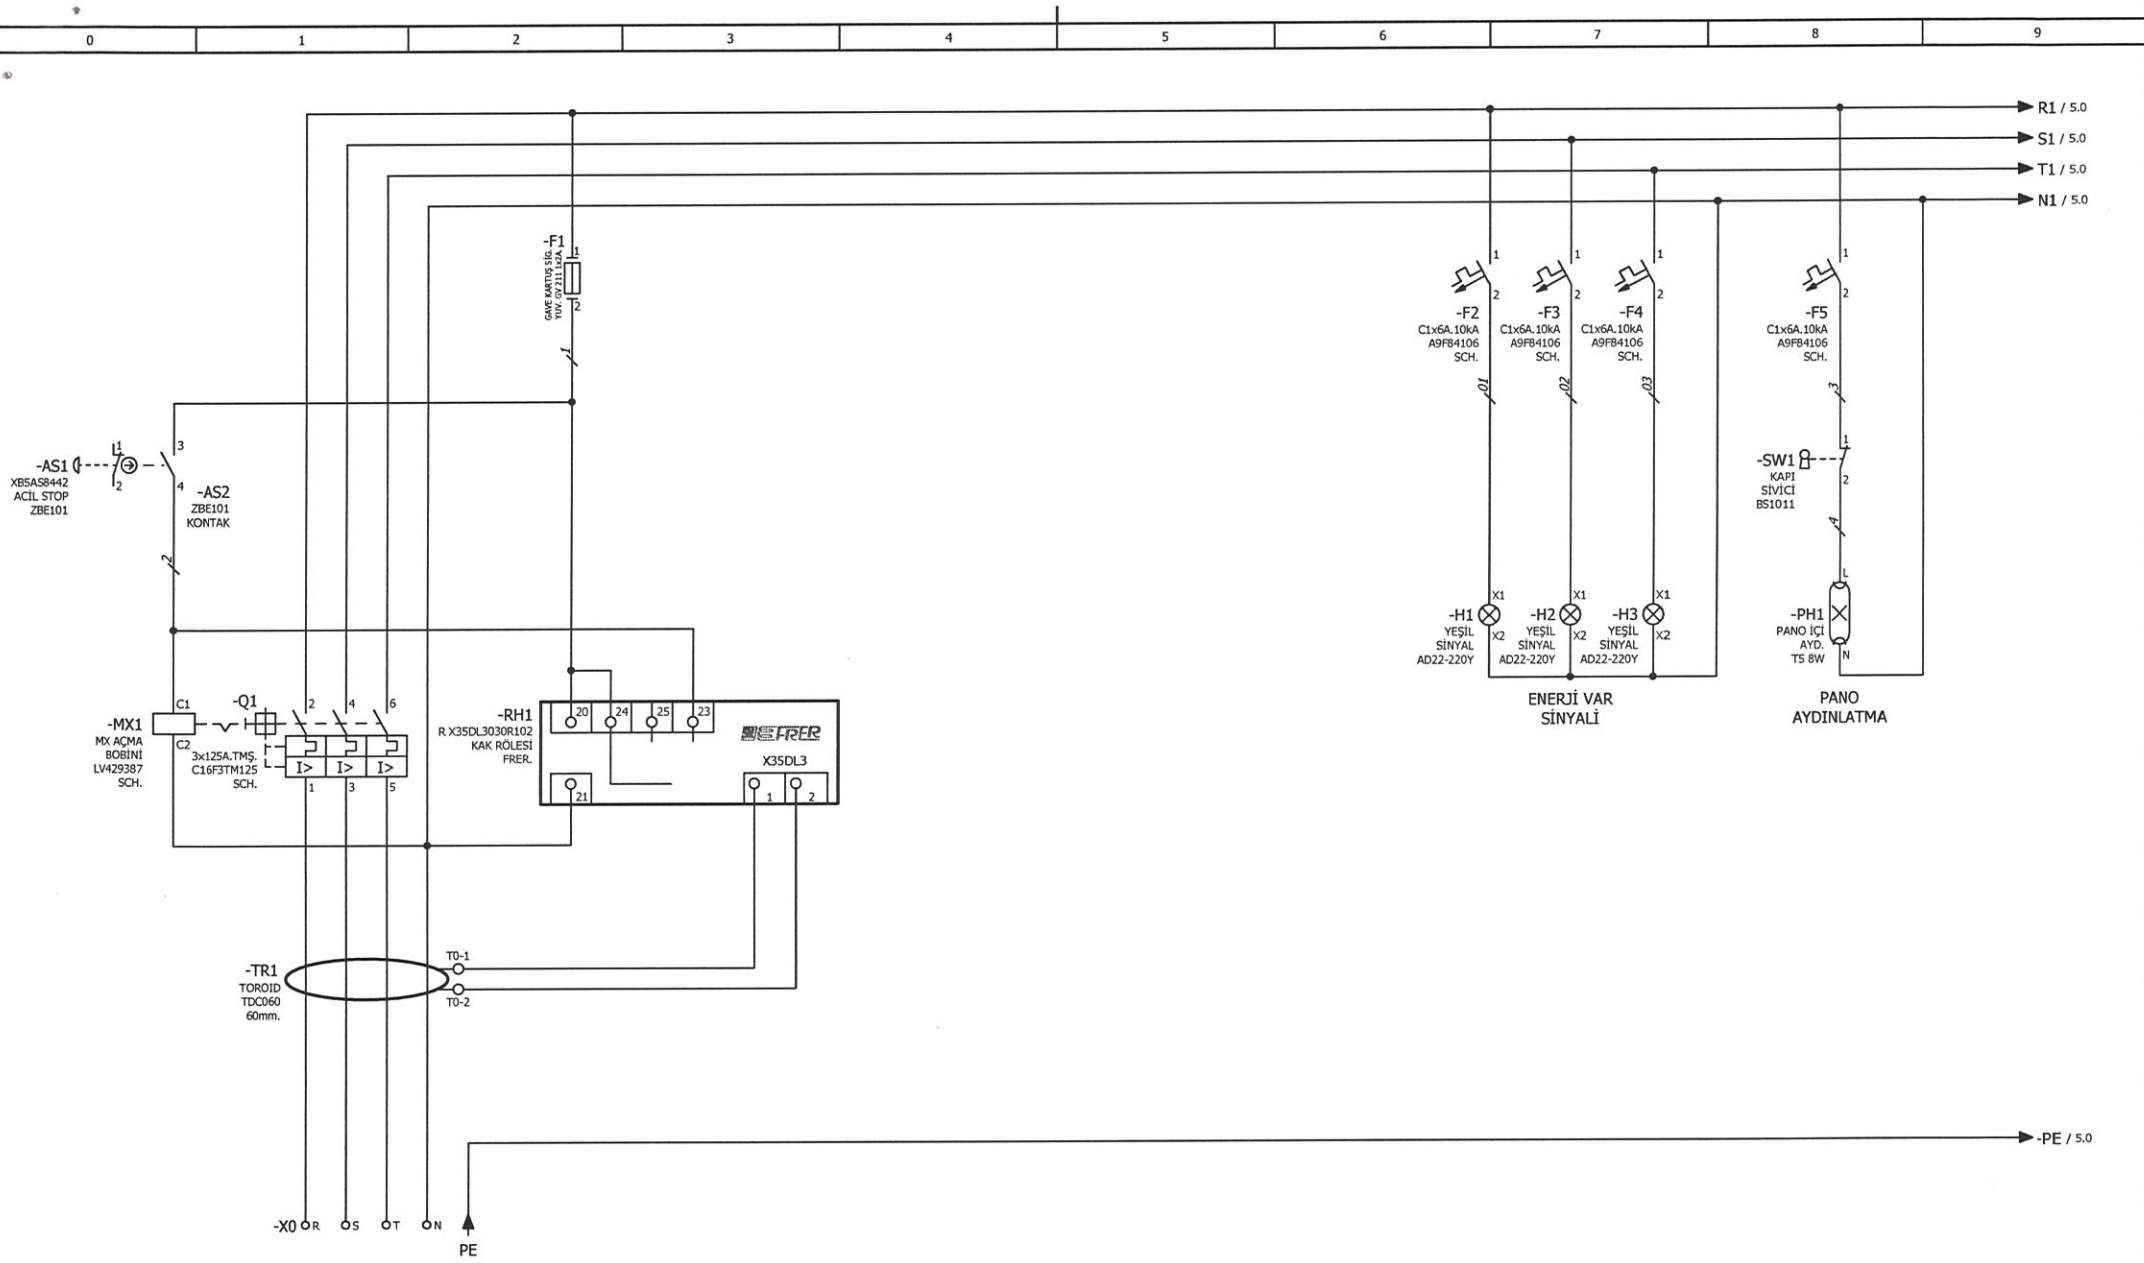


LİNYE NO:	ŞEBEKE
AÇIKLAMA	ENERJİ GİRİŞİ 220/380V AC 50Hz
KABLO	4x25mm ² +1x16 mm ² N2XH
GÜÇ (W)	71.456

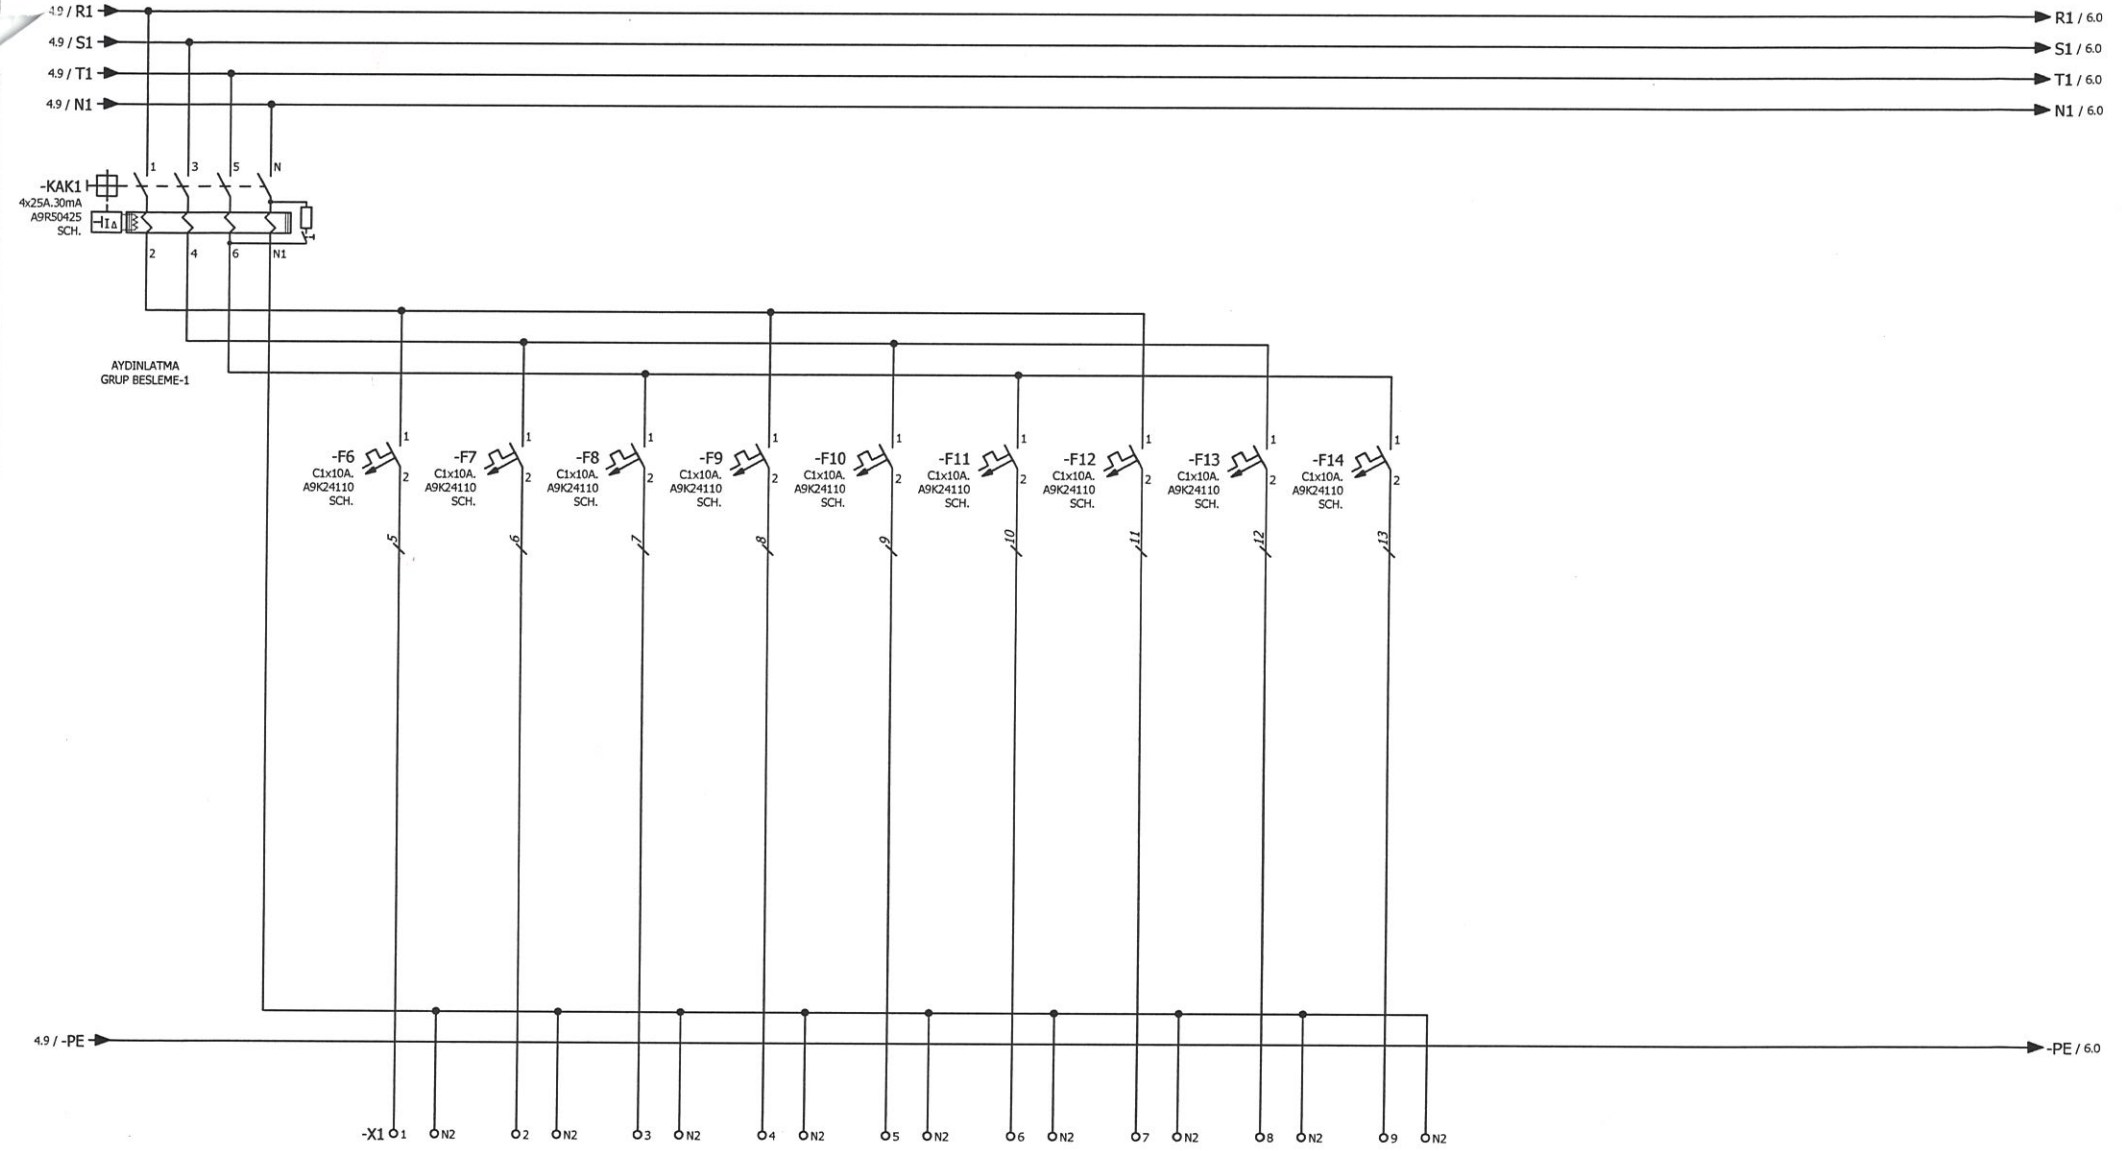


LİNYE NO:	A-01	A-02	A-03	A-04	A-05	A-06	A-07	A-08	A-09
AÇIKLAMA	TOPLANTI ODASI	KORİDOR	KORİDOR	KORİDOR	DİZAYN	DİZAYN	WC-SERVİS	YÖNETİM&İCRA KURULU	TERSANE MÜDÜRÜ
KABLO	3x2.5mm ² NHXMH	3x2.5mm ² NHXMH	3x2.5mm ² NHXMH	3x2.5mm ² NHXMH	3x2.5mm ² NHXMH	3x2.5mm ² NHXMH	3x2.5mm ² NHXMH	3x2.5mm ² NHXMH	3x2.5mm ² NHXMH
GÜÇ (W)	88	360	360	396	200	60	32	76	64

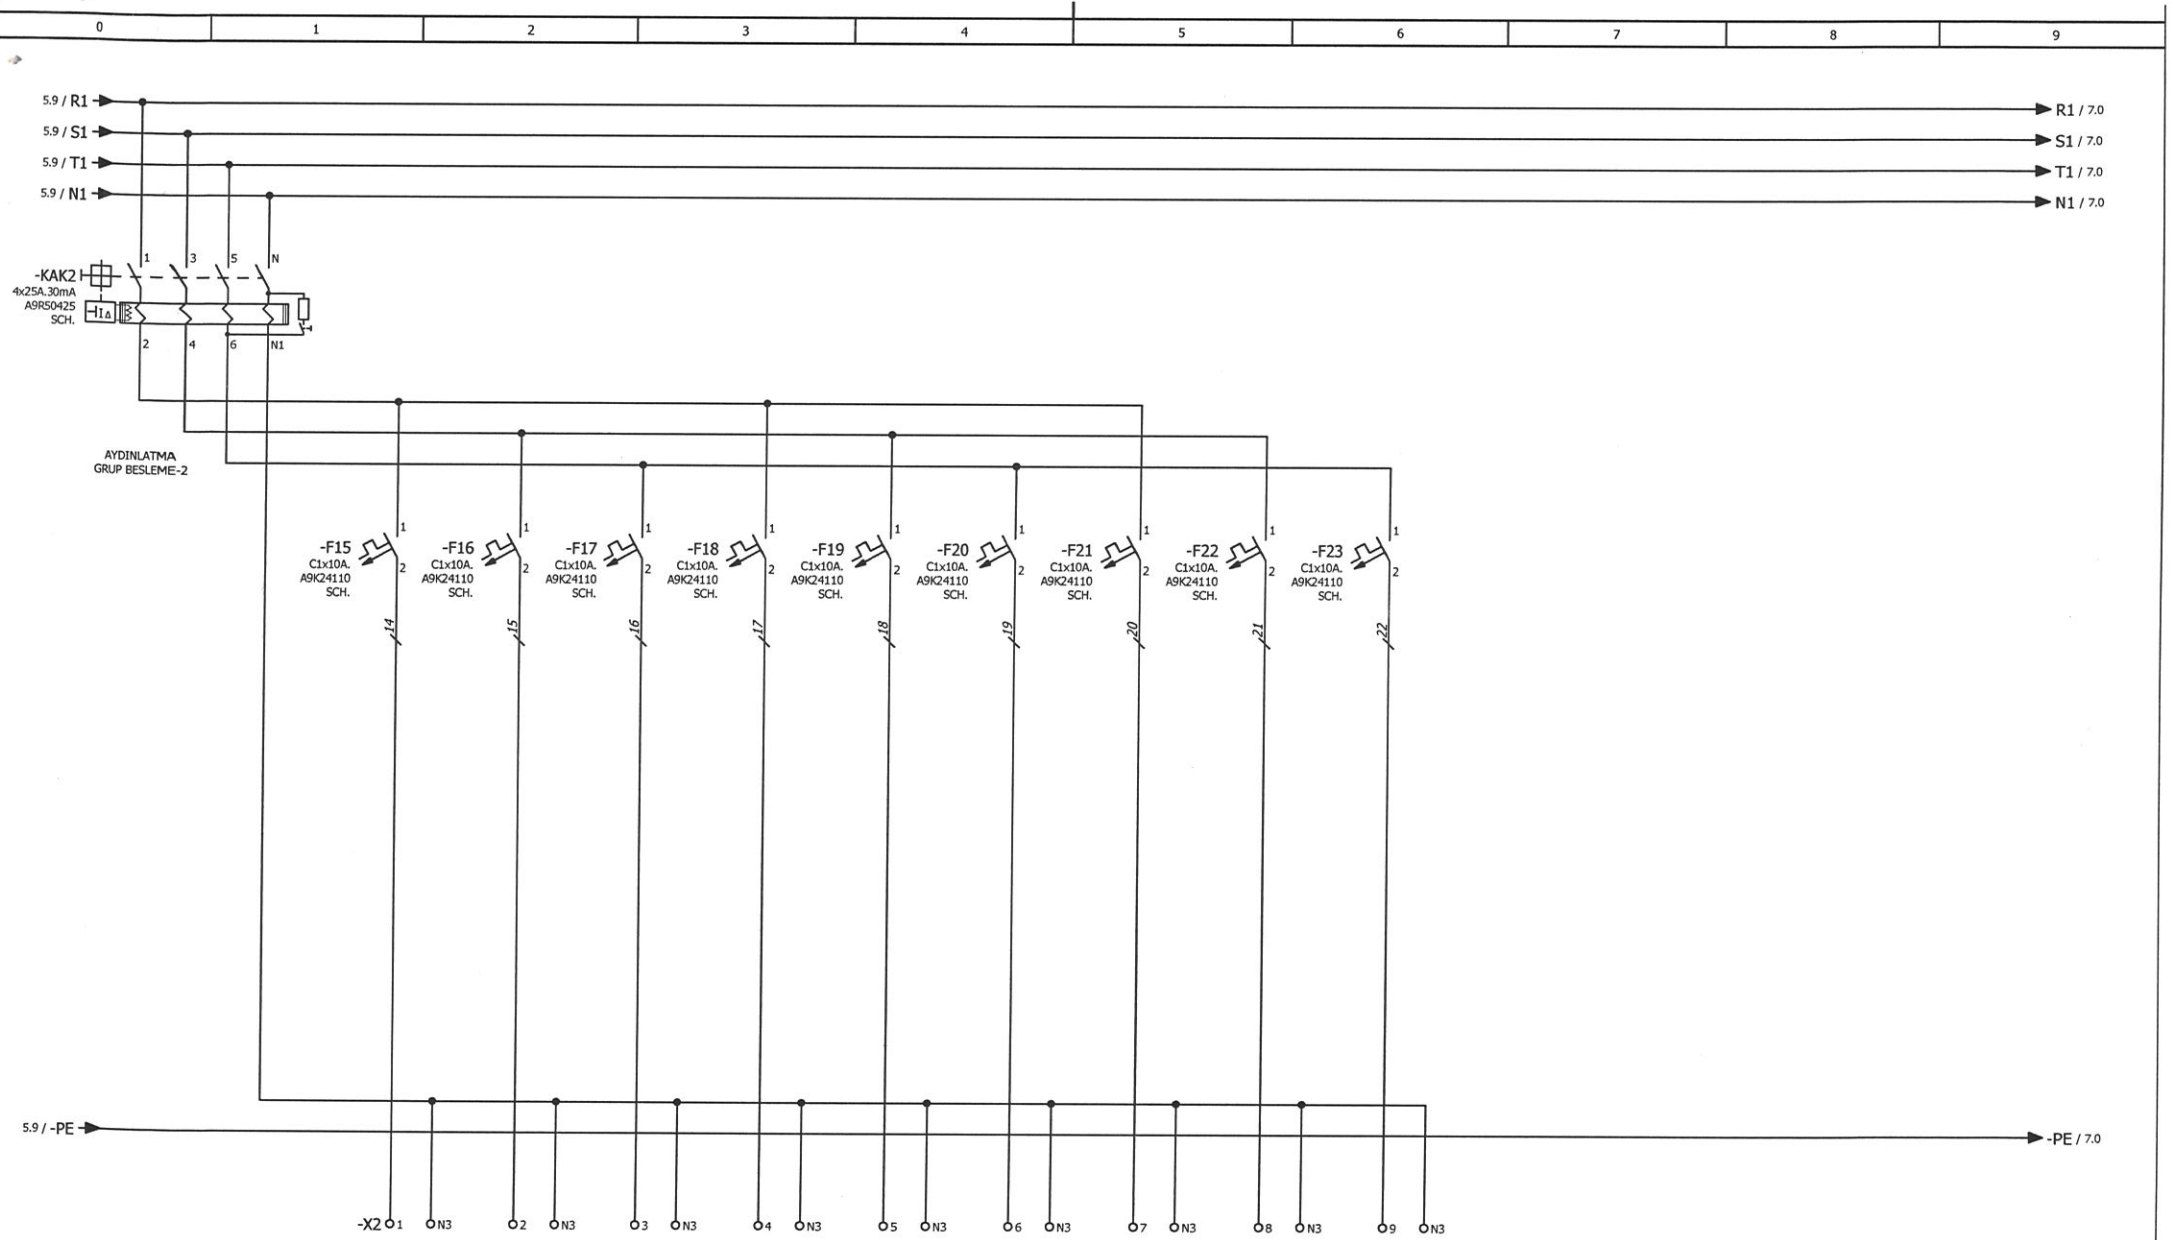


LİNYE NO:	A-10	A-11	A-12	A-13	A-14	A-15	A-16	A-17	A-18
AÇIKLAMA	ÜRETİM KALİTE KONTROL	ÜRETİM KALİTE KONTROL	ÜRETİM KALİTE KONTROL	ÜRETİM KALİTE KONTROL	KADIN WC	TOPLANTI ODASI	TOPLANTI ODASI	KİTCHENETTE	PAZARLAMA
KABLO	3x2.5mm²NHXMH	3x2.5mm²NHXMH	3x2.5mm²NHXMH	3x2.5mm²NHXMH	3x2.5mm²NHXMH	3x2.5mm²NHXMH	3x2.5mm²NHXMH	3x2.5mm²NHXMH	3x2.5mm²NHXMH
GÜÇ (W)	200	54	72	200	72	56	56	84	104

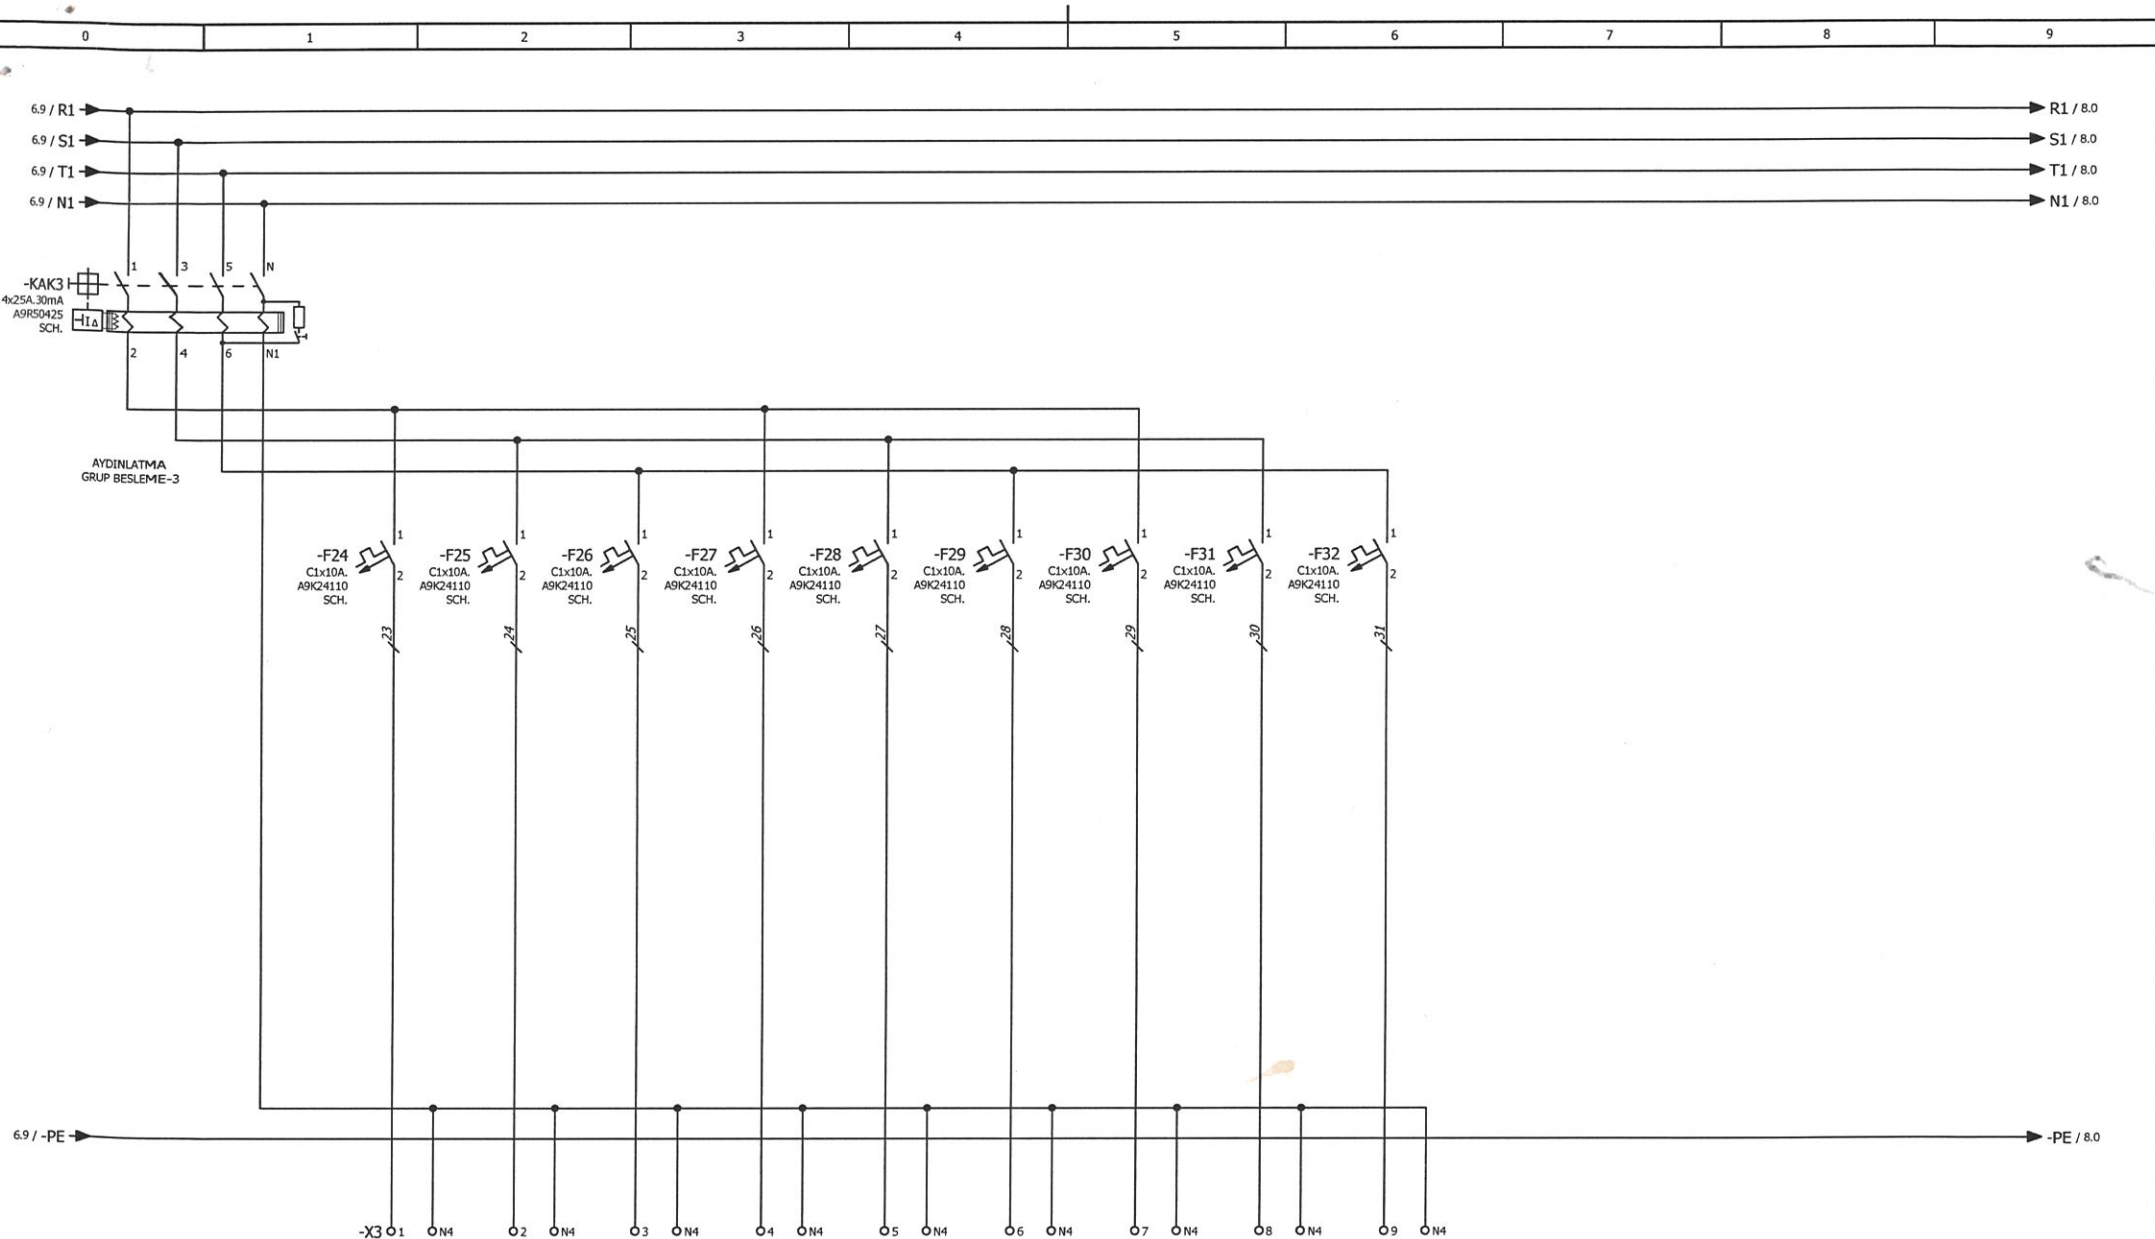


LİNYE NO:	A-19	A-20	A-21	A-22	A-23	A-24	EX-01	-	-
AÇIKLAMA	PLAN KEŞİF	PLAN KEŞİF	PLANLAMA	PLANLAMA	ERKEK WC	ERKEK WC	KORİDOR	KÜÇÜK YEDEK	BÜYÜK YEDEK
KABLO	3x2.5mm ² NHDMH	3x2.5mm ² NHDMH	3x2.5mm ² NHDMH	3x2.5mm ² NHDMH	3x2.5mm ² NHDMH	3x2.5mm ² NHDMH	3x2.5mm ² NHDMH	3x2.5mm ² NHDMH	3x2.5mm ² NHDMH
GÜÇ (W)	60	120	200	72	42	60	88	-	-

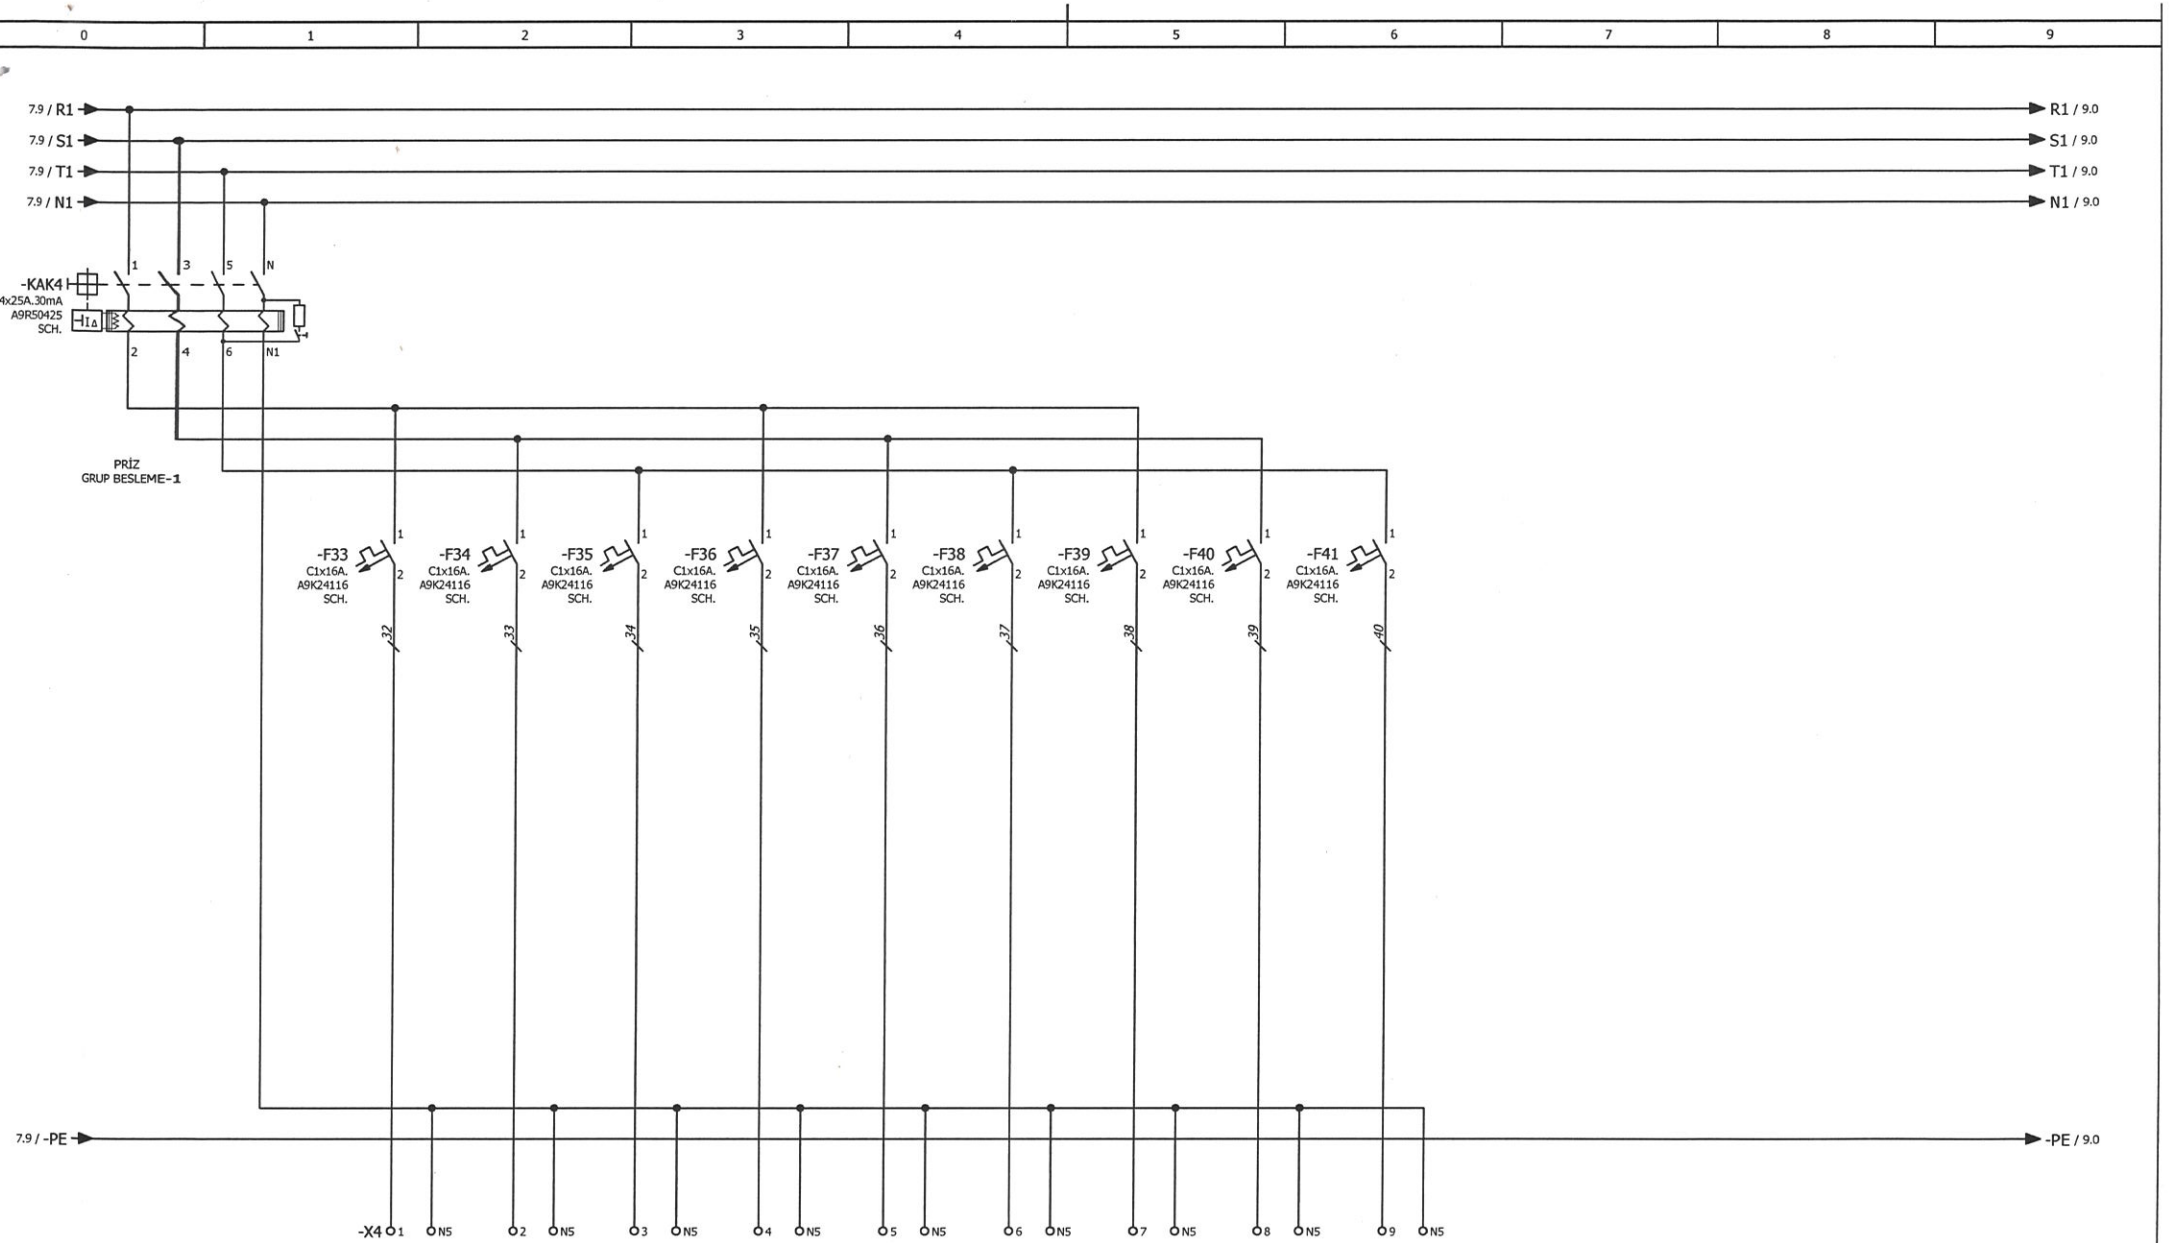


LİNYE NO:	P01	P02	P03	P04	P05	P06	P07	P08	P09
AÇIKLAMA	TOPLANTI ODASI	KORİDOR TEMİZLİK PRİZLERİ	ÜRETİM KALİTE KONTROL	ÜRETİM KALİTE KONTROL	ÜRETİM KALİTE KONTROL	ÜRETİM KALİTE KONTROL	ÜRETİM KALİTE KONTROL	ÜRETİM KALİTE KONTROL	ÜRETİM KALİTE KONTROL
KABLO	3x2.5mm ² NHXMH	3x2.5mm ² NHXMH	3x2.5mm ² NHXMH	3x2.5mm ² NHXMH	3x2.5mm ² NHXMH	3x2.5mm ² NHXMH	3x2.5mm ² NHXMH	3x2.5mm ² NHXMH	3x2.5mm ² NHXMH
GÜÇ (W)	2100	2400	1200	2100	1800	1800	1200	1200	2100

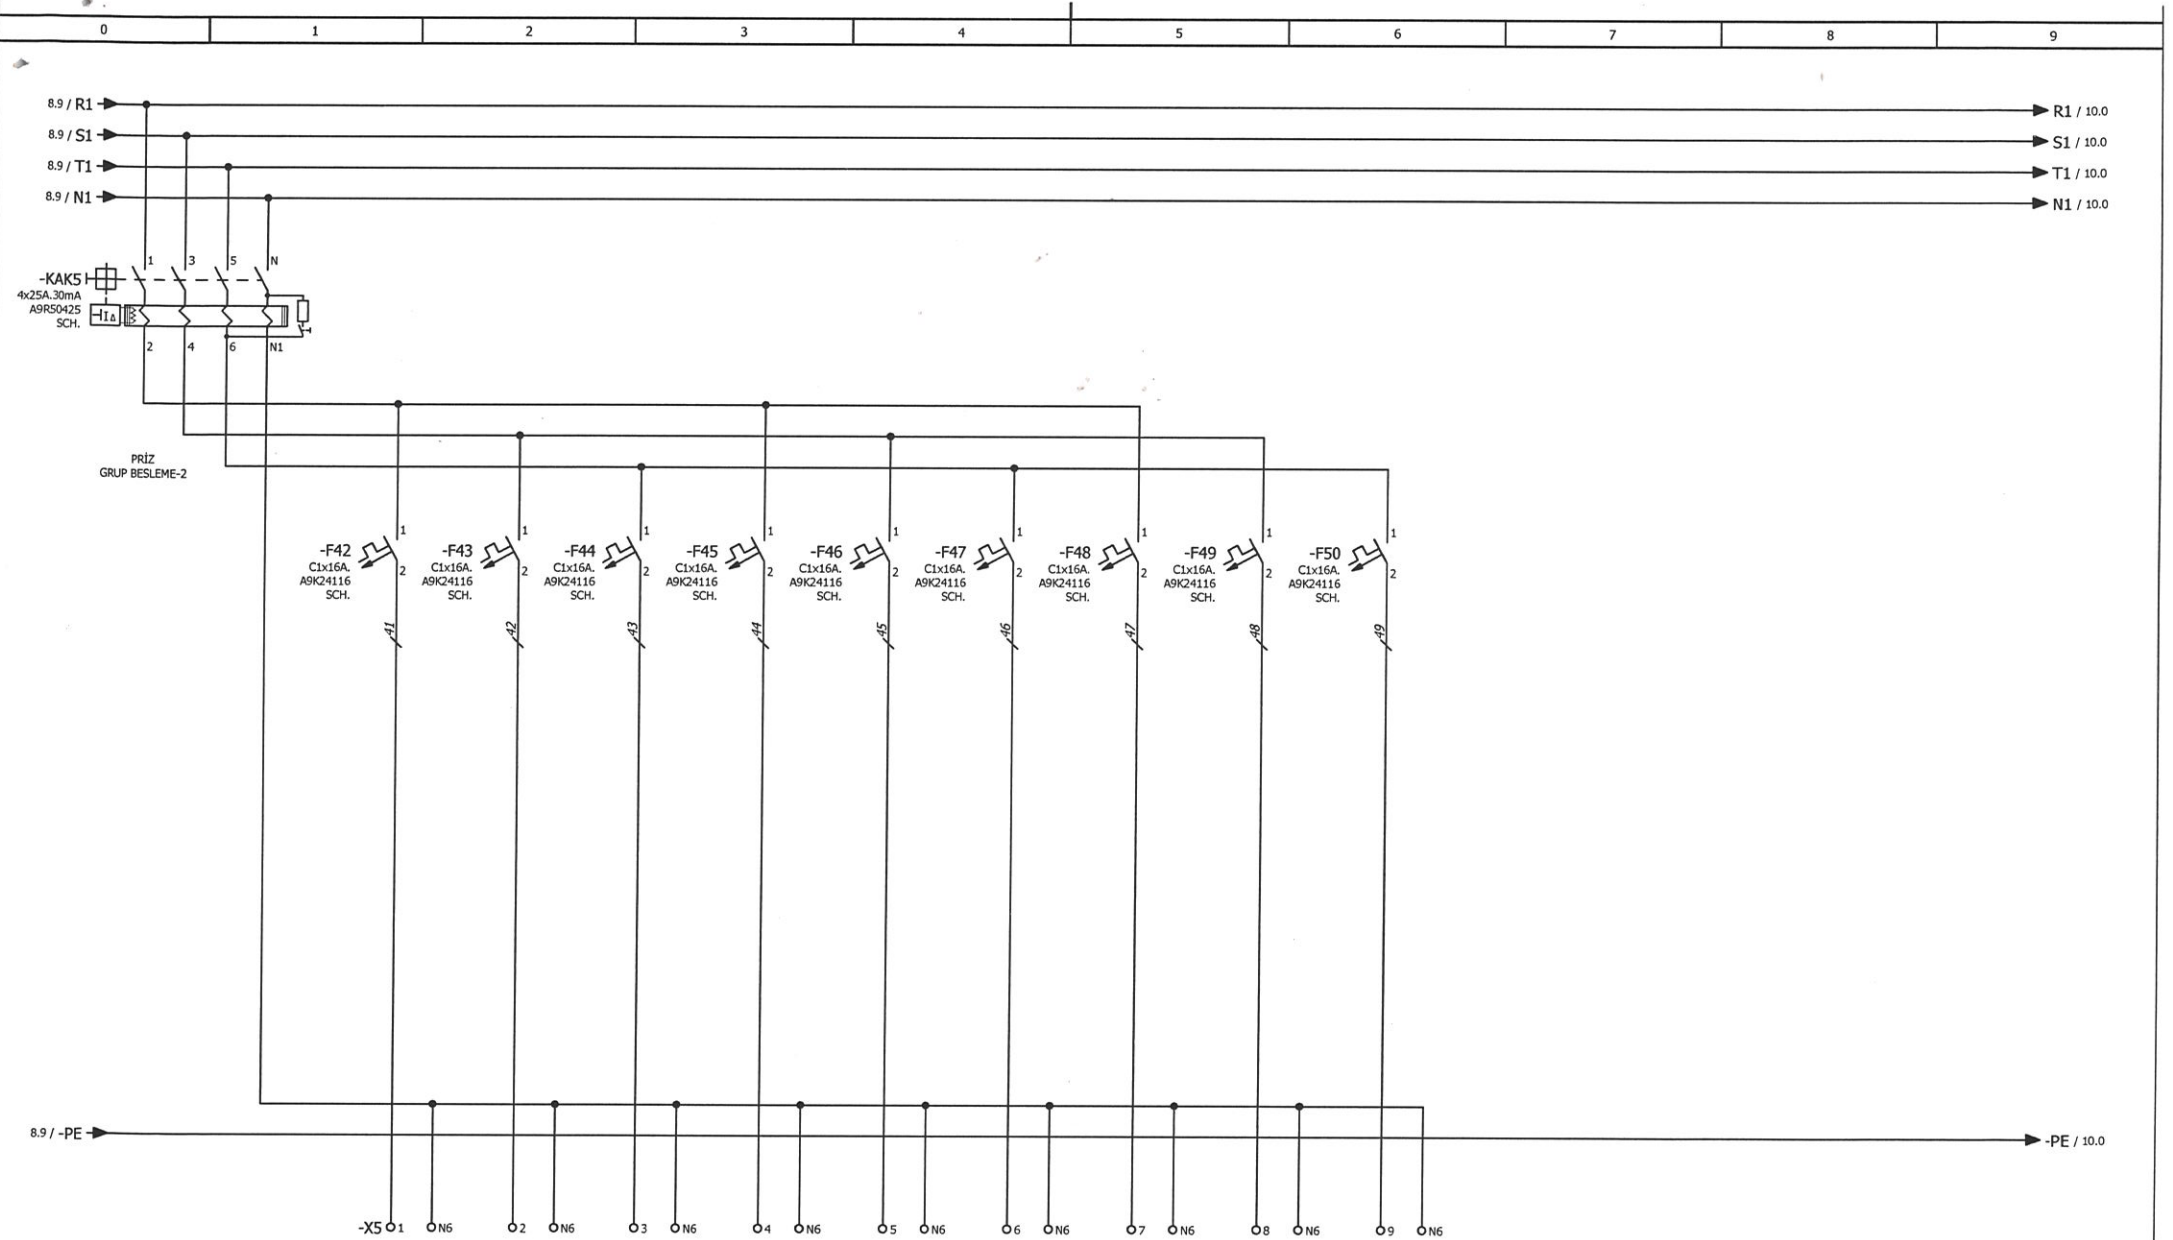


LİNYE NO:	P10	P11	P12	P13	P14	P15	P16	P17	P18
AÇIKLAMA	ÜRETİM KALİTE KONTROL	DİZAYN	DİZAYN	DİZAYN	DİZAYN	YÖNETİM& İCRA KURULU	TERSANE MÜDÜRÜ	PAZARLAMA	PAZARLAMA
KABLO	3x2.5mm²NHXMH	3x2.5mm²NHXMH	3x2.5mm²NHXMH	3x2.5mm²NHXMH	3x2.5mm²NHXMH	3x2.5mm²NHXMH	3x2.5mm²NHXMH	3x2.5mm²NHXMH	3x2.5mm²NHXMH
GÜÇ (W)	1800	2100	1800	2400	1800	2100	2100	1500	1500

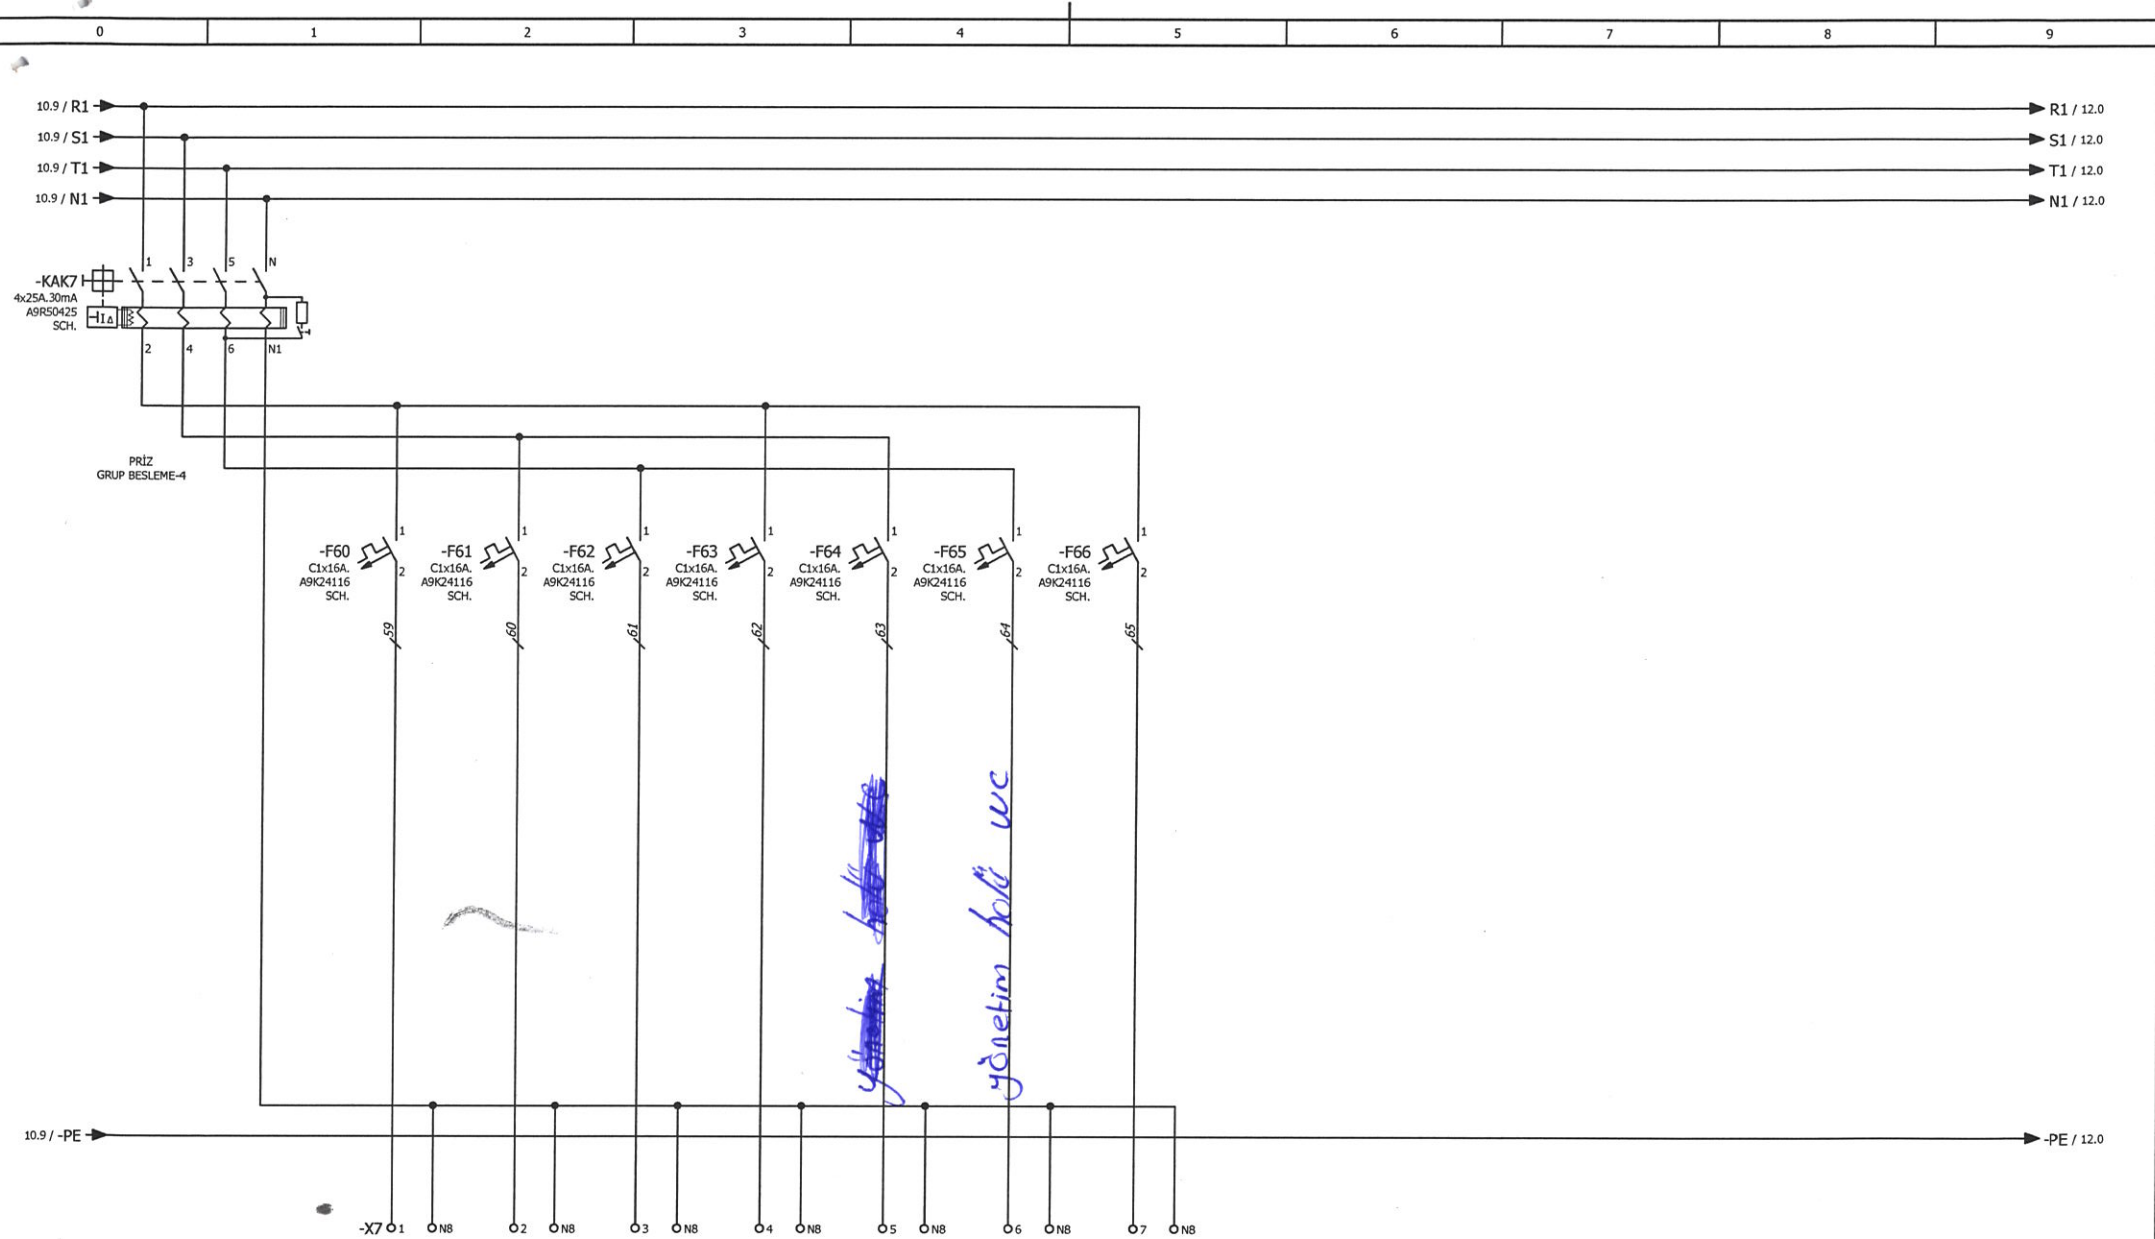

LİNYE NO:	P28	P29	P30	P31	P32	P33	P34
AÇIKLAMA	KİTCHENETTE	KİTCHENETTE	KİTCHENETTE	ERKEK WC	YEDEK	YEDEK	YEDEK
KABLO	3x2.5mm ² NHXMH	3x2.5mm ² NHXMH	3x2.5mm ² NHXMH	3x2.5mm ² NHXMH	-	-	-
GÜÇ (W)	900	2900	2900	3300	-	-	-

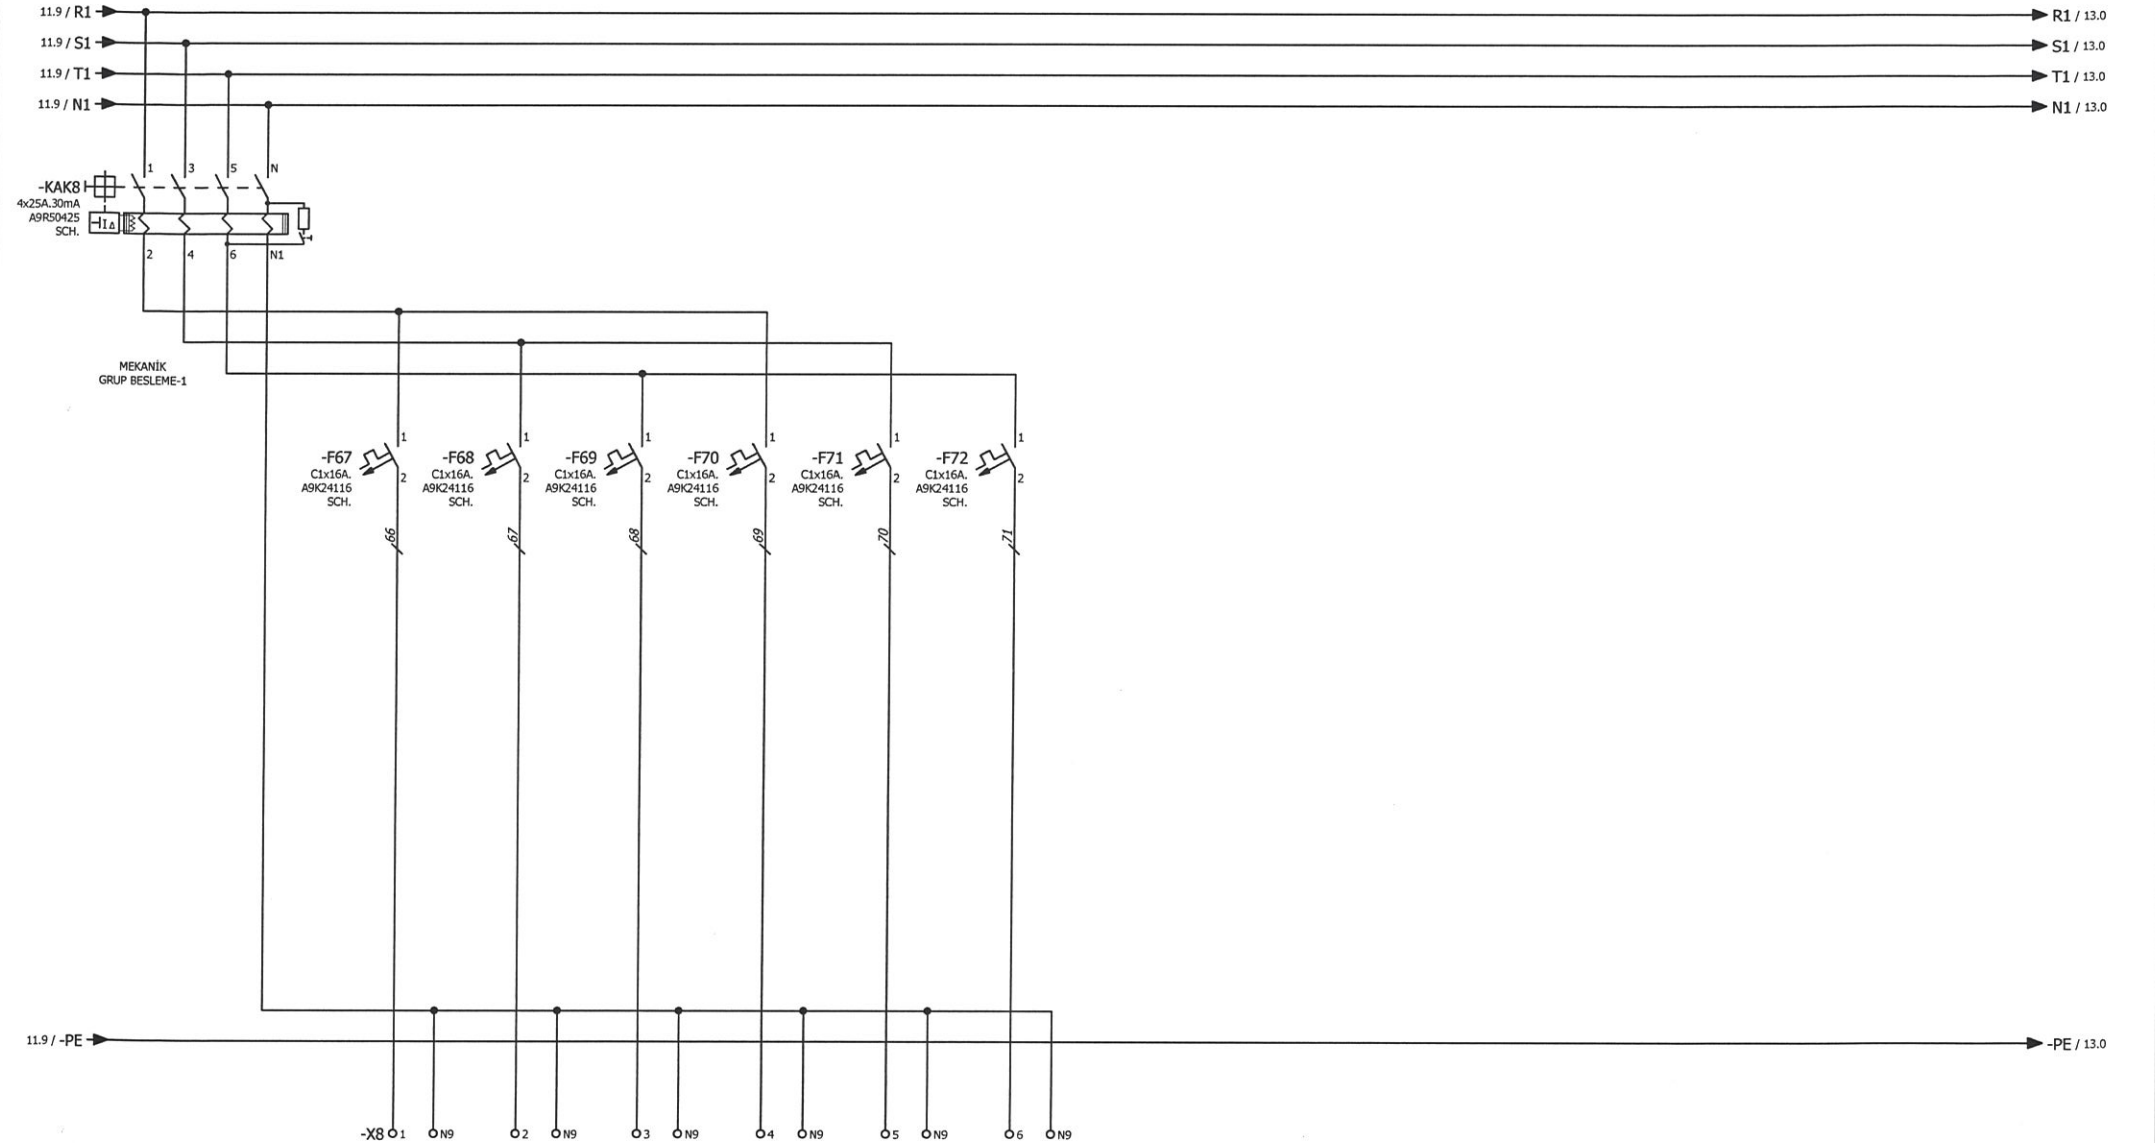

LİNYE NO:	M01	M02	M03	M04	M05	M06
AÇIKLAMA	VRF İÇ ÜNİTE-1	VRF İÇ ÜNİTE-2	VRF İÇ ÜNİTE-3	VRF İÇ ÜNİTE-4	VRF İÇ ÜNİTE-5	VRF İÇ ÜNİTE-6
KABLO	3x2.5mm ² NHXMH	3x2.5mm ² NHXMH	3x2.5mm ² NHXMH	3x2.5mm ² NHXMH	3x2.5mm ² NHXMH	3x2.5mm ² NHXMH
GÜÇ (W)	410	820	820	1870	410	1900

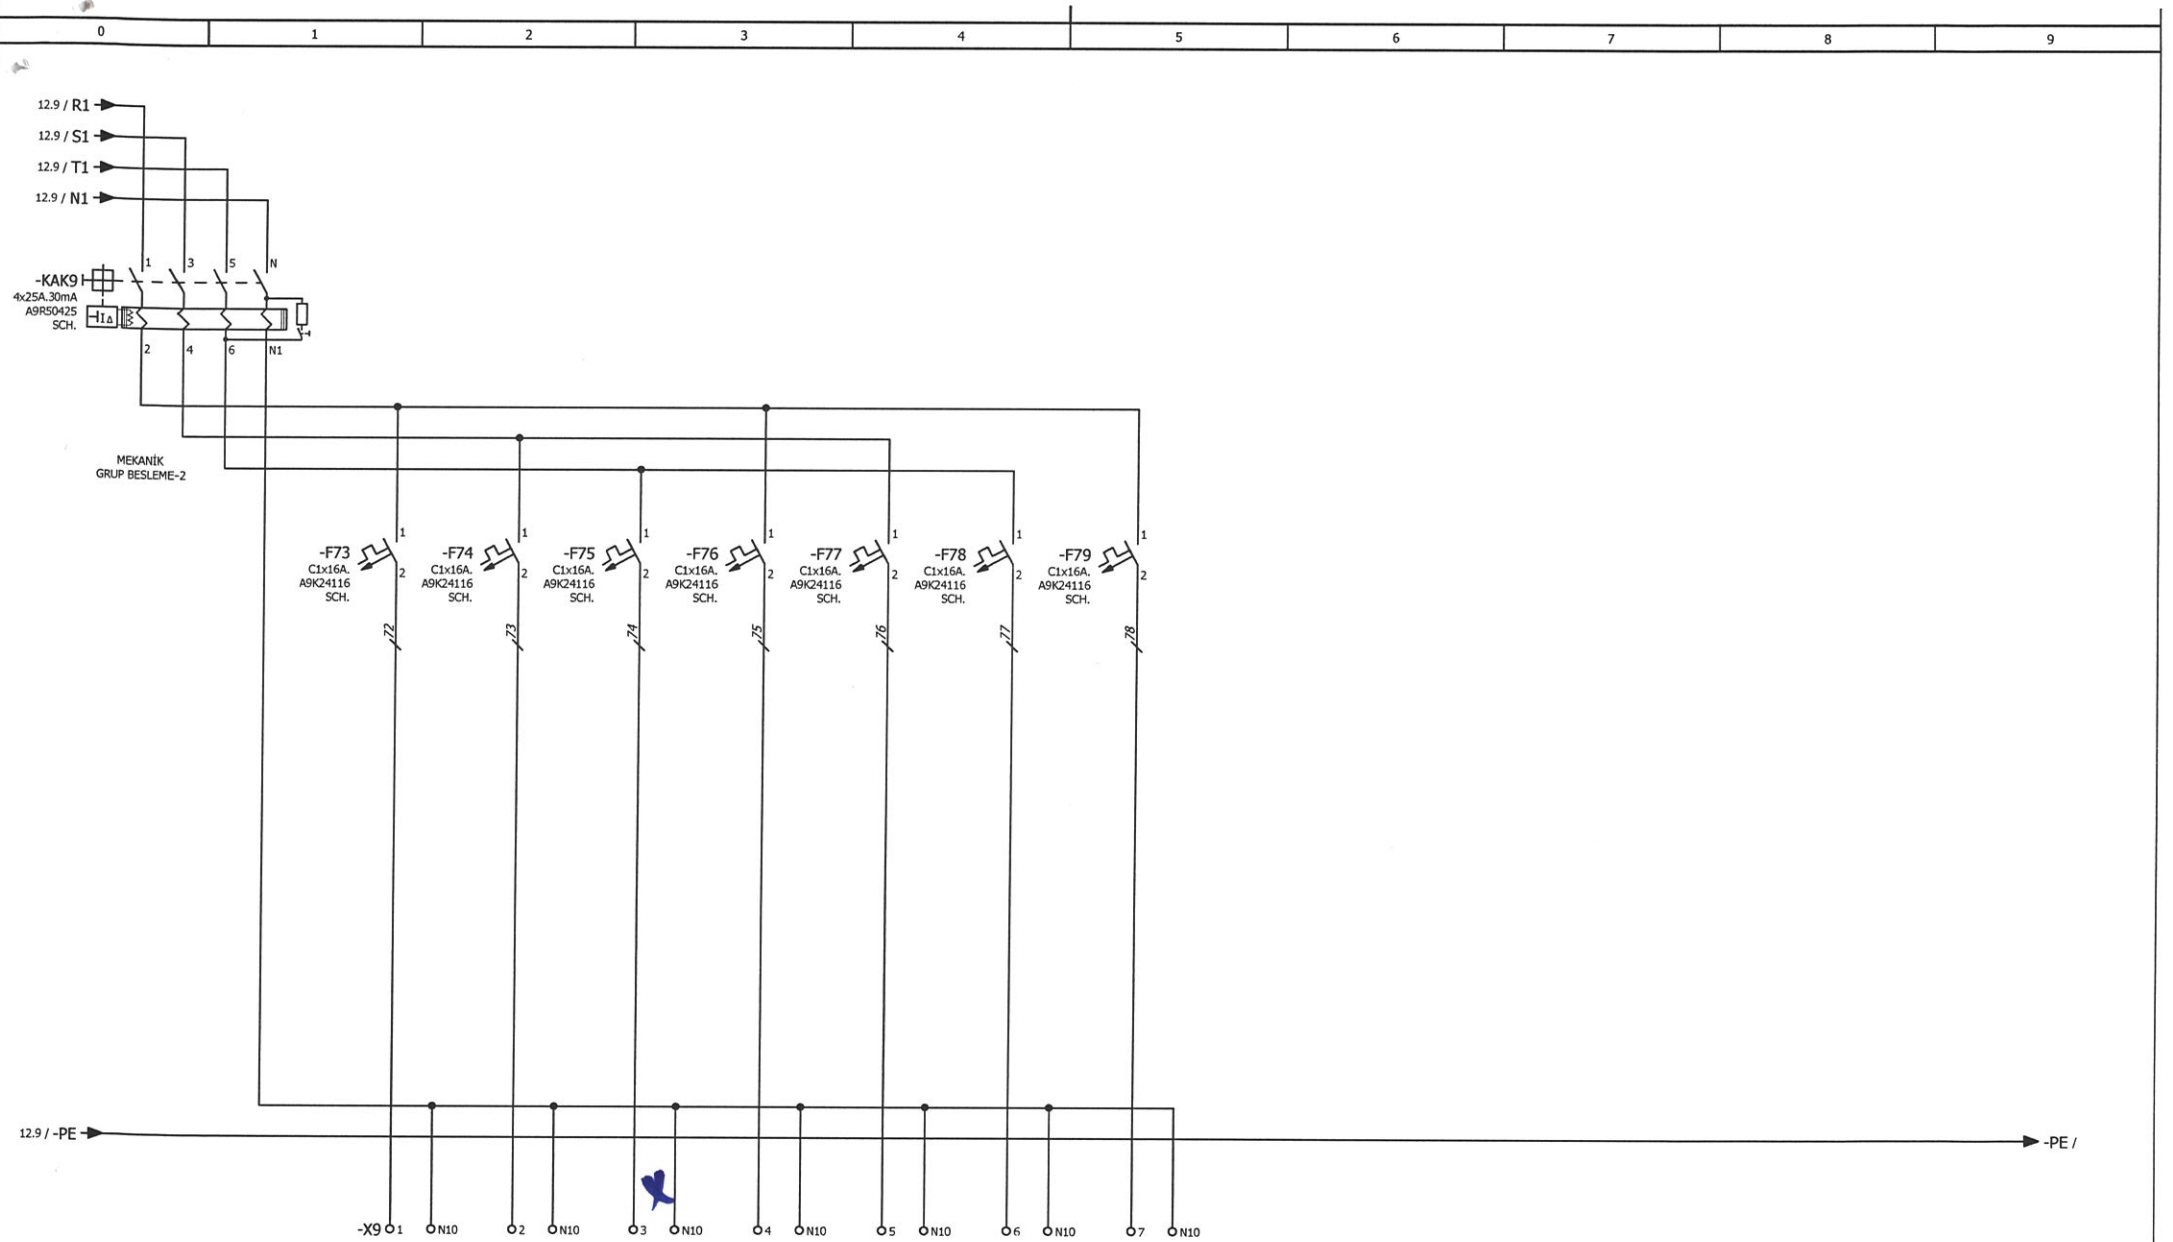

LİNYE NO:	M07	M08	M09	M10	M11	M12	M13
AÇIKLAMA	VRF İÇ ÜNİTE-7	VRF İÇ ÜNİTE-8	VRF İÇ ÜNİTE-9	VRF İÇ ÜNİTE-10	MOTORLU YANGIN DAMPERİ	YEDEK Satın alma	YEDEK
KABLO	3x2.5mm ² NHXMH	3x2.5mm ² NHXMH	3x2.5mm ² NHXMH	3x2.5mm ² NHXMH	3x2.5mm ² NHXMH	3x2.5mm ² NHXMH	3x2.5mm ² NHXMH
GÜÇ (W)	450	410	460	1230	60	-	-

0

1

2

3

4

5

6

7

8

9

Parça Listesi

No:	Malzeme Tanımı	Miktar
1		0
2	3x125A.TMŞ. C16F3TM125 SCH.	1
3	4x25A.30mA A9R50425 SCH.	9
4	30F2GL 1x2A.BUŞON SİGORTA	1
5	C1x6A.10kA A9F84106 SCH.	4
6	C1x10A. A9K24110 SCH.	27
7	C1x16A. A9K24116 SCH.	47
8	GAVE KARTUŞ SİG. YUV. GV 211 1x2A.	1
9	KAPI SİVİCİ BS1011	1
10	MX AÇMA BOBİNİ LV429387 SCH.	1
11	PANO İÇİ AYD. T5 8W	1
12	R X35DL3030R102 KAK RÖLESİ FRER.	1
13	TOROID TDC060 60mm.	1
14	XB5AS8442 ACİL STOP ZBE101	1
15	YEŞİL SİNYAL AD22-220Y	3
16	ZBE101	2
17	ZBE101 KONTAK	1