


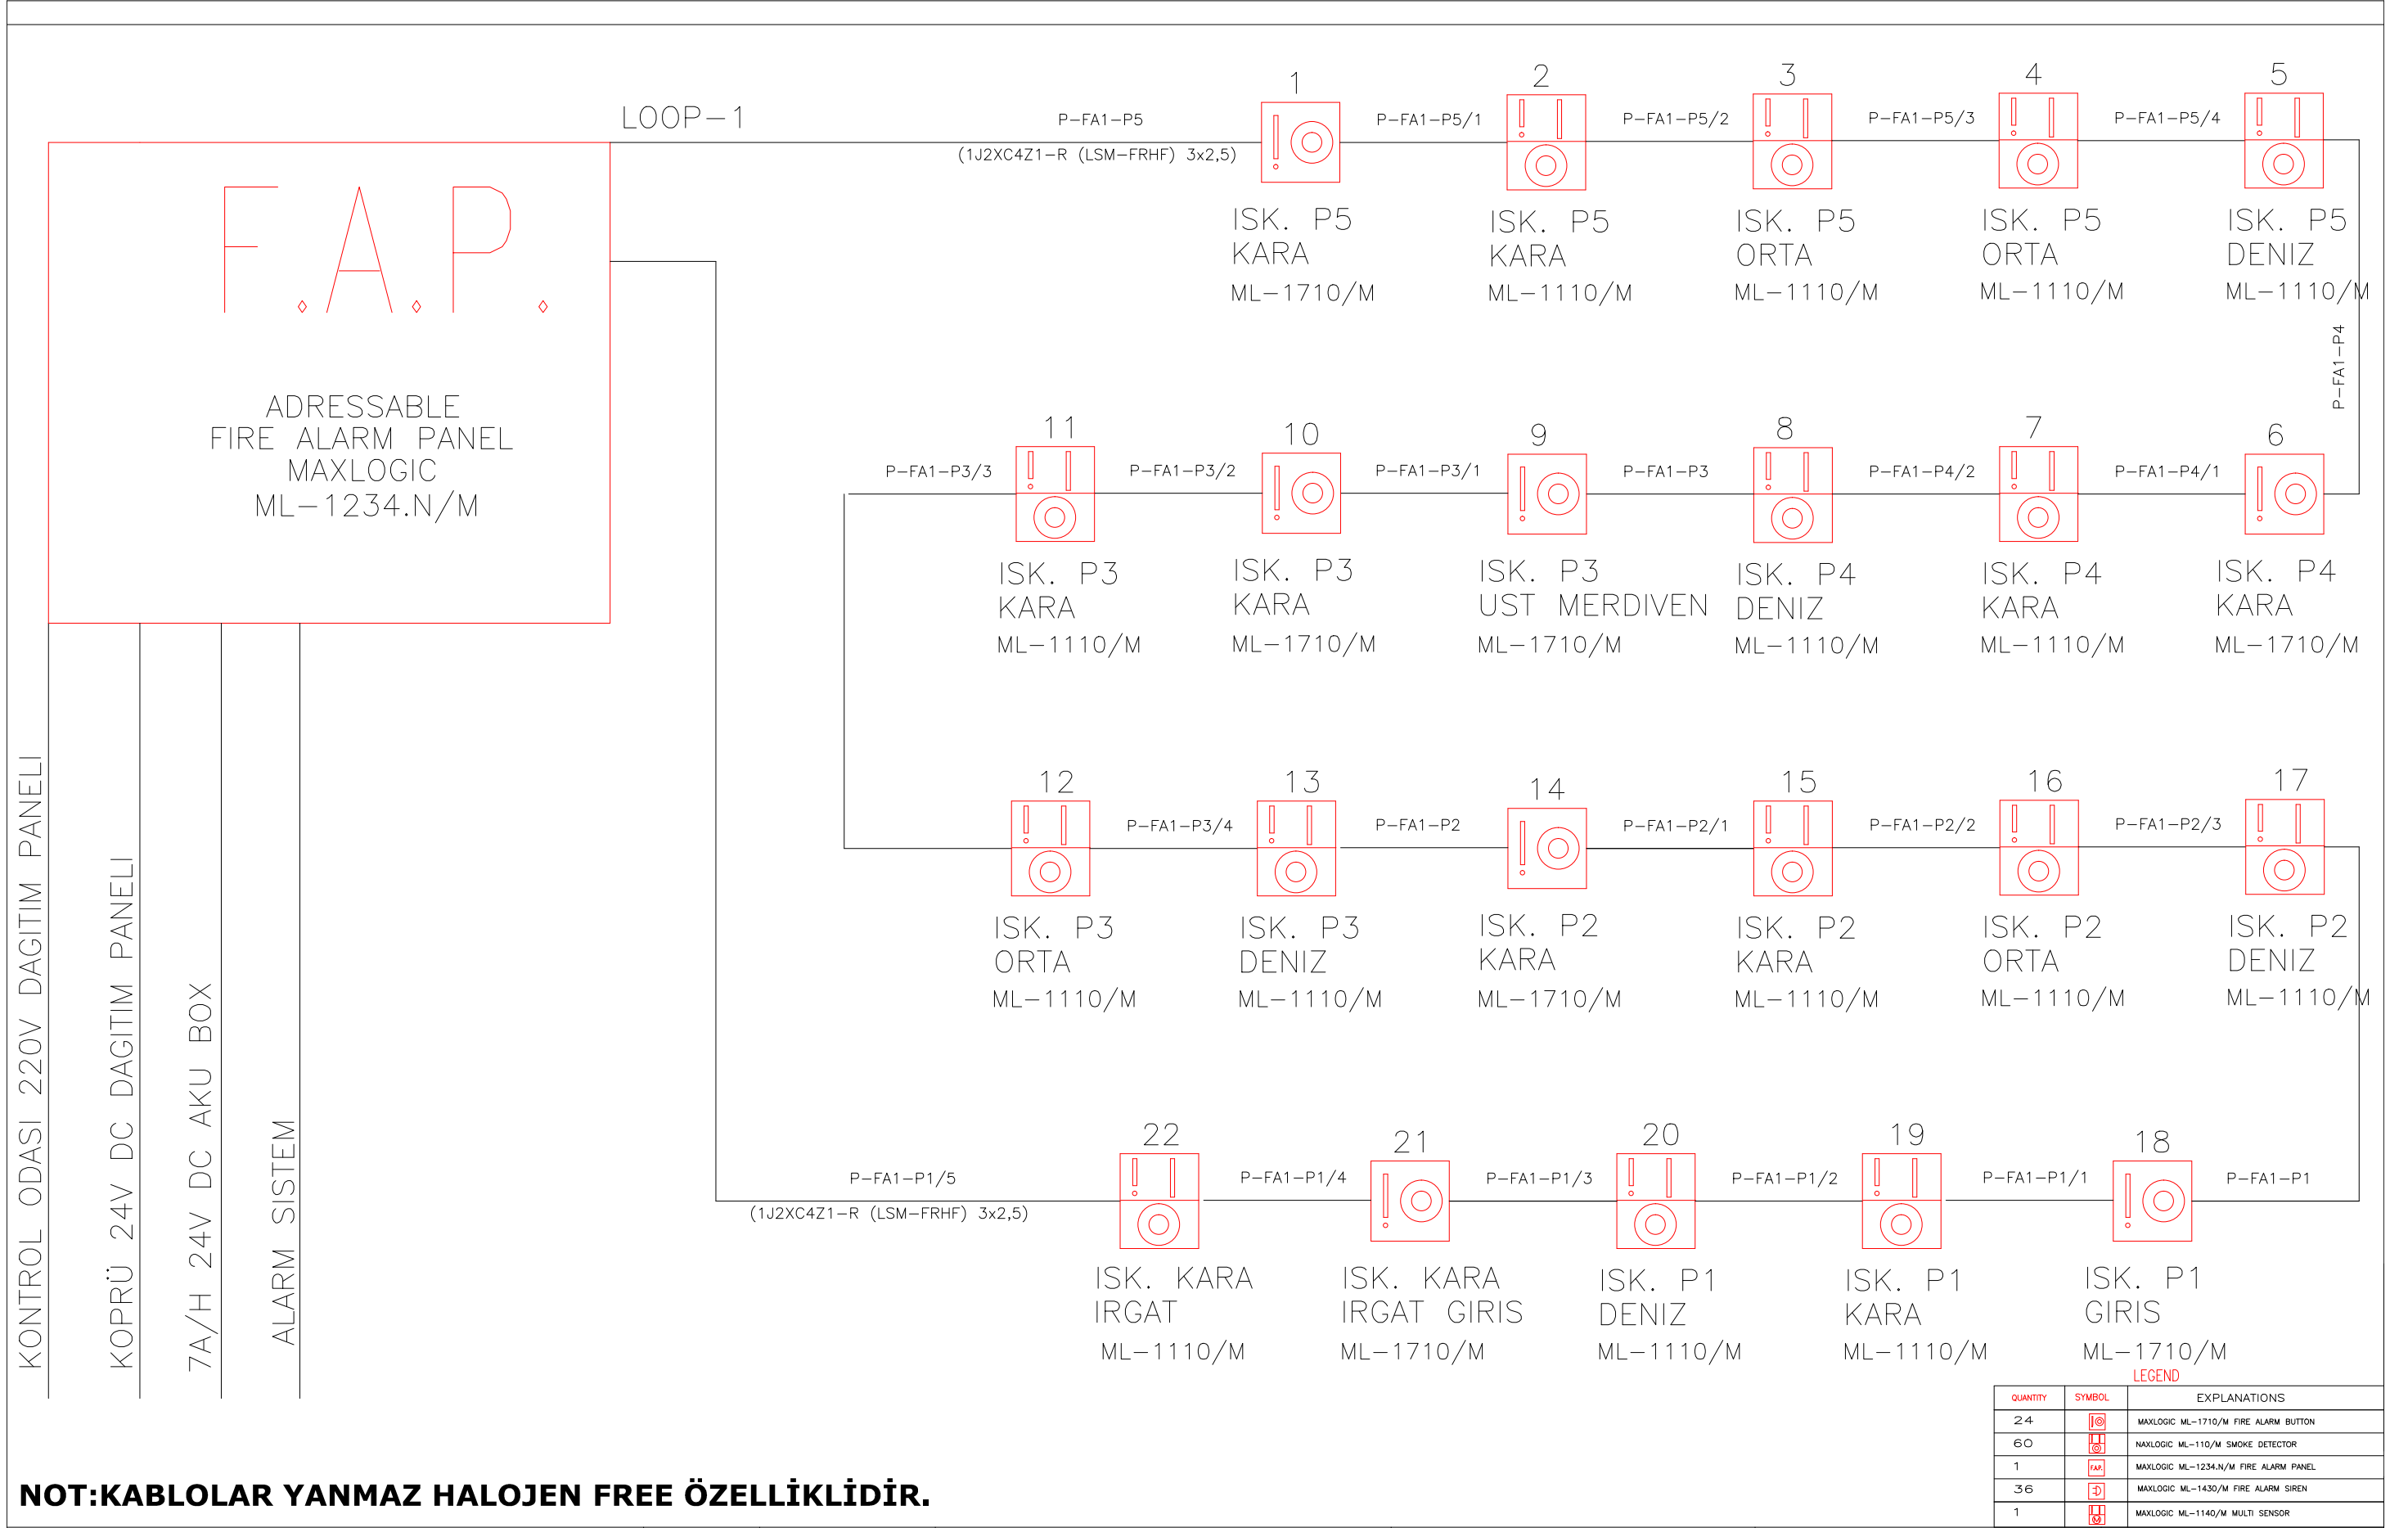

NOT:KABLolar YANMAZ HALOJEN FREE ÖZELLİKLİDİR.



HİLAL GEMİ MUHENDİSLİK
ELEKTRİK DONANIM VE OTOMASYON SAN.TİC. LTD. STİ
Aydıntepe mah. İbrahim Koray sok. No:20/2-3 TUZLA/İSTANBUL
Tel:0216 395 60 50 GSM:0530 602 98 77
www.hilalgemi.com

DATE	26,01,2023
DRAWN BY	SULEYMAN SANCAK
CHECKED BY	YUSUF BAK

FIRE ALARM SYSTEM SINGLE LINE DIAGRAMI


FLOATING DOCK
BESİKTAS YZH-3

BESİKTAS SHIPYARD


PROJE KOD
CLASS

BE2/HLL003
RINA

+	Page Number	1
	Highest Page Number	

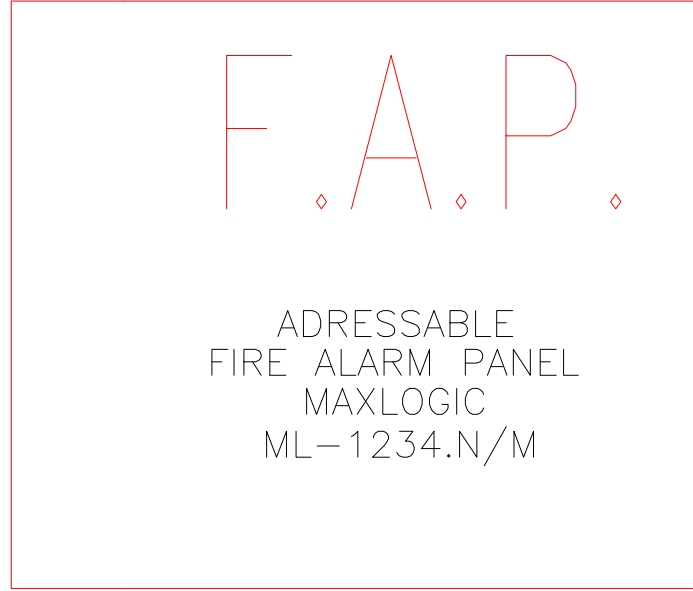

LOOP-2

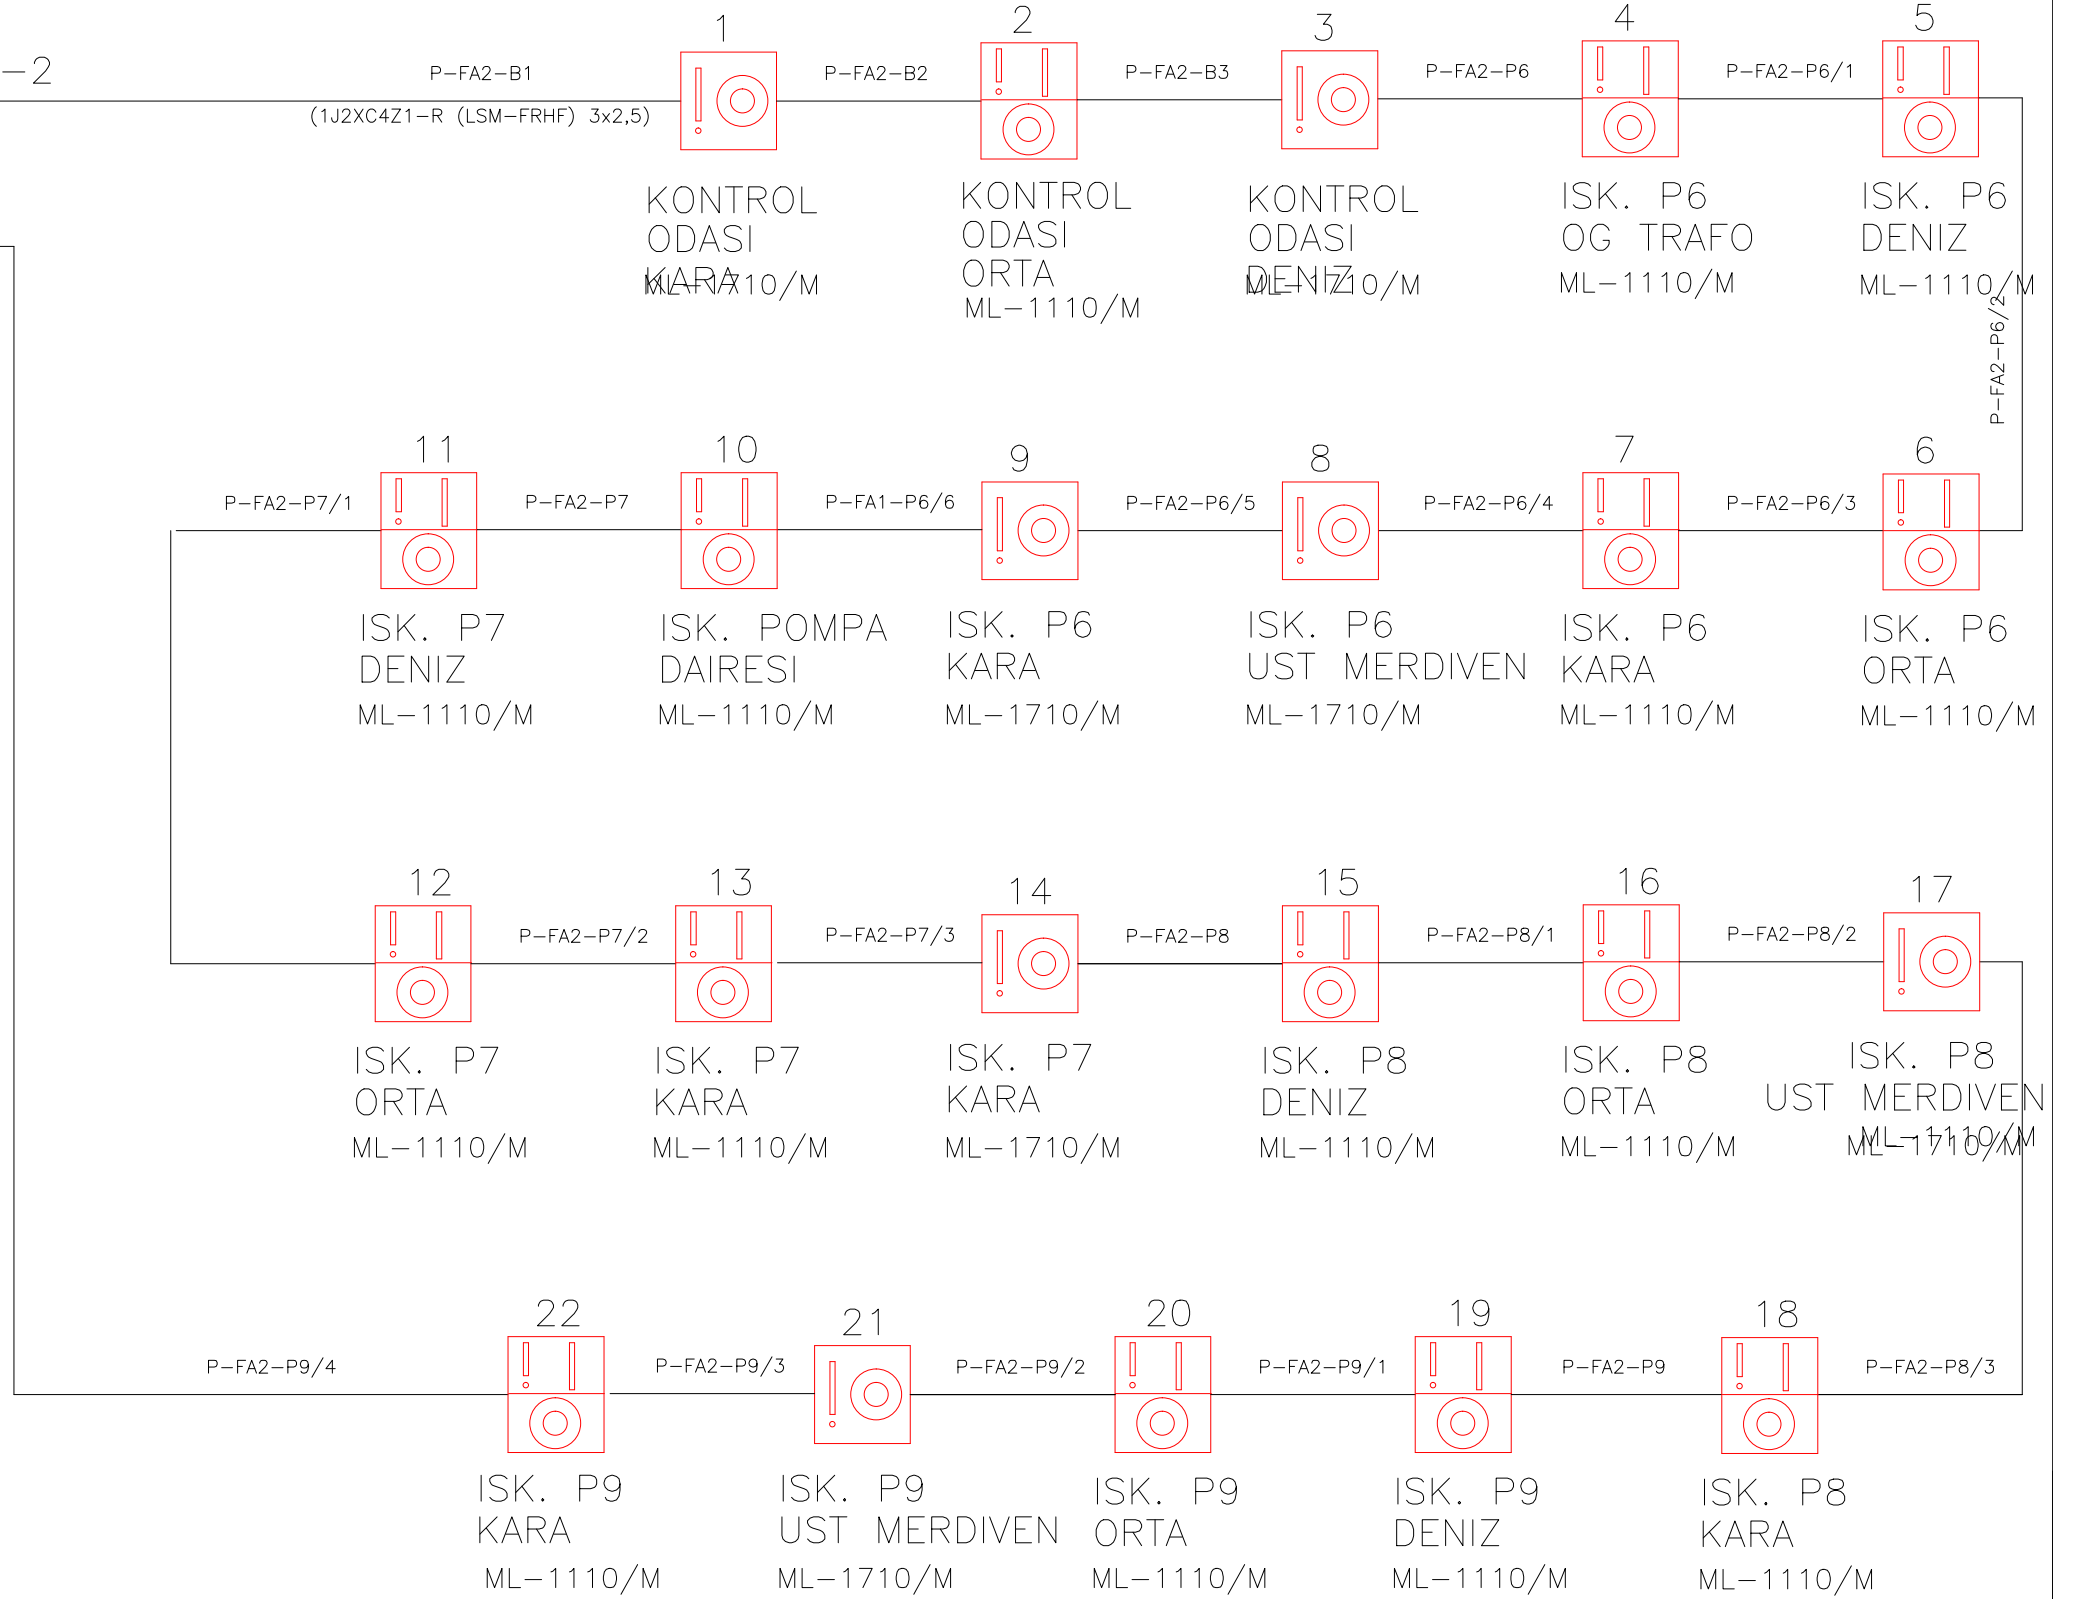

LEGEND

SYMBOL	EXPLANATIONS
	MAXLOGIC ML-1710/M FIRE ALARM BUTTON
	MAXLOGIC ML-110/M SMOKE DETECTOR
	MAXLOGIC ML-1234.N/M FIRE ALARM PANEL
	MAXLOGIC ML-1430/M FIRE ALARM SIREN
	MAXLOGIC ML-1140/M MULTI SENSOR

NOT:KABLolar YANMAZ HALOJEN FREE ÖZELLİKLİDİR.



HİLAL GEMİ MUHENDİSLİK
ELEKTRİK DONANIM VE OTOMASYON SAN.TİC. LTD. STİ
Aydıntepe mah. İbrahim Koray sok. No:20/2-3 TUZLA/İSTANBUL
Tel:0216 395 60 50 GSM:0530 602 98 77
www.hilalgemi.com

DATE	26,01,2023
DRAWN BY	SULEYMAN SANCAK
CHECKED BY	YUSUF BAK


FIRE ALARM SYSTEM SINGLE LINE DIAGRAMI

FLOATING DOCK
BESİKTAS YZH-3


BESİKTAS SHIPYARD

PROJE KOD	BE2/HLL003
CLASS	RINA

+	Page Number	2
	Highest Page Number	6

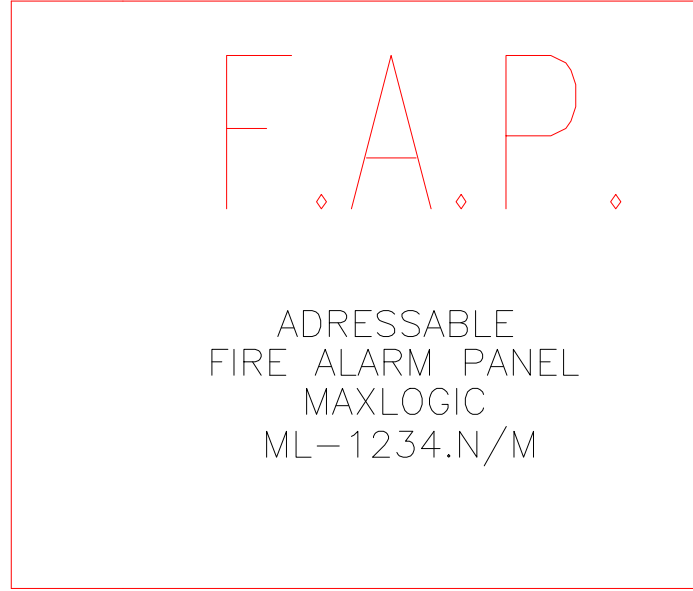

LOOP-3

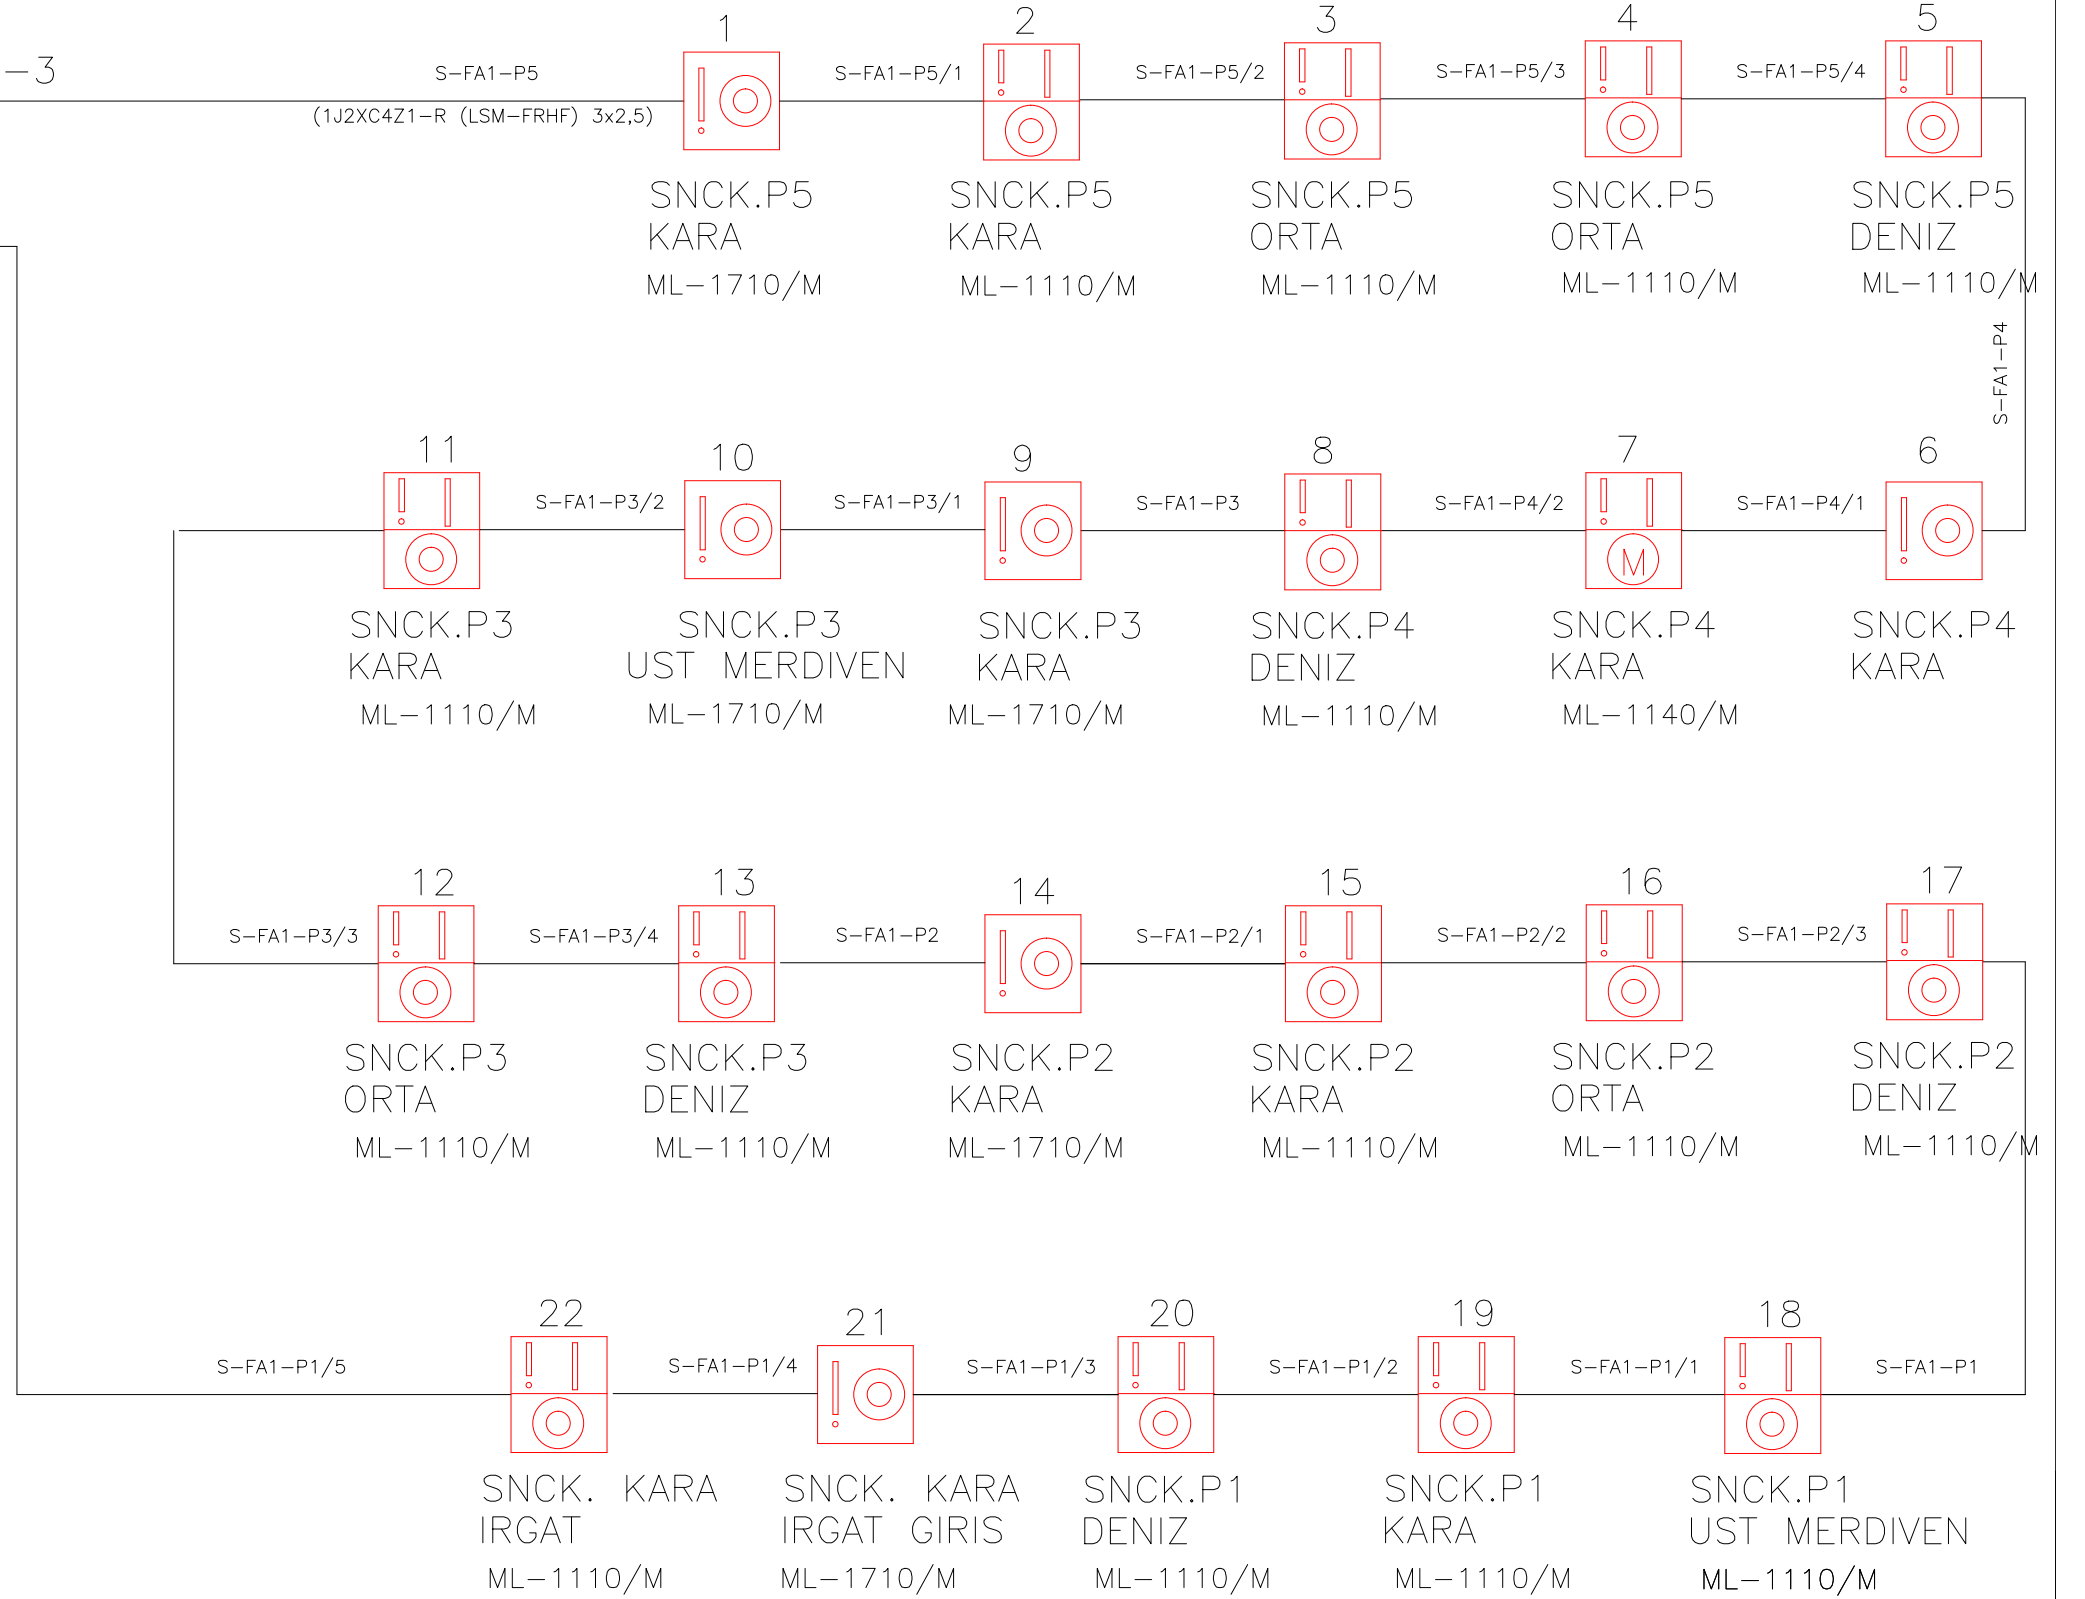

LEGEND

SYMBOL	EXPLANATIONS
	MAXLOGIC ML-1710/M FIRE ALARM BUTTON
	MAXLOGIC ML-110/M SMOKE DETECTOR
	MAXLOGIC ML-1234.N/M FIRE ALARM PANEL
	MAXLOGIC ML-1430/M FIRE ALARM SIREN
	MAXLOGIC ML-1140/M MULTI SENSOR

NOT:KABLolar YANMAZ HALOJEN FREE ÖZELLİKLİDİR.



HİLAL GEMİ MUHENDİSLİK
ELEKTRİK DONANIM VE OTOMASYON SAN.TİC. LTD. STİ
Aydıntepe mah. İbrahim Koray sok. No:20/2-3 TUZLA/İSTANBUL
Tel:0216 395 60 50 GSM:0530 602 98 77
www.hilalgemi.com

DATE	26,01,2023
DRAWN BY	SULEYMAN SANCAK
CHECKED BY	YUSUF BAK


FIRE ALARM SYSTEM SINGLE LINE DIAGRAMI

FLOATING DOCK
BESİKTAS YZH-3


BESİKTAS SHIPYARD

PROJE KOD	BE2/HLL003
CLASS	RINA

Page Number	3
Highest Page Number	6

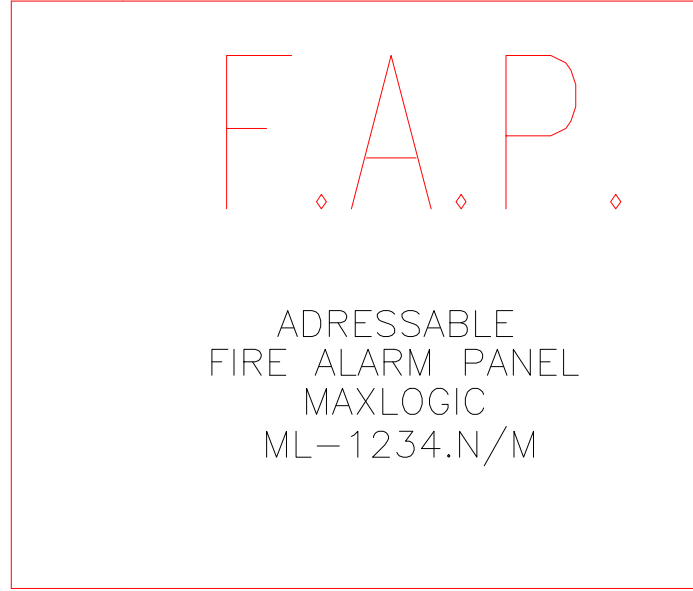

LOOP-4

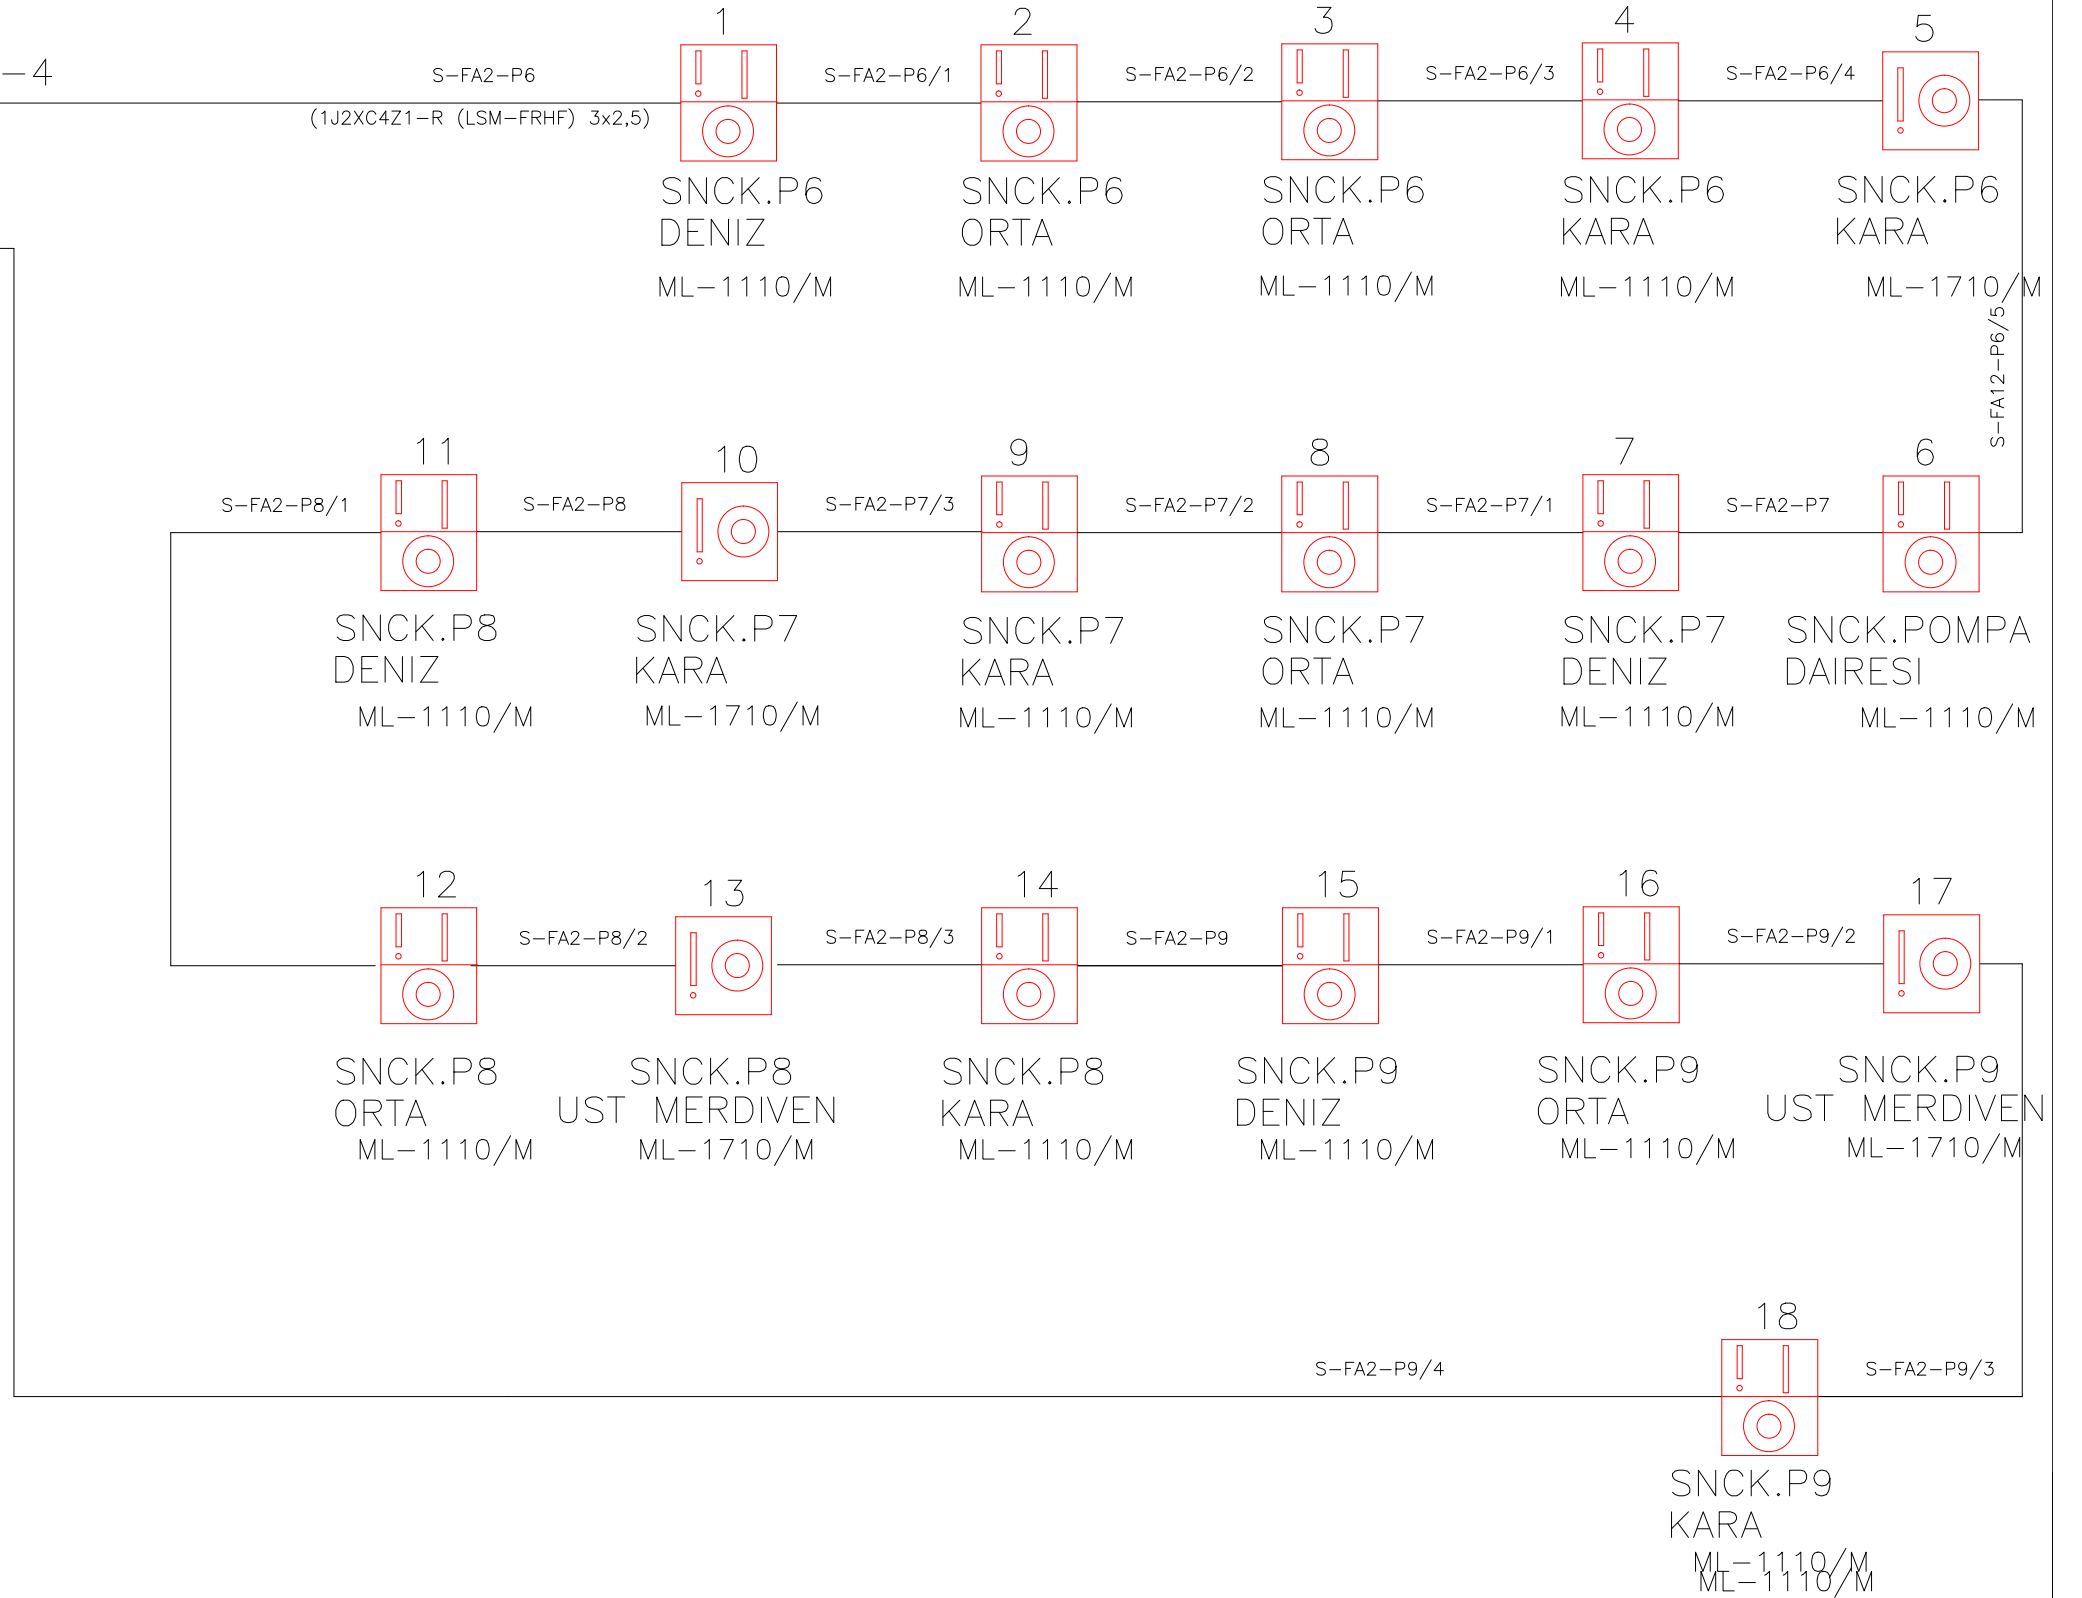

LEGEND	
SYMBOL	EXPLANATIONS
	MAXLOGIC ML-1710/M FIRE ALARM BUTTON
	MAXLOGIC ML-110/M SMOKE DETECTOR
	MAXLOGIC ML-1234.N/M FIRE ALARM PANEL
	MAXLOGIC ML-1430/M FIRE ALARM SIREN
	MAXLOGIC ML-1140/M MULTI SENSOR

NOT:KABLolar YANMAZ HALOJEN FREE ÖZELLİKLİDİR.



HILAL GEMİ MUHENDİSLİK
ELEKTRİK DONANIM VE OTOMASYON SAN.TİC. LTD. STİ
Aydıntepe mah. İbrahim Koray sok. No:20/2-3 TUZLA/İSTANBUL
Tel:0216 395 60 50 GSM:0530 602 98 77
www.hilalgemi.com

DATE	26,01,2023
DRAWN BY	SULEYMAN SANCAK
CHECKED BY	YUSUF BAK



FIRE ALARM SYSTEM SINGLE LINE DIAGRAMI

FLOATING DOCK
BESİKTAS YZH-3

BESİKTAS SHIPYARD

PROJE KOD	BE2/HLL003
CLASS	RINA

+	Page Number	4
	Highest Page Number	6

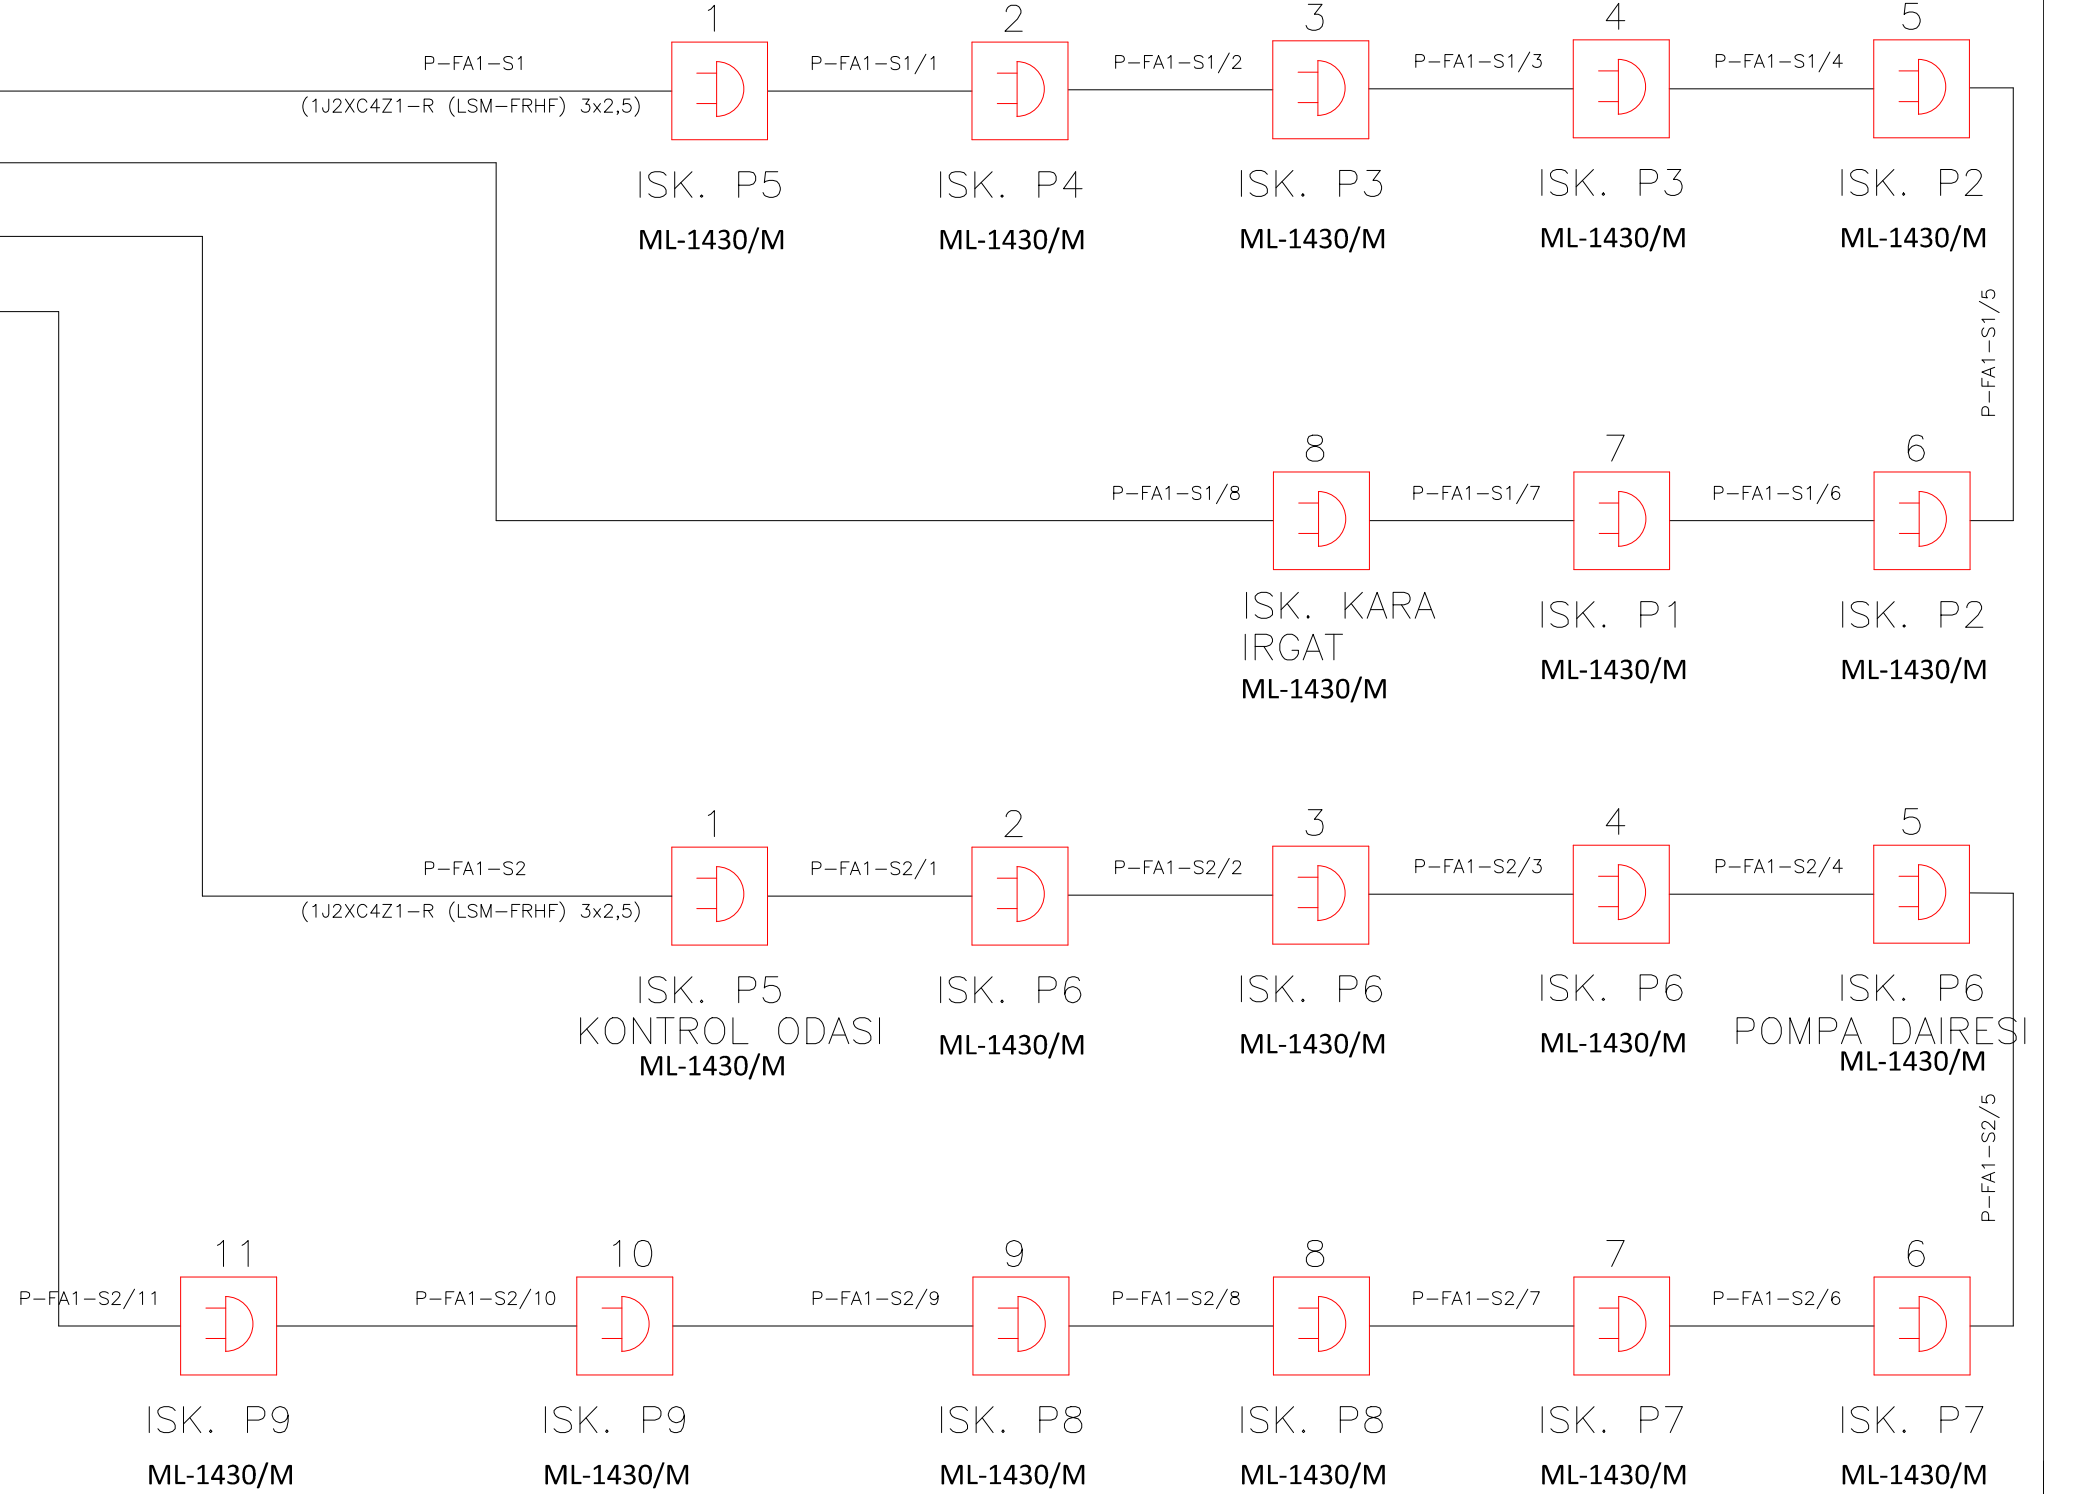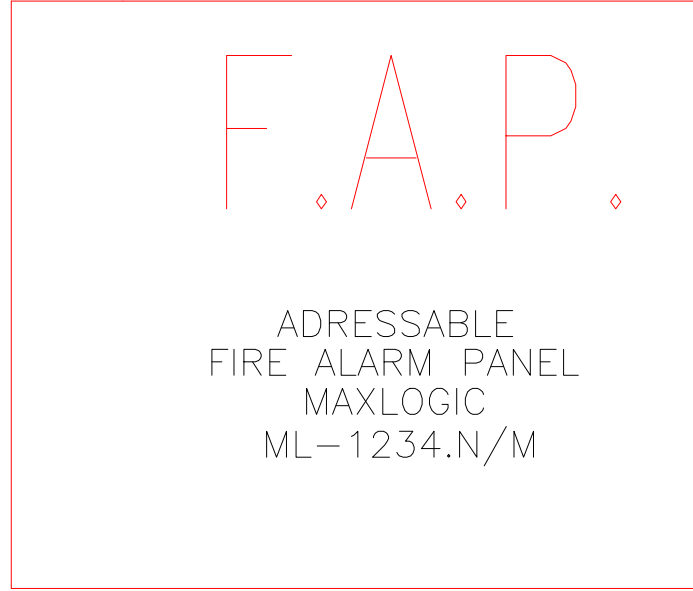

ML-1110/M

LEGEND

SYMBOL	EXPLANATIONS
	MAXLOGIC ML-1710/M FIRE ALARM BUTTON
	MAXLOGIC ML-110/M SMOKE DETECTOR
	MAXLOGIC ML-1234.N/M FIRE ALARM PANEL
	MAXLOGIC ML-1430/M FIRE ALARM SIREN
	MAXLOGIC ML-1140/M MULTI SENSOR

NOT:KABLolar YANMAZ HALOJEN FREE ÖZELLİKLİDİR.



HİLAL GEMİ MUHENDİSLİK
ELEKTRİK DONANIM VE OTOMASYON SAN.TİC. LTD. STİ
Aydıntepe mah. İbrahim Koray sok. No:20/2-3 TUZLA/İSTANBUL
Tel:0216 395 60 50 GSM:0530 602 98 77
www.hilalgemi.com

DATE	26,01,2023
DRAWN BY	SULEYMAN SANCAK
CHECKED BY	YUSUF BAK

FIRE ALARM SYSTEM SINGLE LINE DIAGRAMI

FLOATING DOCK

BESİKTAS YZH-3

BESİKTAS SHIPYARD

PROJE KOD

BE2/HLL003



CLASS

RINA

+

Page Number 5

Highest Page Number 6

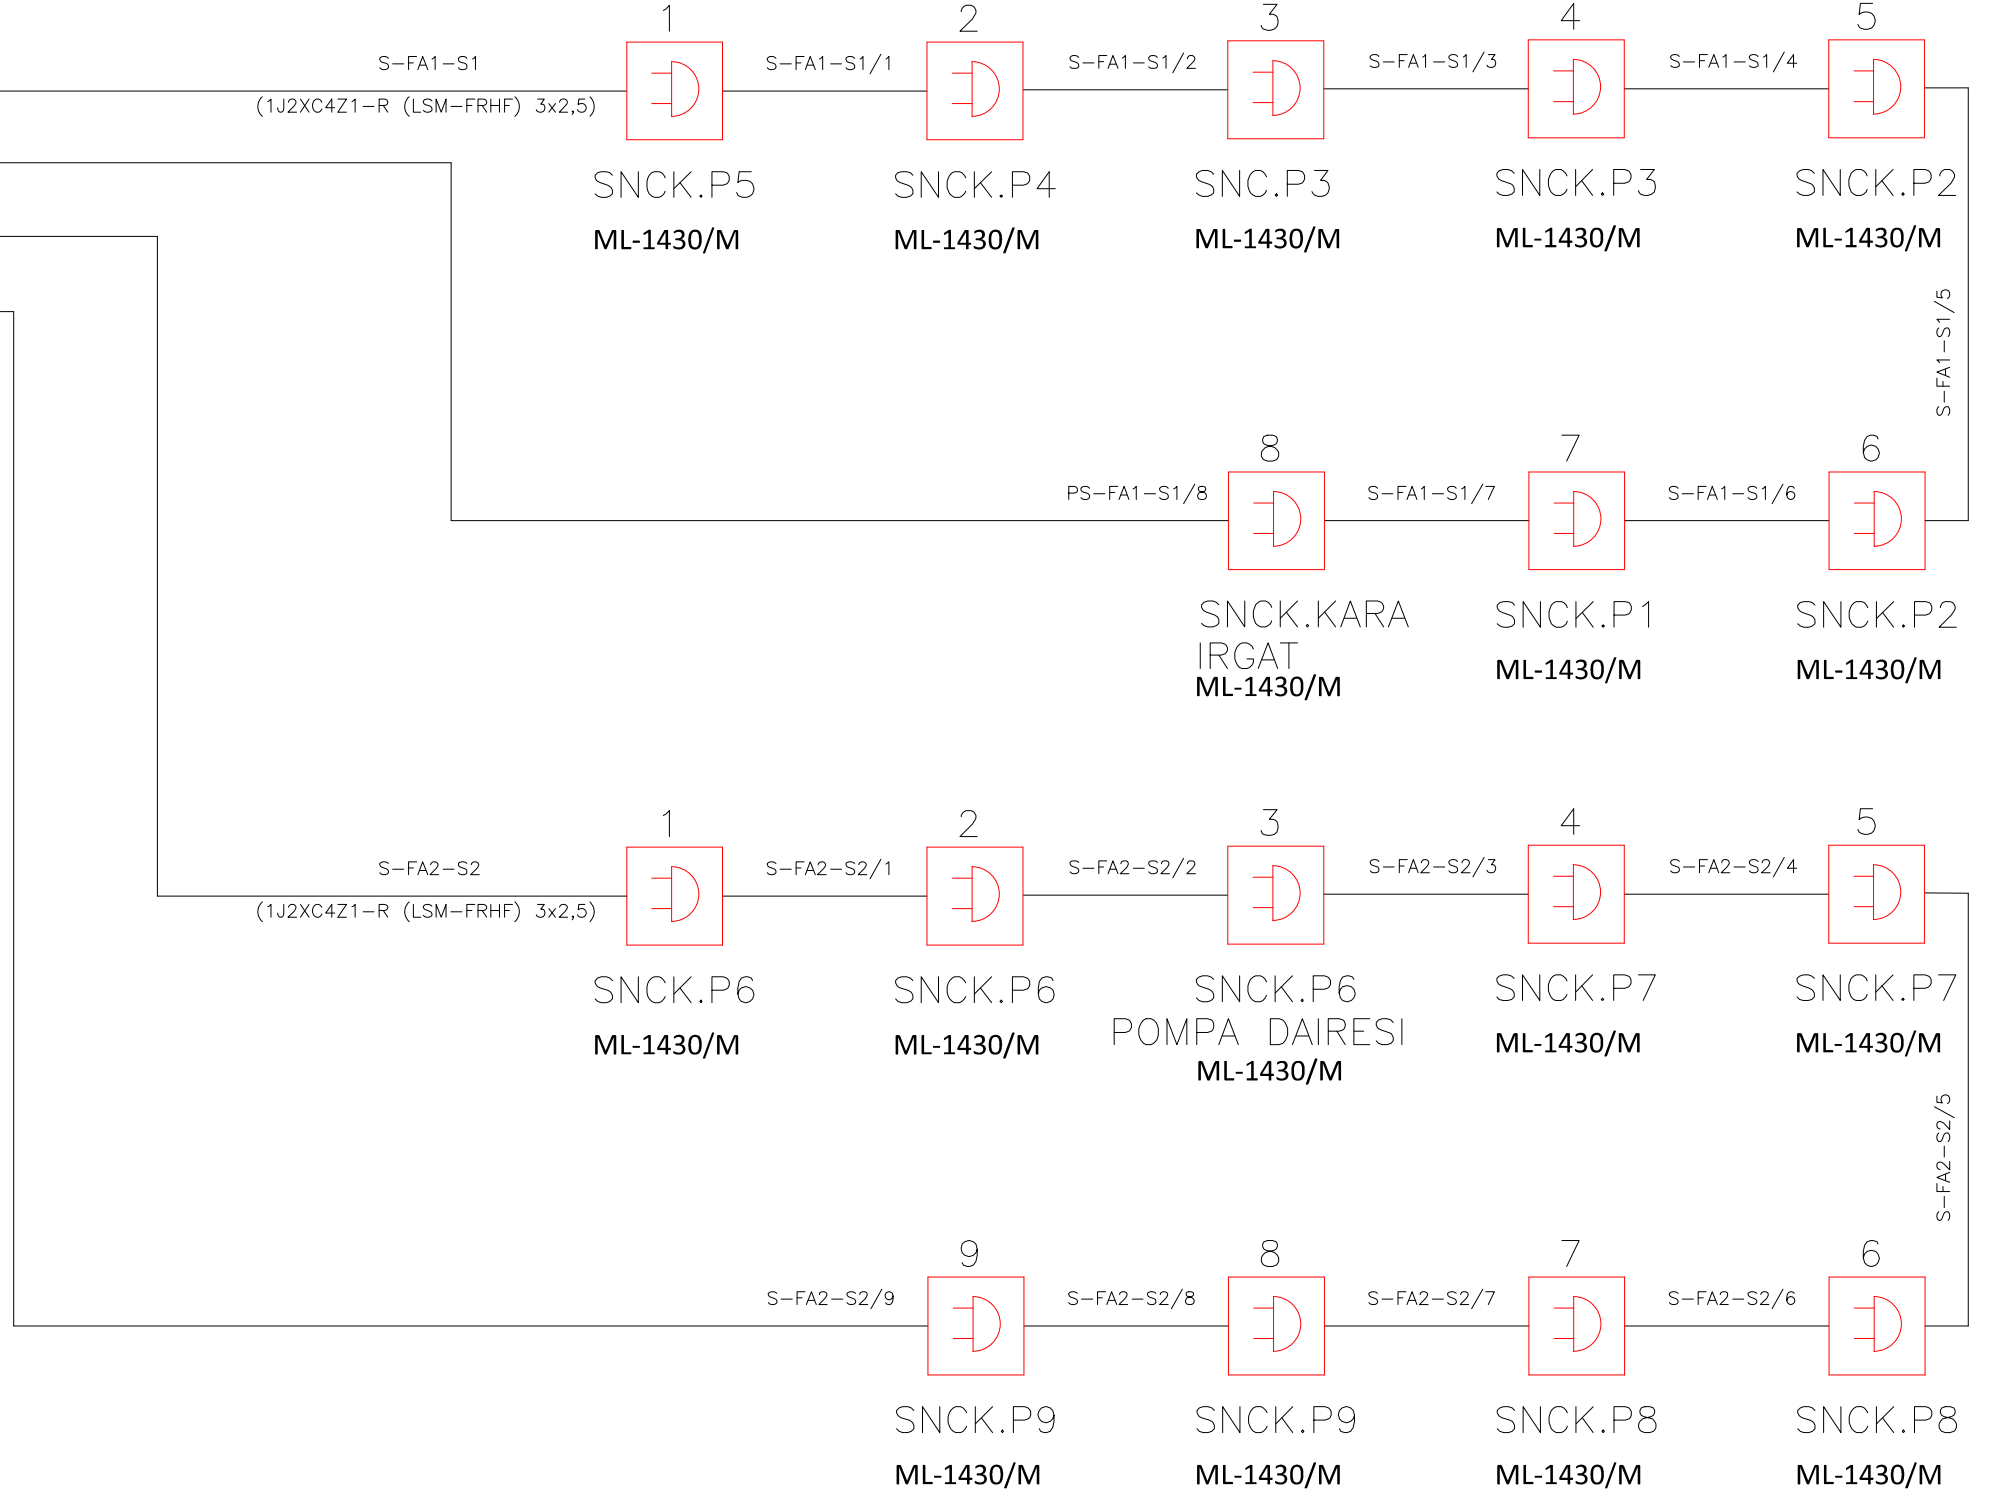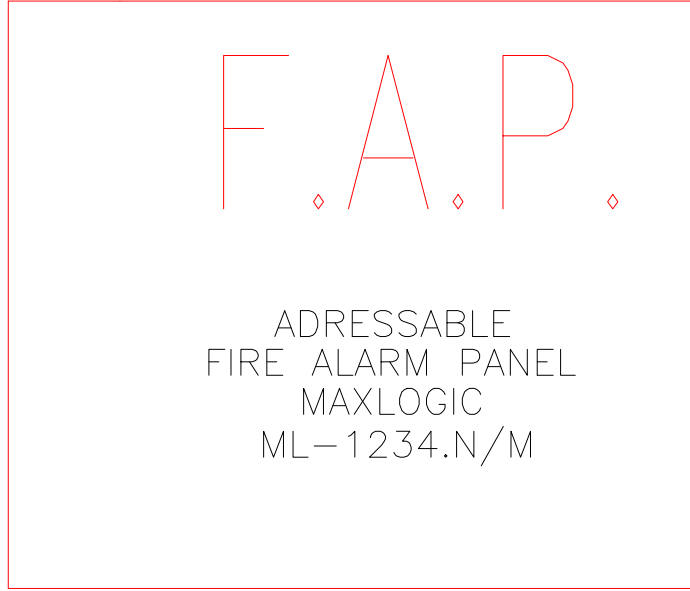

ML-1110/M

LEGEND

SYMBOL	EXPLANATIONS
	MAXLOGIC ML-1710/M FIRE ALARM BUTTON
	MAXLOGIC ML-110/M SMOKE DETECTOR
	MAXLOGIC ML-1234.N/M FIRE ALARM PANEL
	MAXLOGIC ML-1430/M FIRE ALARM SIREN
	MAXLOGIC ML-1140/M MULTI SENSOR

NOT:KABLOLAR YANMAZ HALOJEN FREE ÖZELLİKLİDİR.



HİLAL GEMİ MUHENDİSLİK
ELEKTRİK DONANIM VE OTOMASYON SAN.TİC. LTD. STİ
Aydıntepe mah. İbrahim Koray sok. No:20/2-3 TUZLA/İSTANBUL
Tel:0216 395 60 50 GSM:0530 602 98 77
www.hilalgemi.com

DATE	26,01,2023
DRAWN BY	SULEYMAN SANCAK
CHECKED BY	YUSUF BAK

FIRE ALARM SYSTEM SINGLE LINE DIAGRAMI

FLOATING DOCK

BESIKTAS YZH-3

BESIKTAS SHIPYARD

PROJE KOD

BE2/HLL003

CLASS

RINA

+

Page Number 6

Highest Page Number 6