




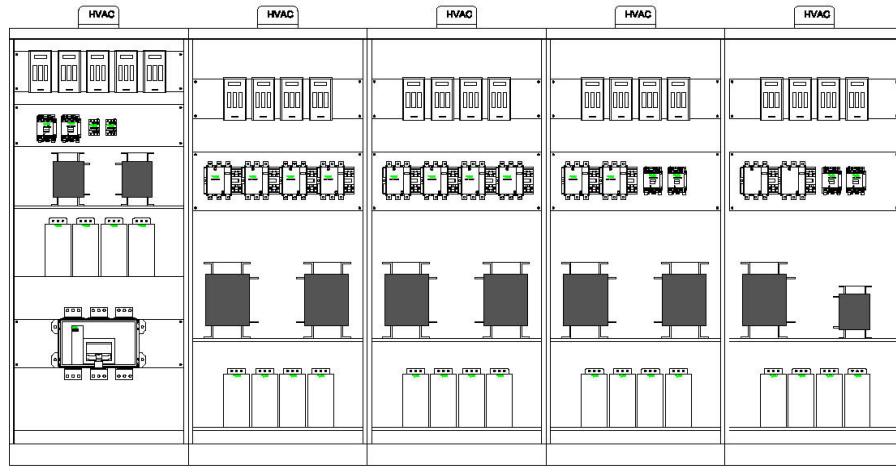


PANO İÇ GÖRÜNÜŞ

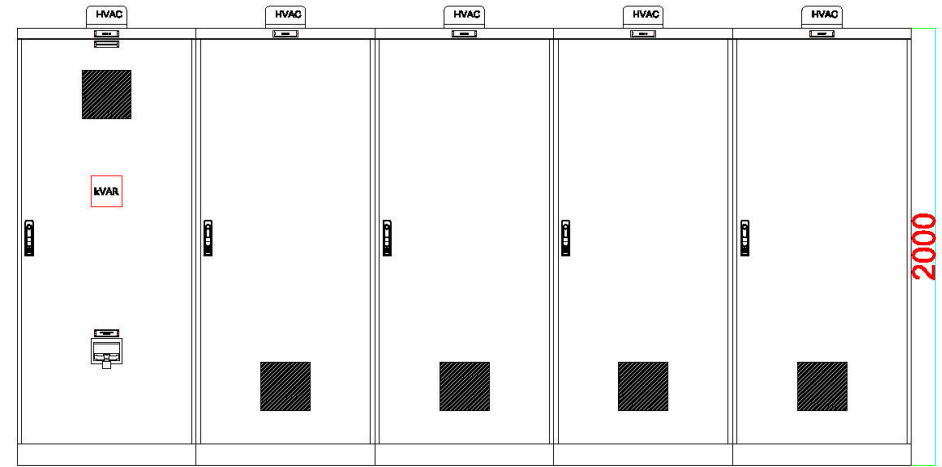


PANO ÖN GÖRÜNÜŞ

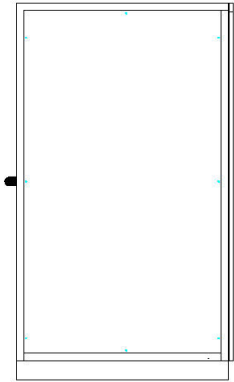

PANO YAN GÖRÜNÜŞ

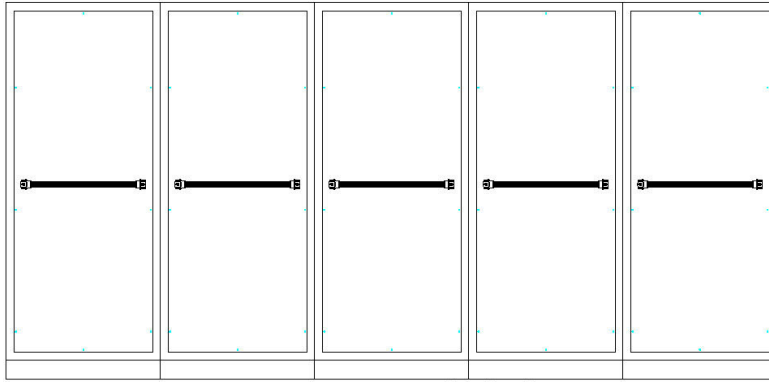

PANO FOUNDATION GÖRÜNÜŞ

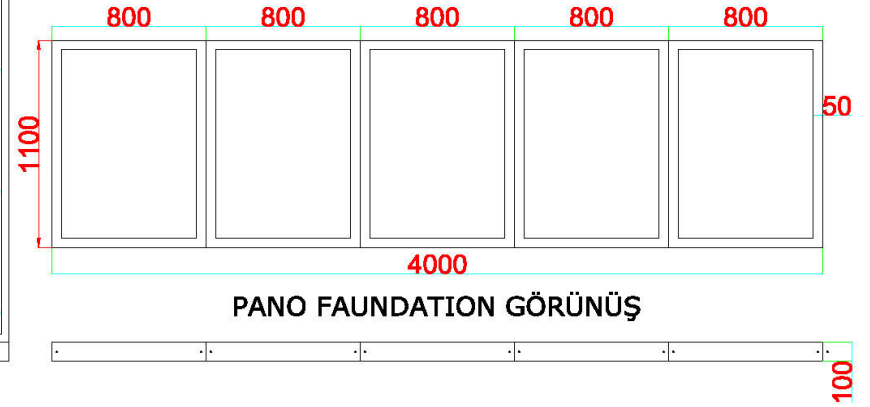

PANO FOUNDATION GÖRÜNÜŞ

BOLME-1


3X100//10 CU

→R/5.0
→S/5.0
→T/5.0

→3F4/4.0


→12/4.0
→11/4.0
→10/4.0
→9/4.0
→8/4.0

4

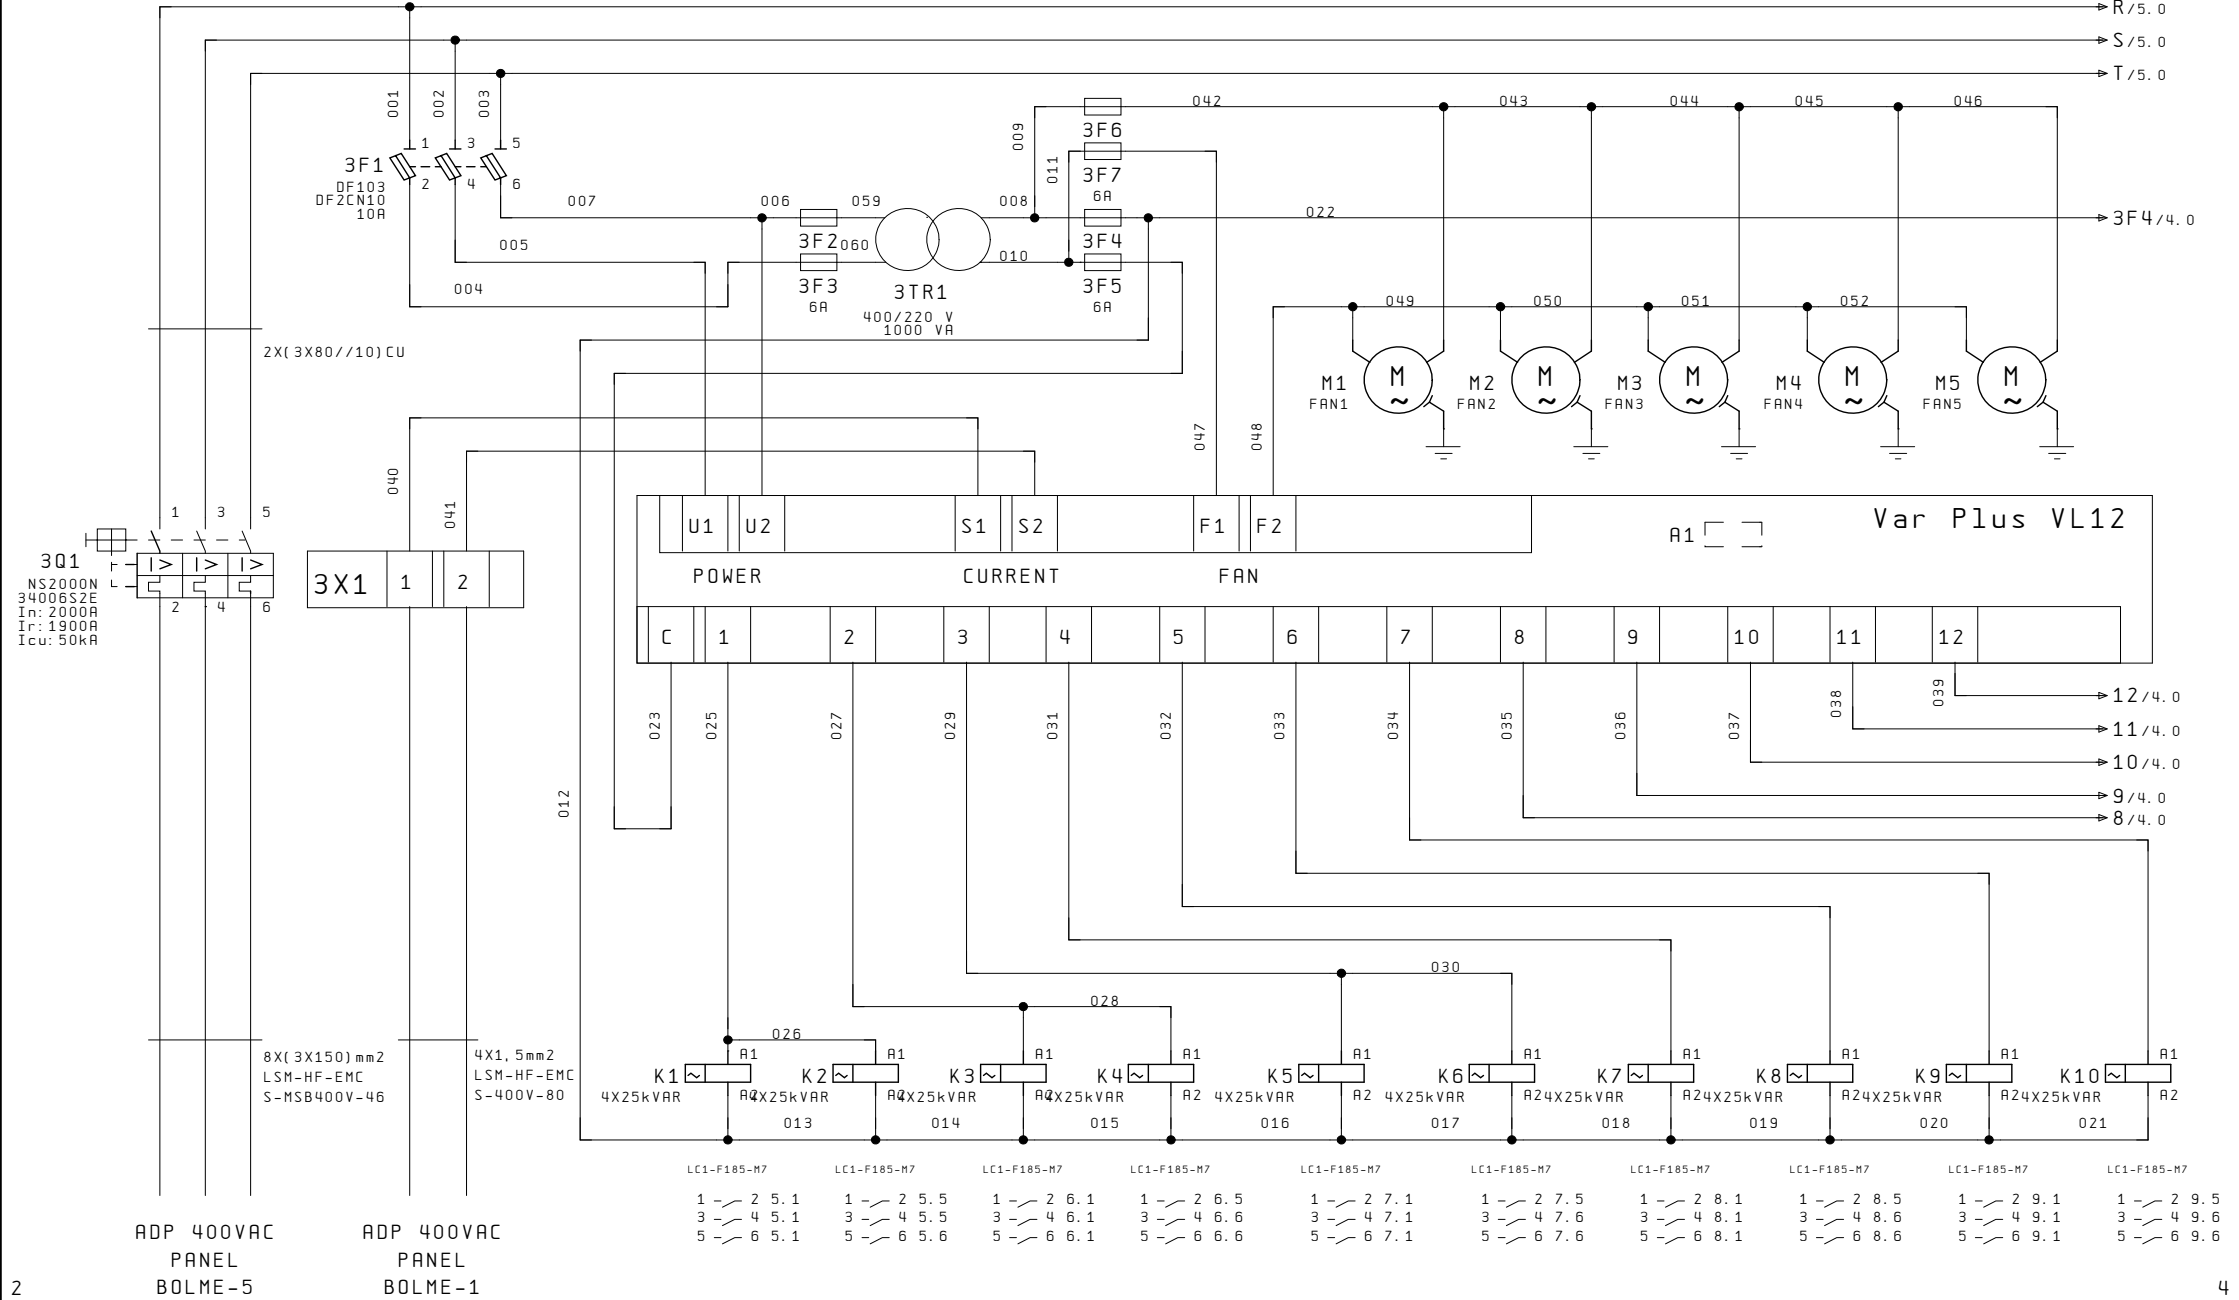


2


0	1	2	3	4	5	6	7	8	9
---	---	---	---	---	---	---	---	---	---

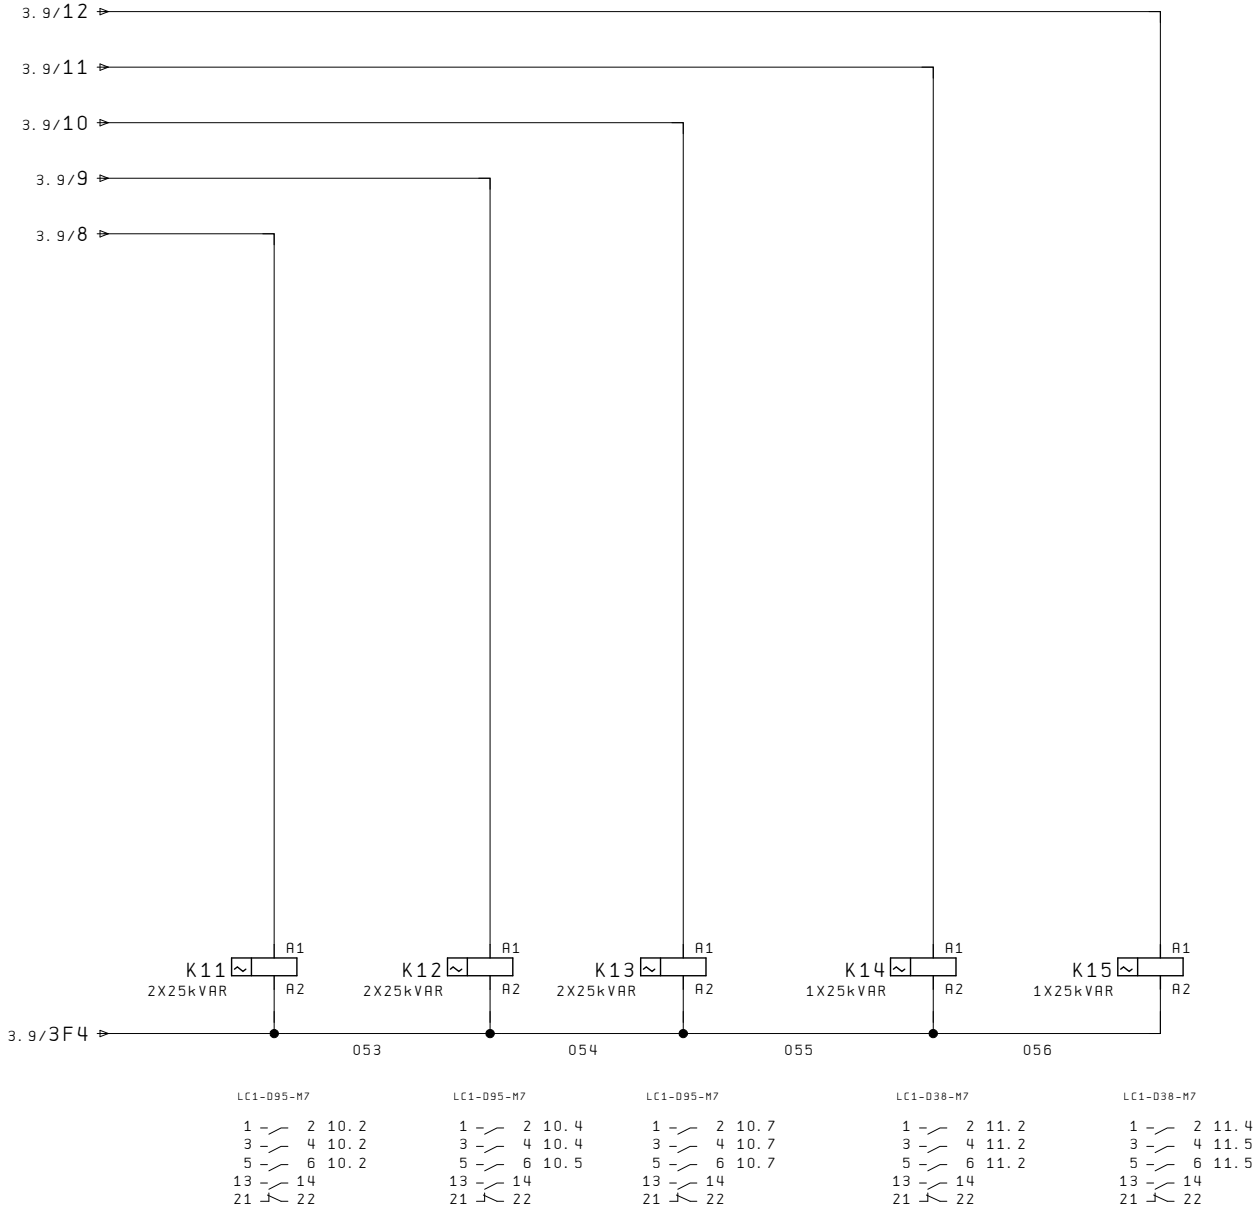

	HILAL GEMİ MUHENDİSLİK ELEKTRİK DONANIM VE OTOMASYON SAN. TİC. LTD. STİ Gıptas San. Sitesi B/Blok No:30 İcmeler/TUZLA Tel:0216 395 60 50 GSM:0539 648 88 05 www.hilalgemi.com		DATE		BESIKTAS TERSANE A. S.	YUZER HAVUZ-3		=
			DRAWN BY	S. SANCAR				+
			CHECKED BY	Y. BAK		PROJE KOD	BSK/HLL-YH52	Page Number
						CLASS	RINA	Highest Page Number


BOLME-2

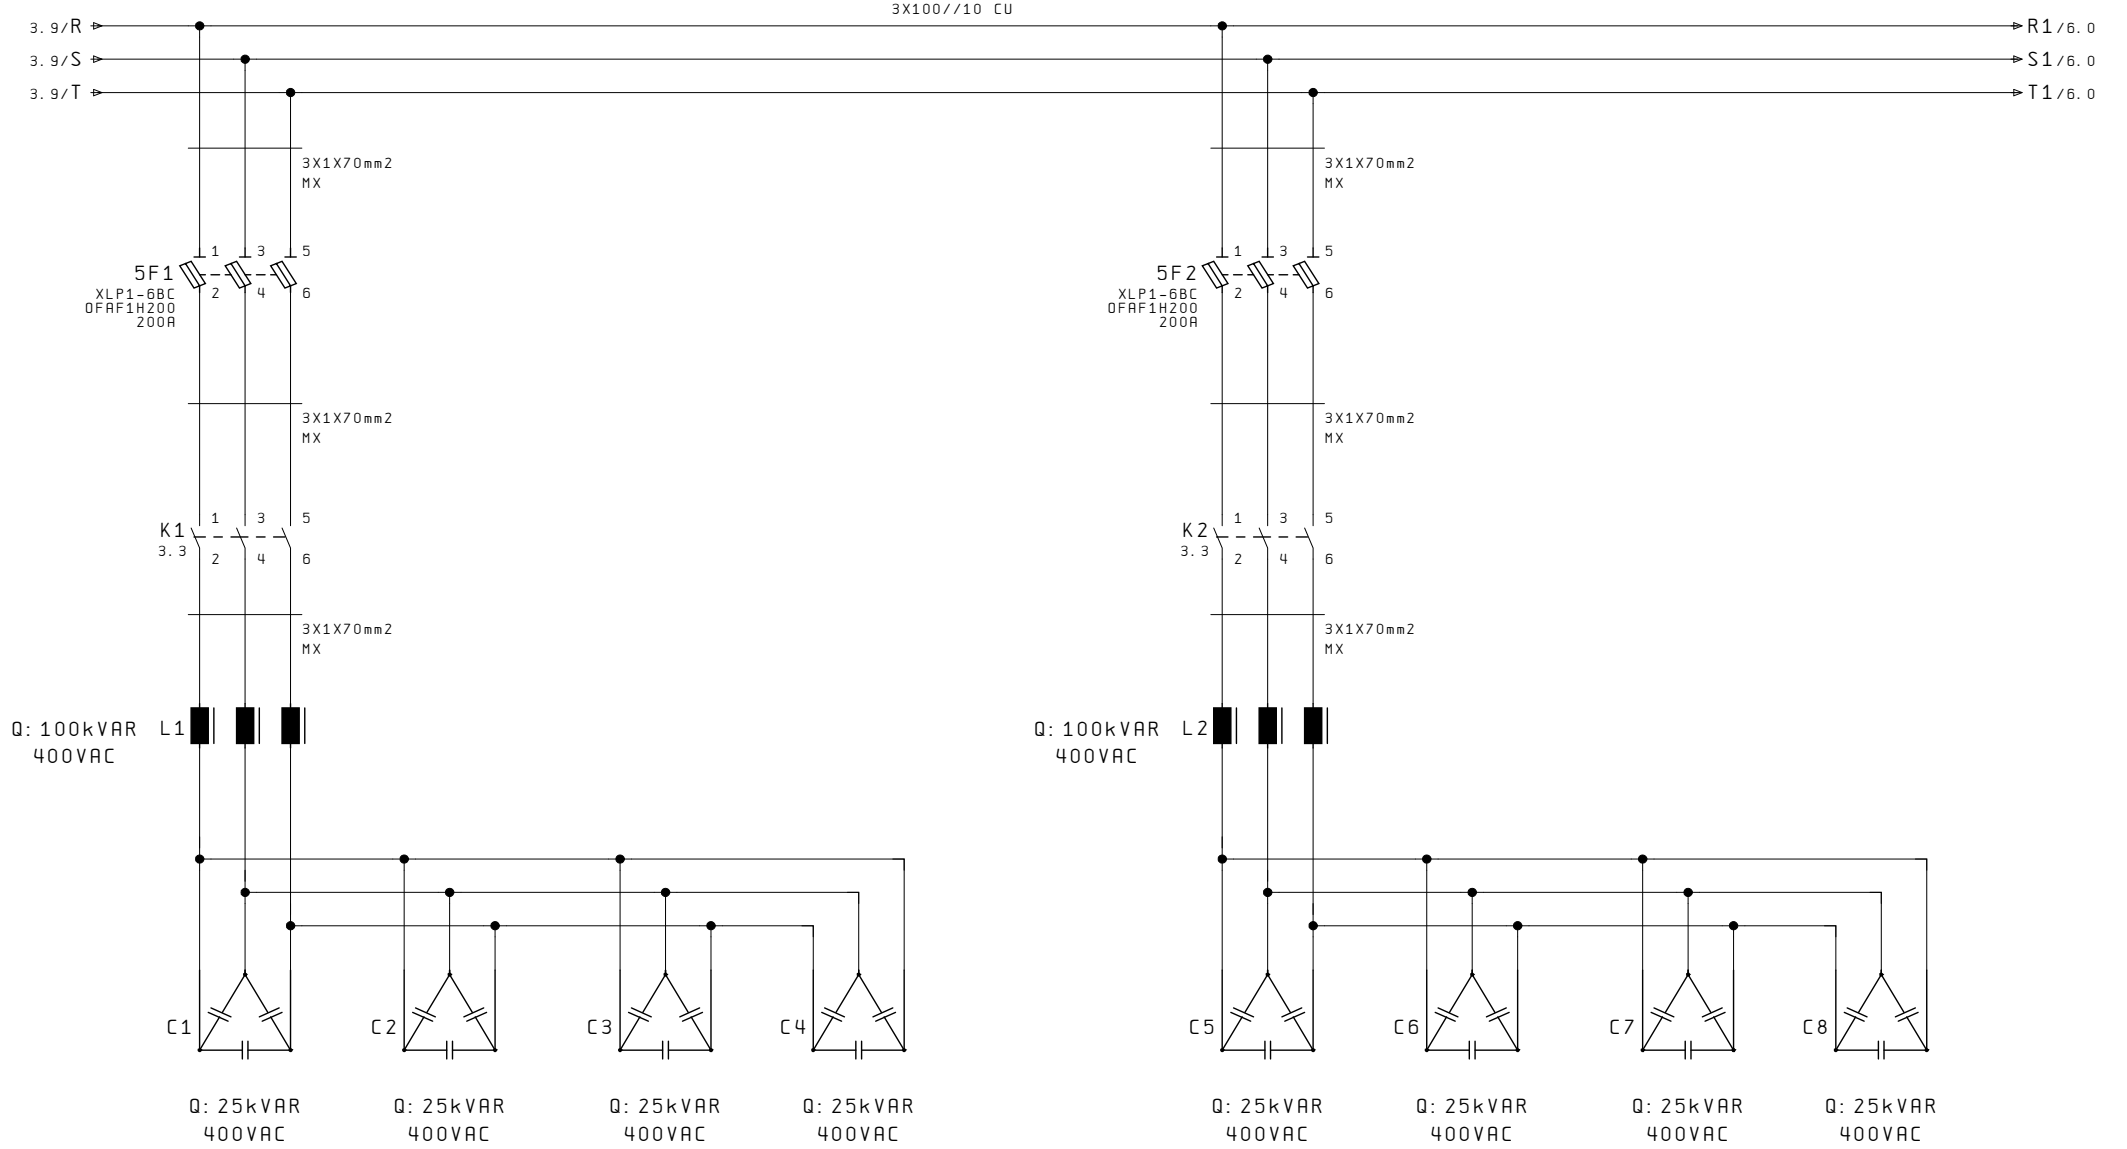

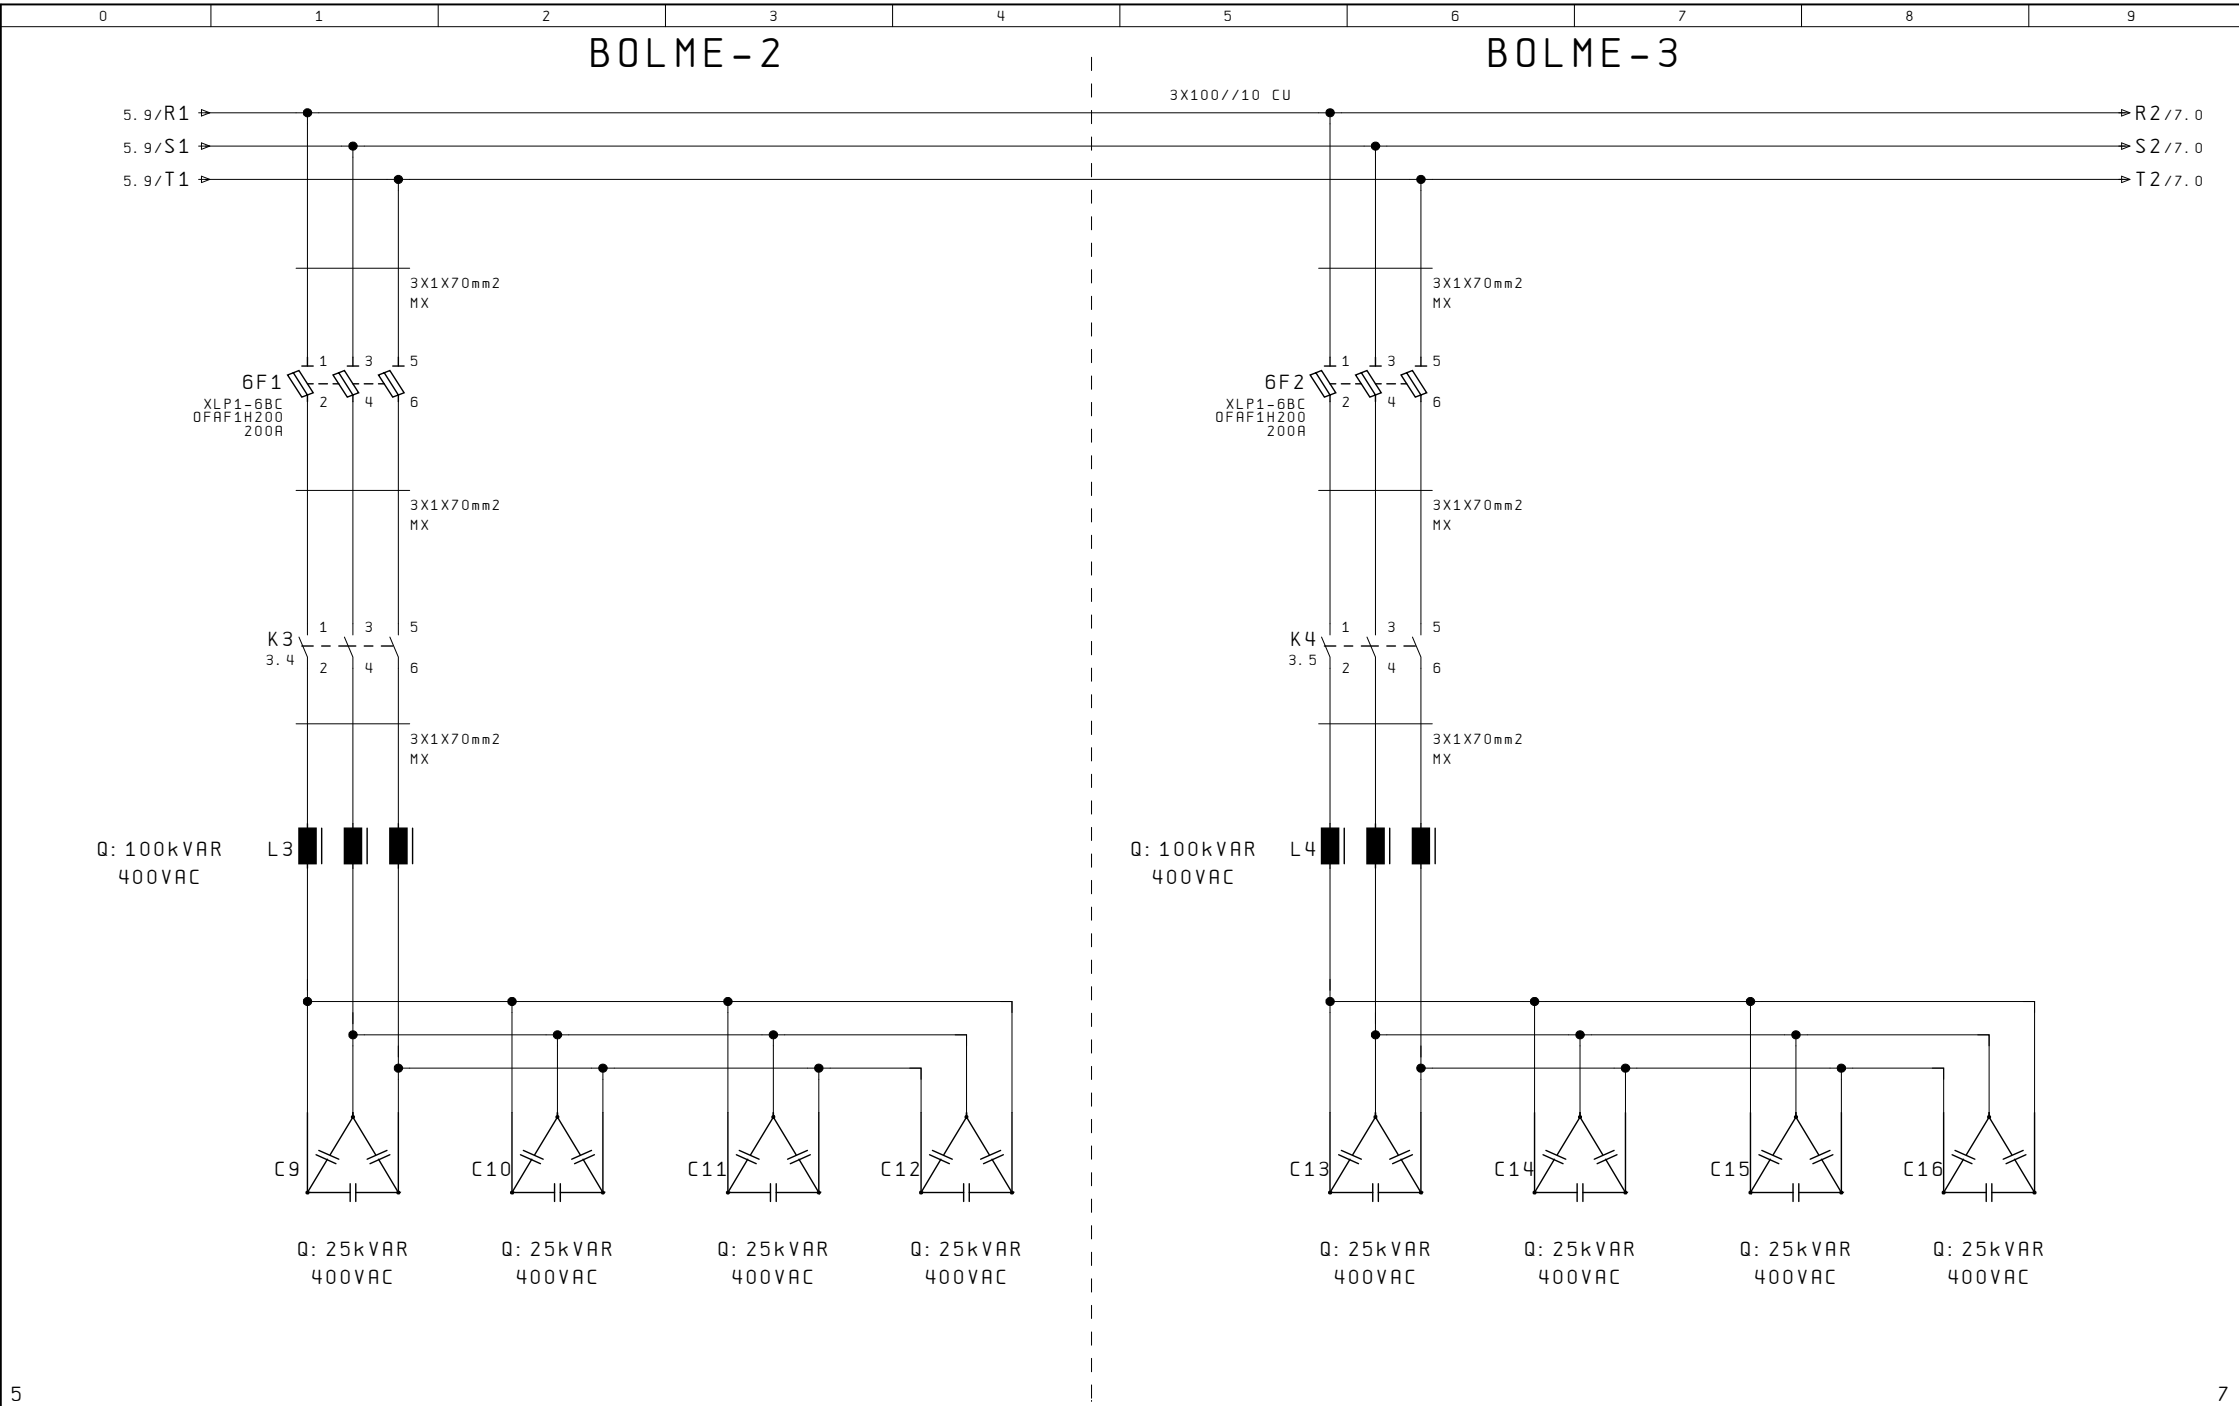


BOLME - 3


3X100//10 CU

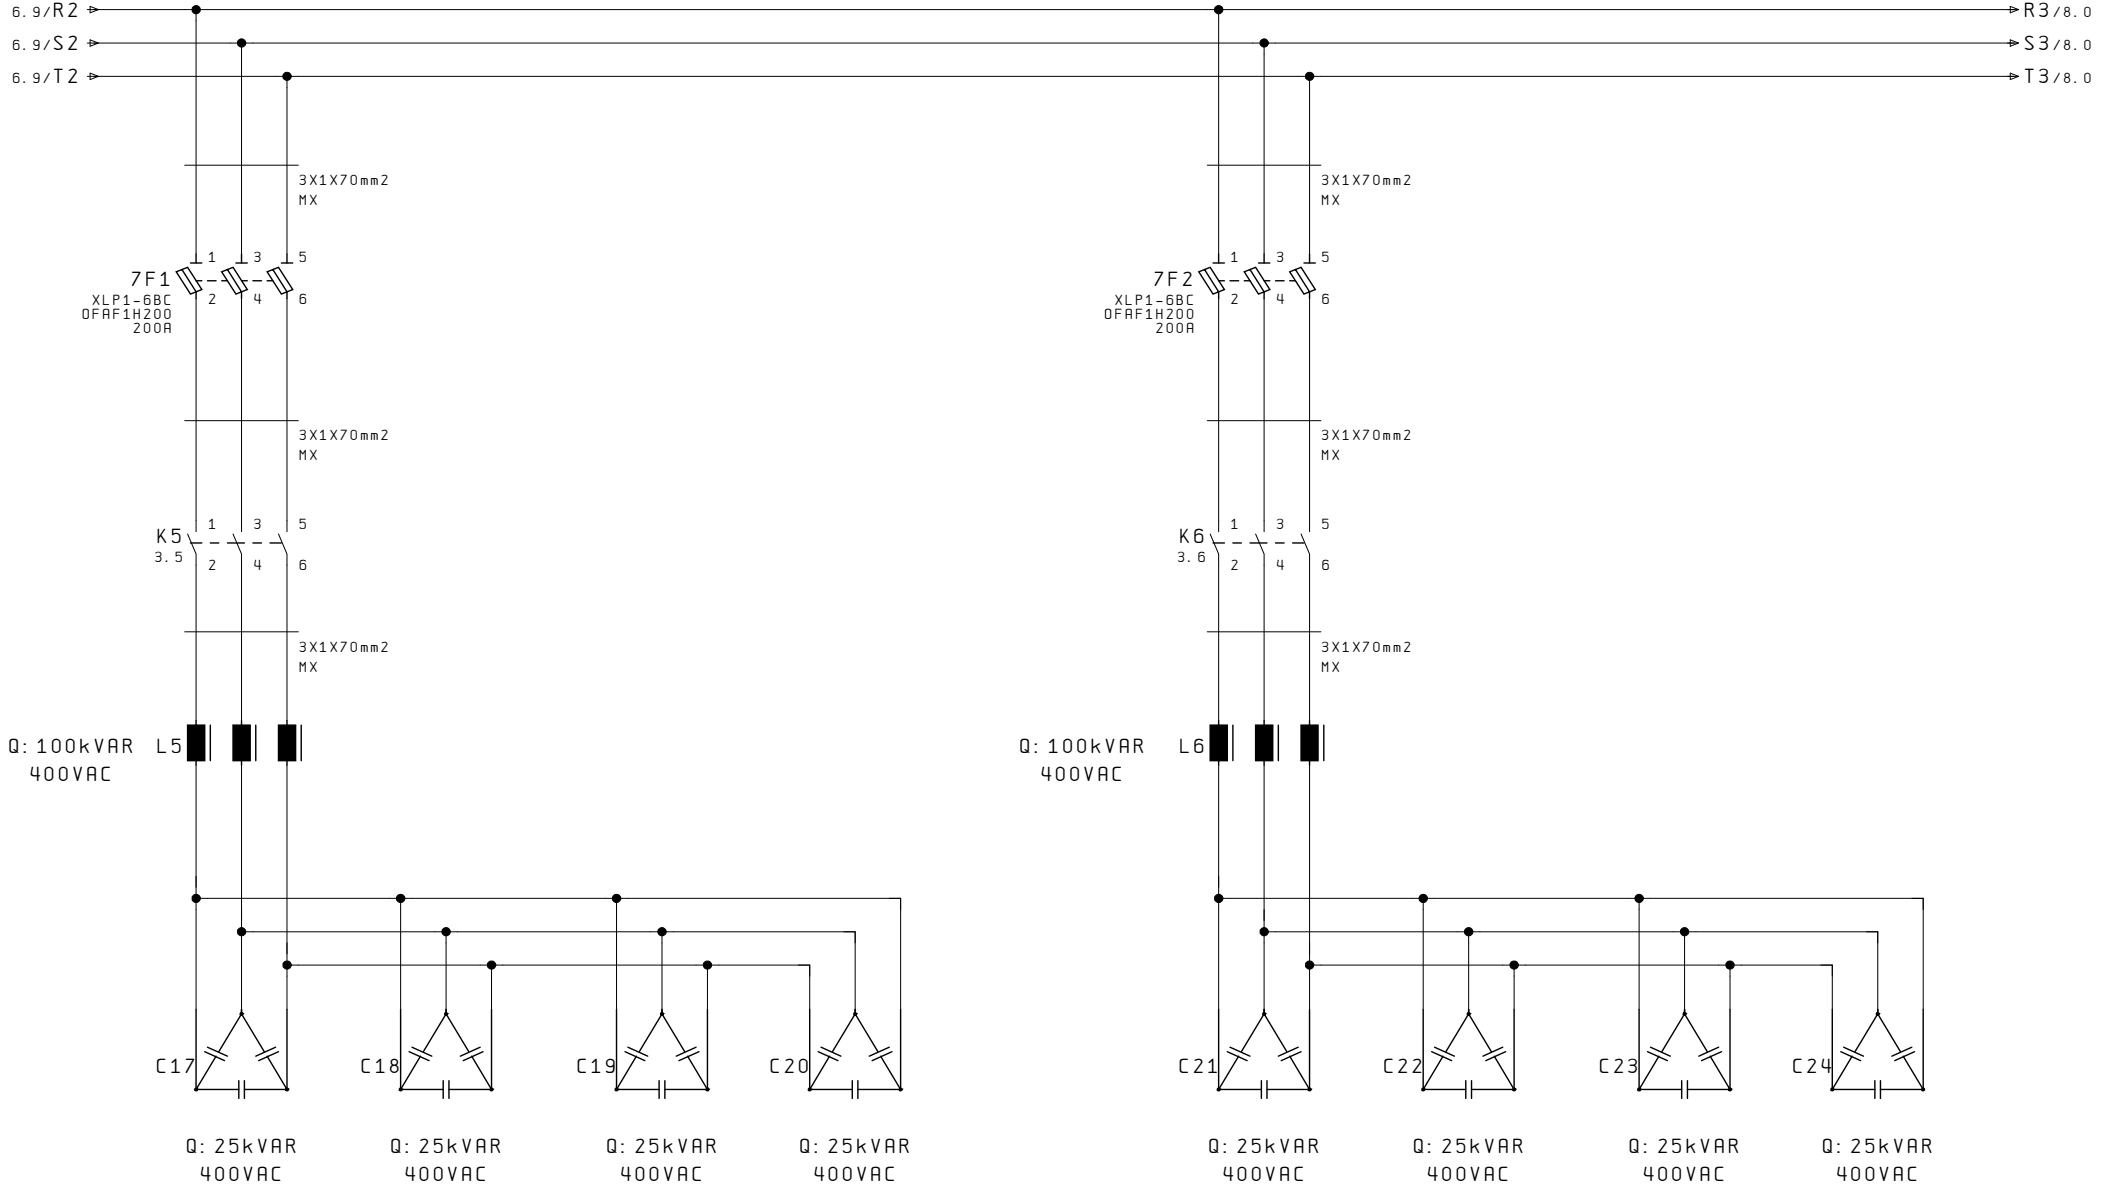


BOLME - 4

3X50//10 CU

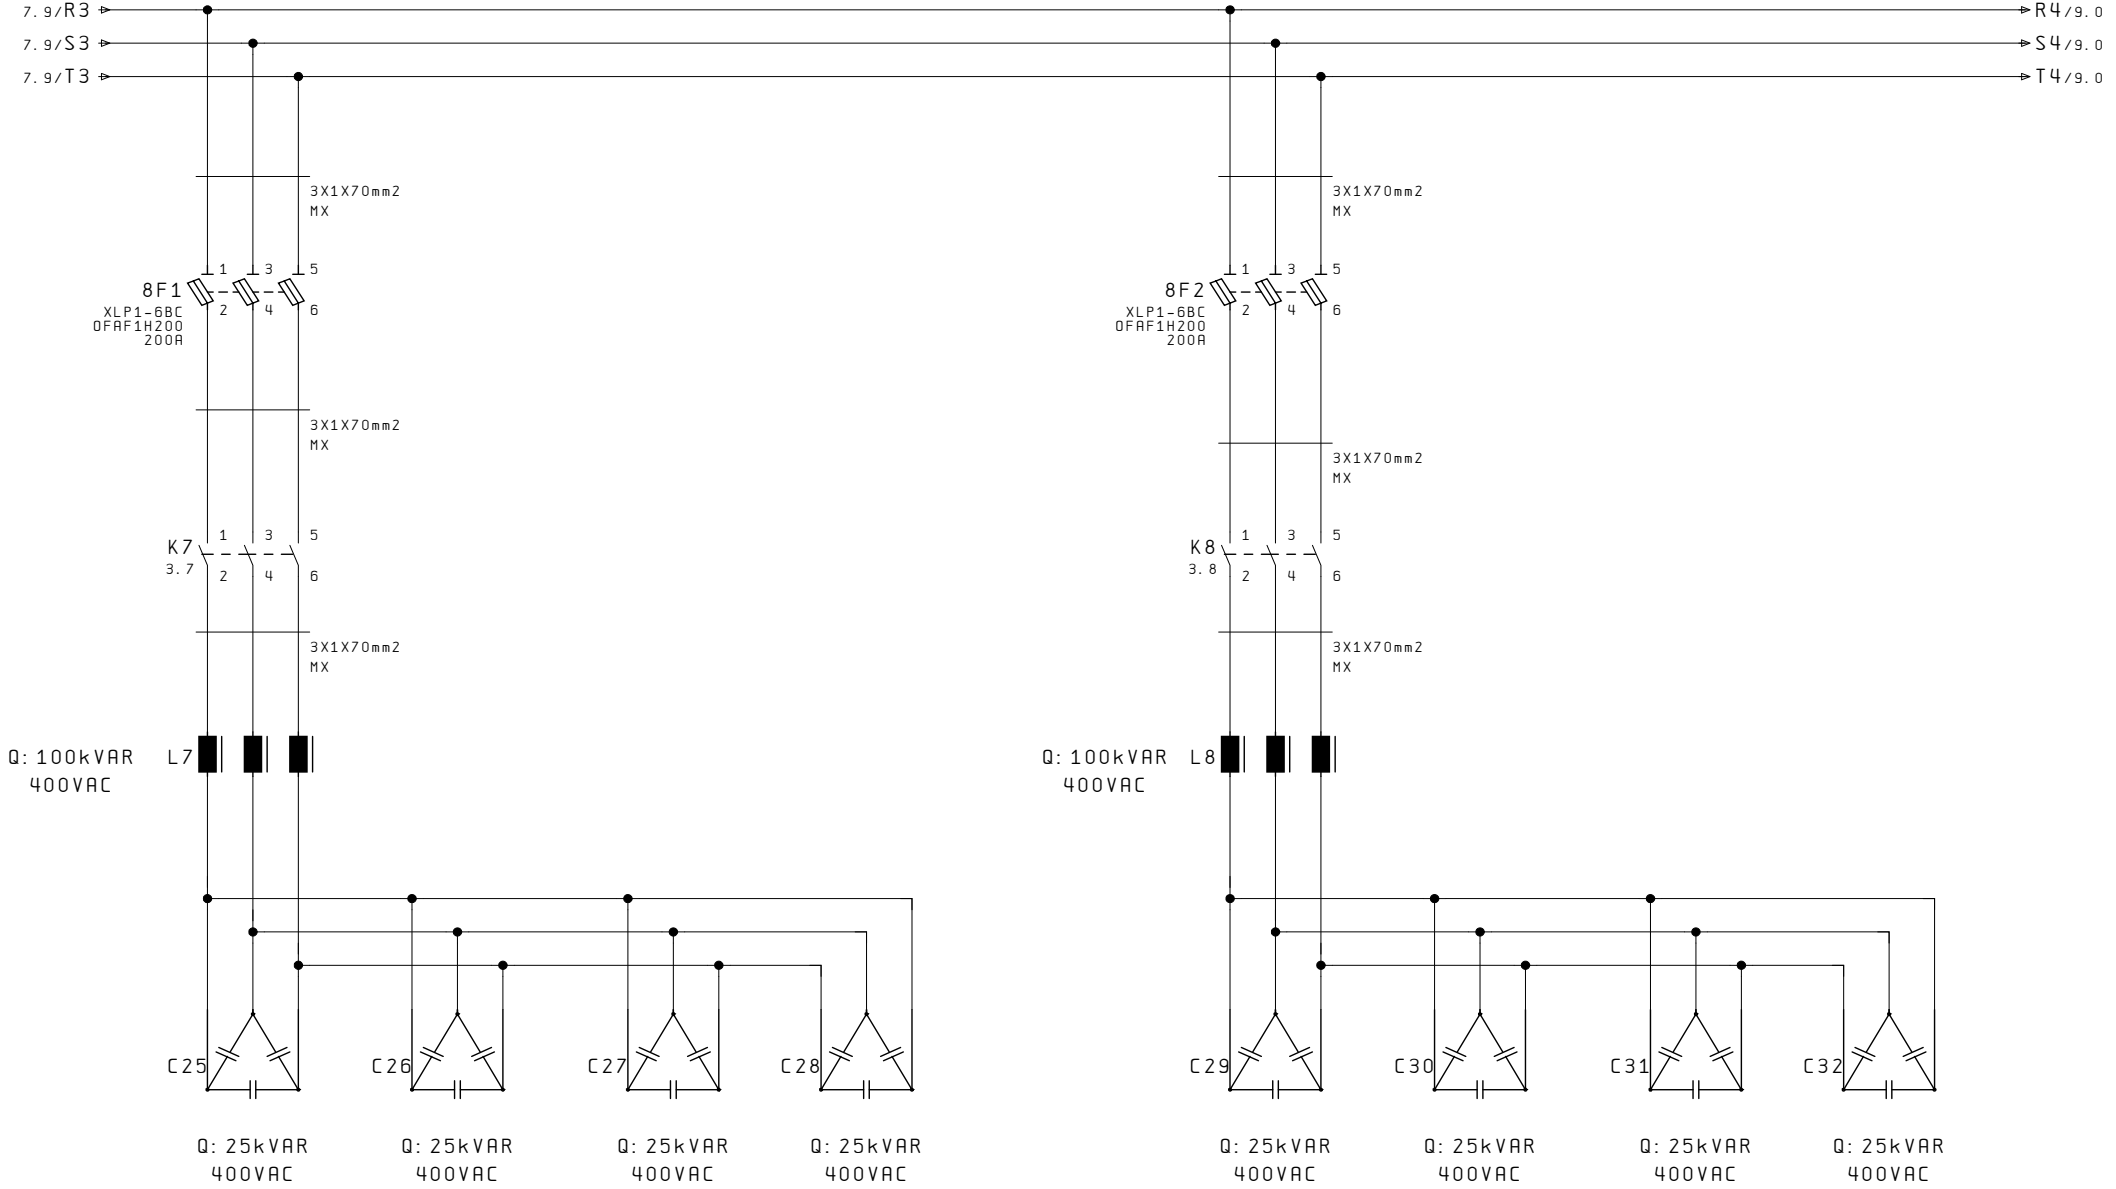


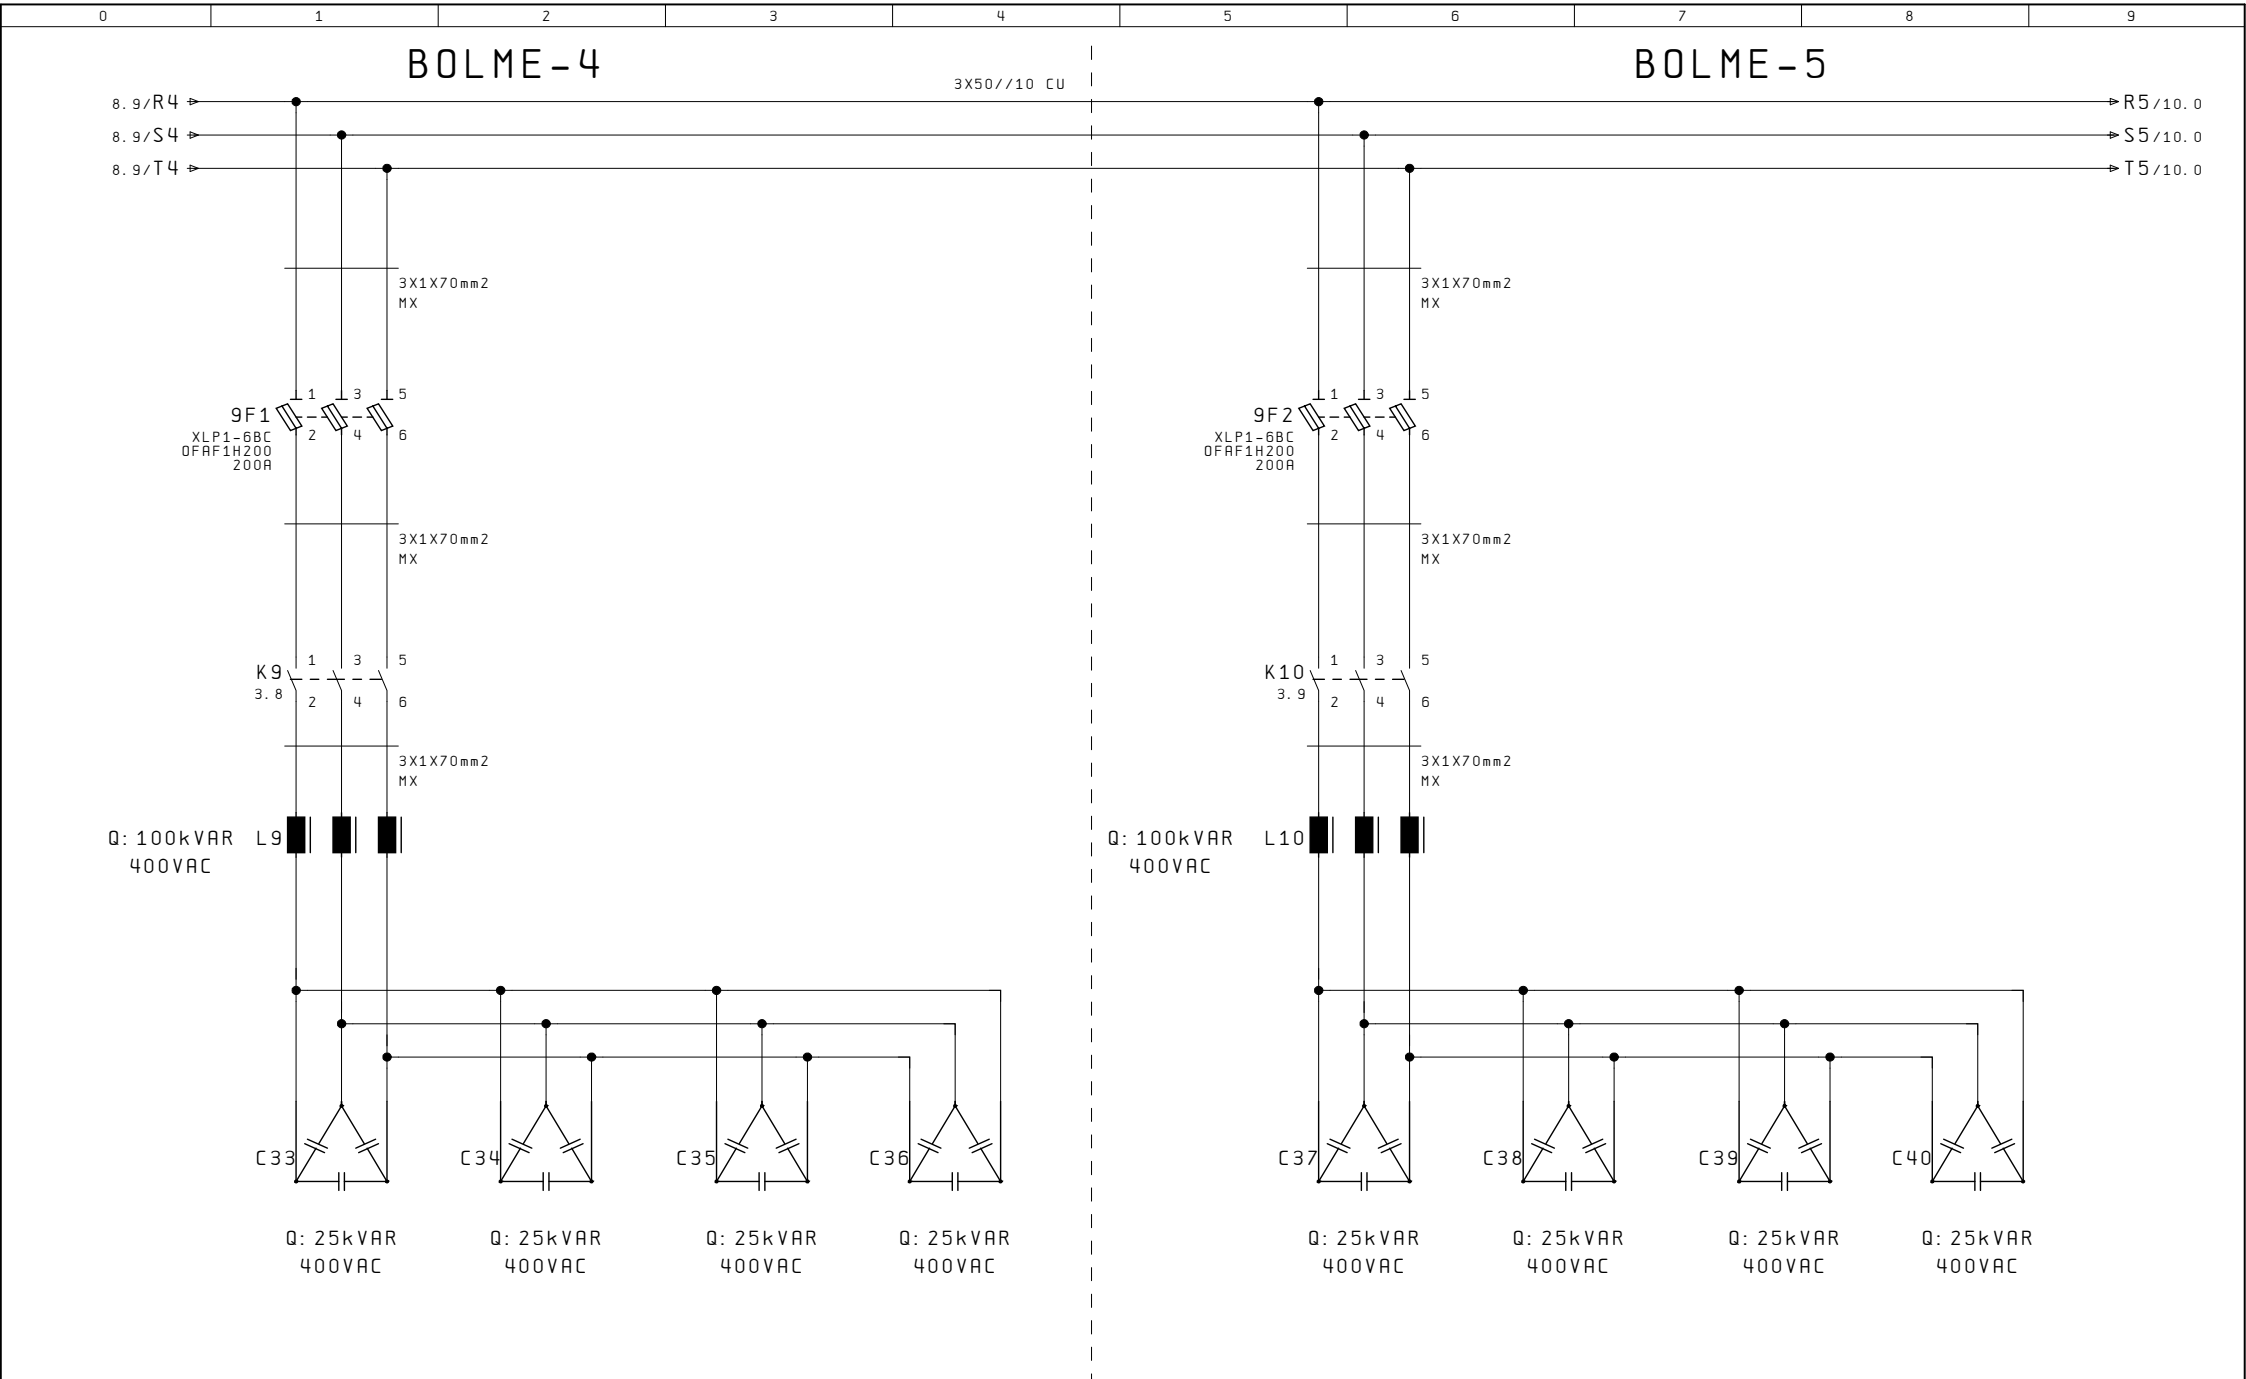

BOLME-5

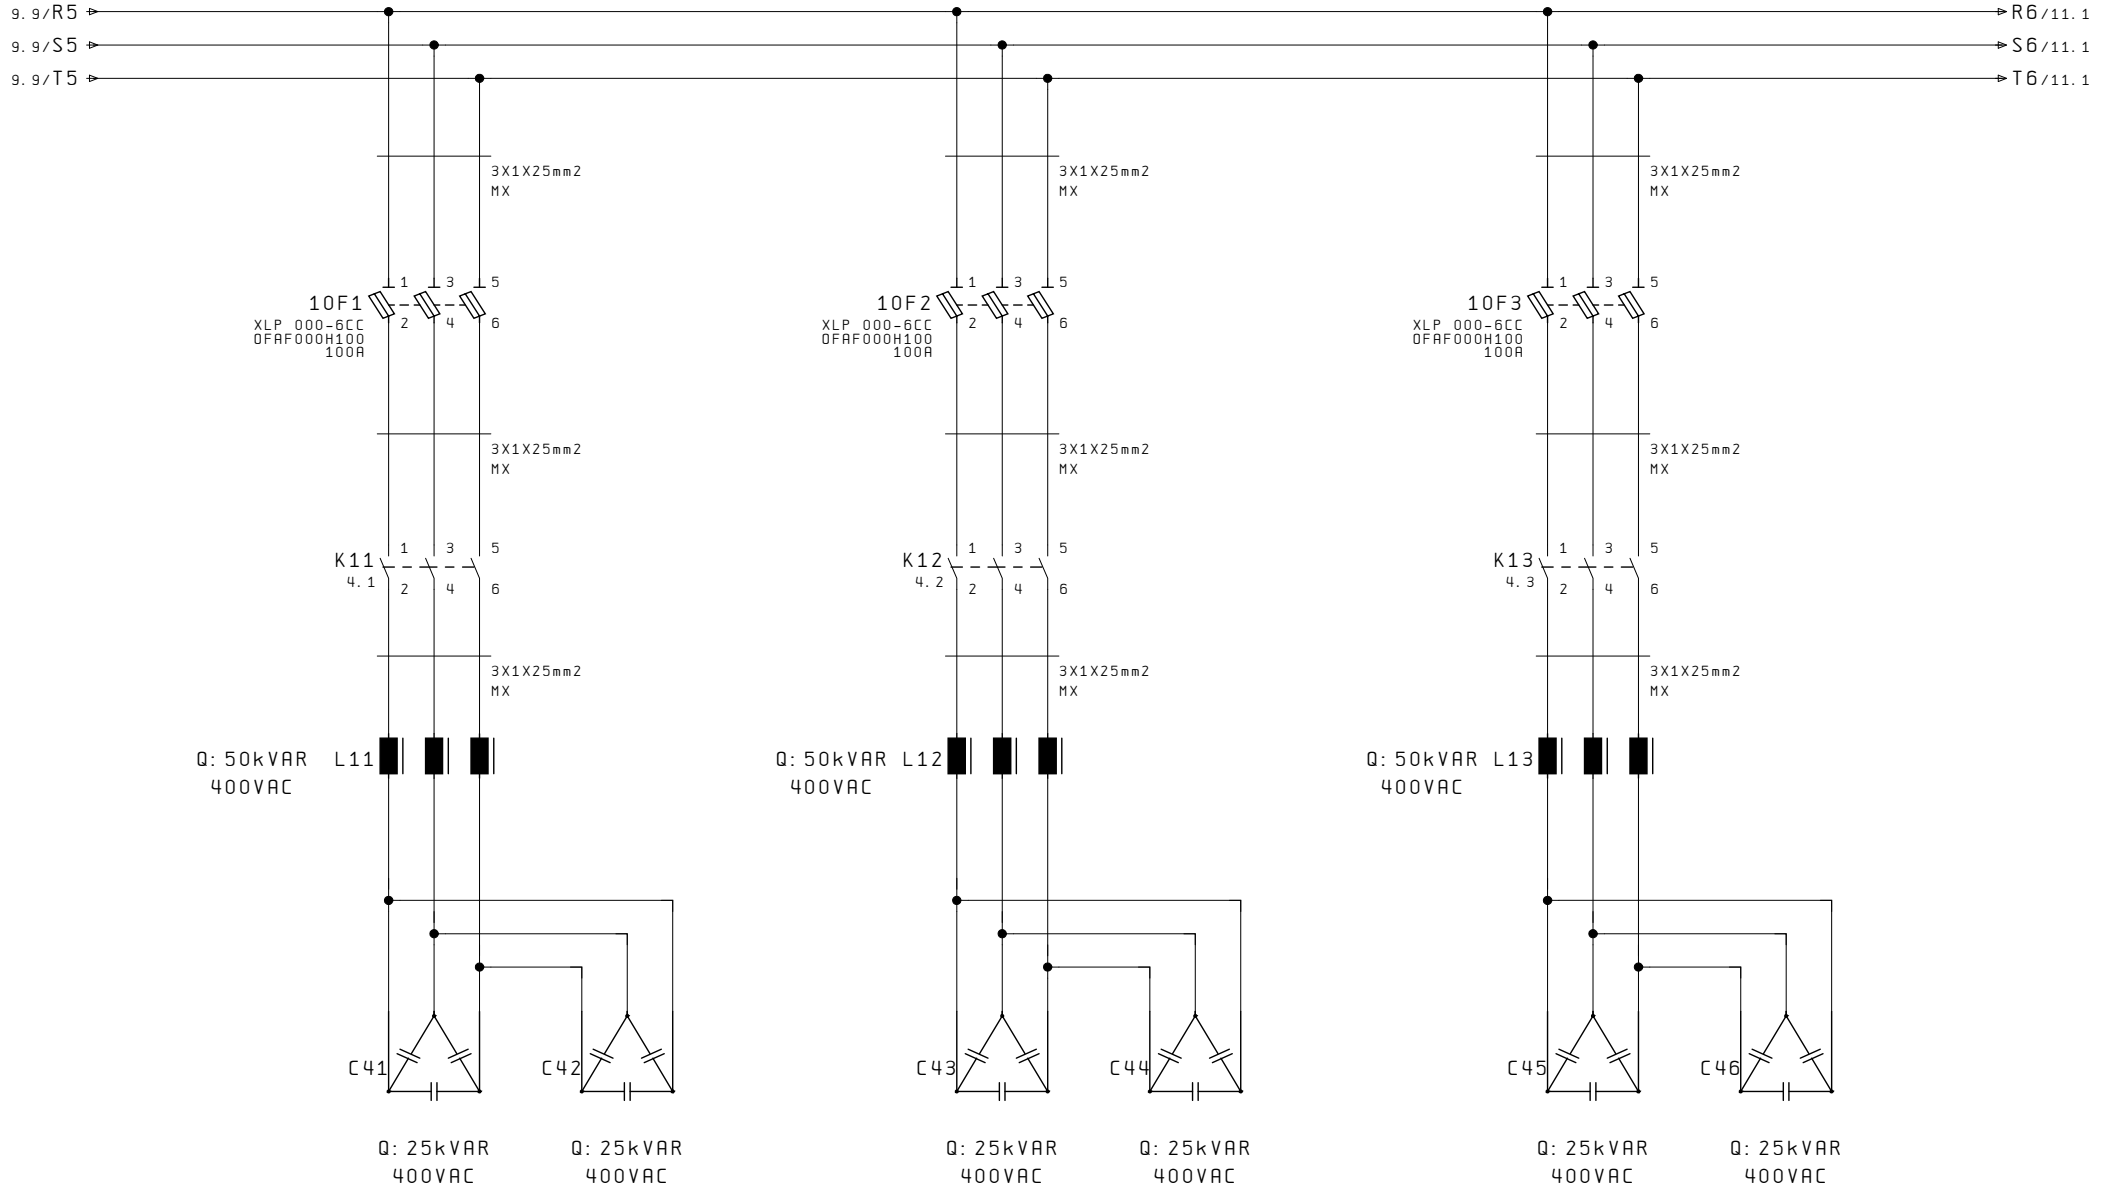

BOLME-5

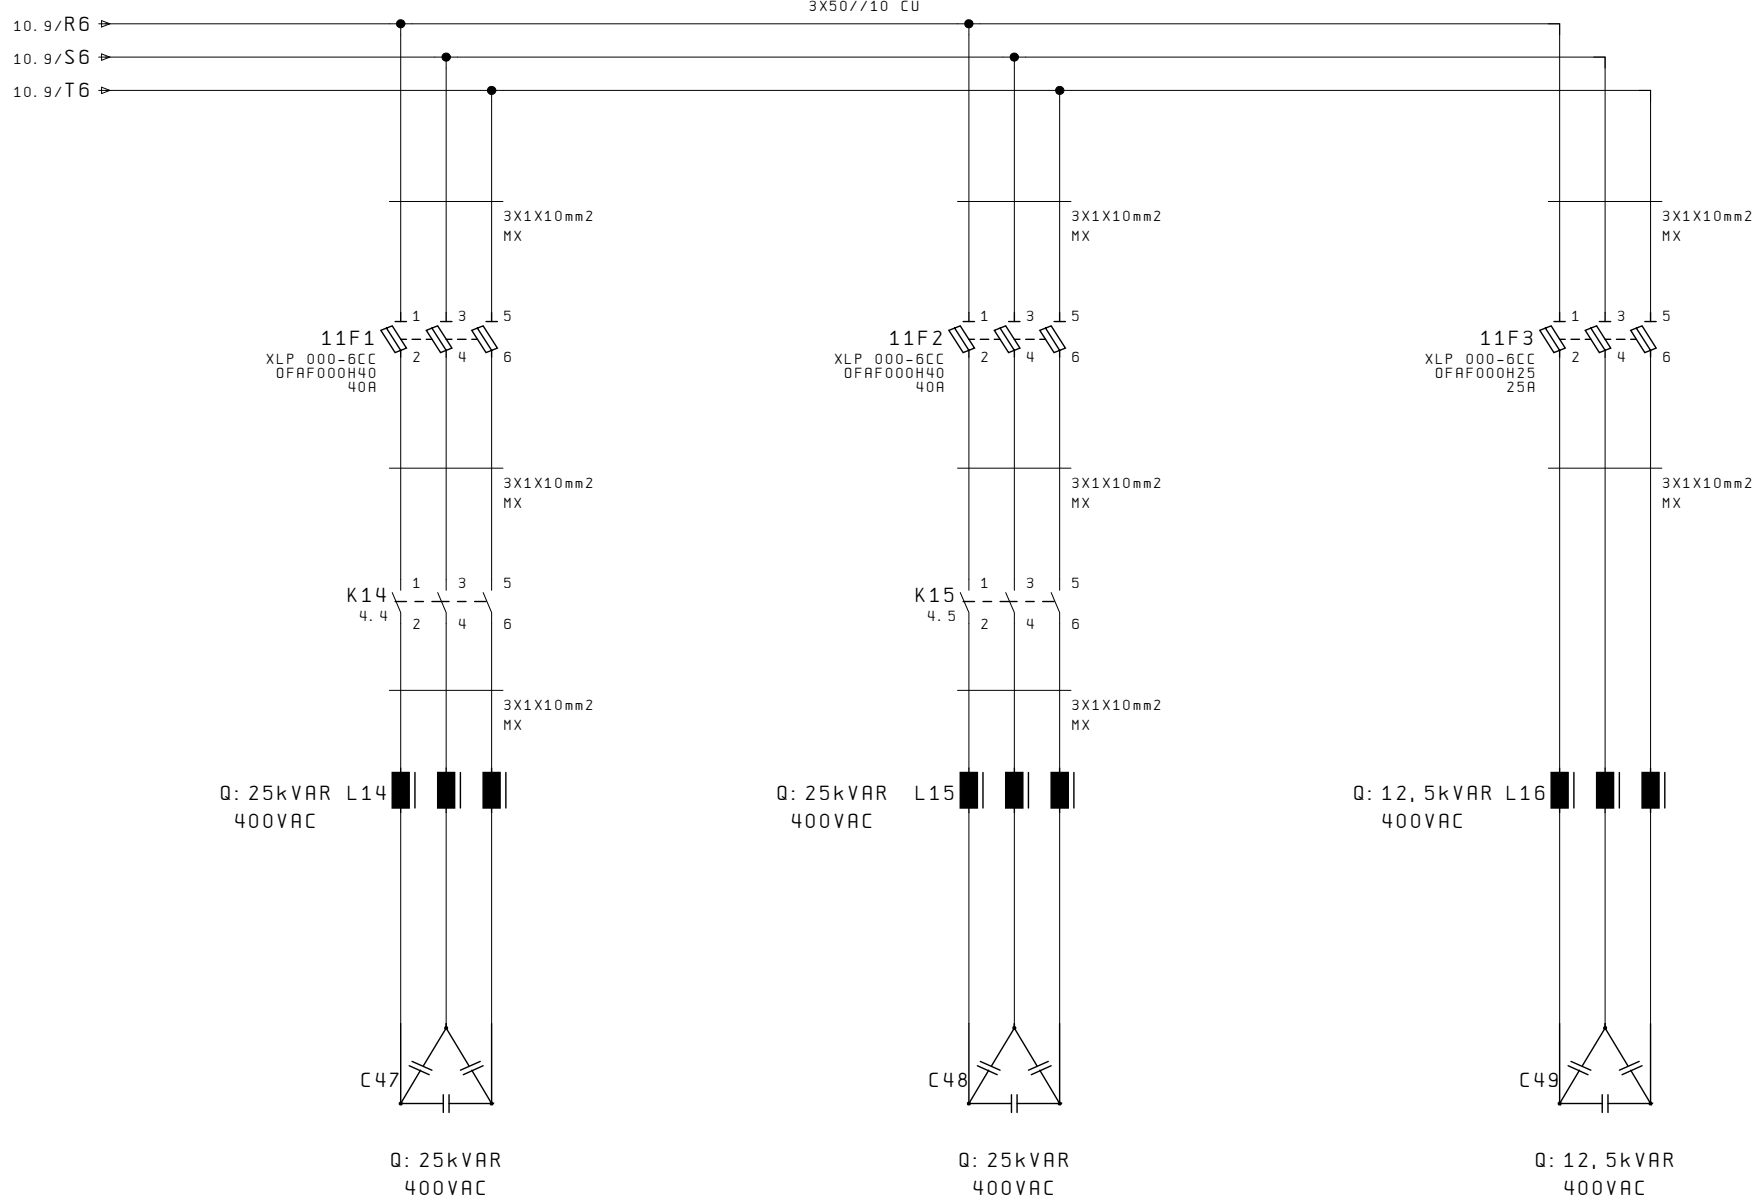

Bill of materials

Item	Amount	Designation	Type	Manufacturer	Article number	Note
301	1	NS2000N		SCHNEIDER	34006S2E 2000A	
3F1	1			SCHNEIDER	DF103	
3F1	3			SCHNEIDER	DF2CN10 10A	
K1	1			SCHNEIDER	LC1-F185-M7-LAD-N40	
3F2	1	SIGORTALI KLEMENS 6mm2 6.3A	351 109	KLEMSAN	ASK 2S	
3F3	1	SIGORTALI KLEMENS 6mm2 6.3A	351 109	KLEMSAN	ASK 2S	
3TR1	1				400/220V 1000VA	
K2	1			SCHNEIDER	LC1-F185-M7-LAD-N40	
K3	1			SCHNEIDER	LC1-F185-M7-LAD-N40	
3F6	1	SIGORTALI KLEMENS 6mm2 6.3A	351 109	KLEMSAN	ASK 2S	
3F7	1	SIGORTALI KLEMENS 6mm2 6.3A	351 109	KLEMSAN	ASK 2S	
3F4	1	SIGORTALI KLEMENS 6mm2 6.3A	351 109	KLEMSAN	ASK 2S	
3F5	1	SIGORTALI KLEMENS 6mm2 6.3A	351 109	KLEMSAN	ASK 2S	
K4	1			SCHNEIDER	LC1-F185-M7-LAD-N40	
K5	1			SCHNEIDER	LC1-F185-M7-LAD-N40	
K6	1			SCHNEIDER	LC1-F185-M7-LAD-N40	
K7	1			SCHNEIDER	LC1-F185-M7-LAD-N40	
A1	1			SCHNEIDER	VL12 KVAR	
K8	1			SCHNEIDER	LC1-F185-M7-LAD-N40	
K9	1			SCHNEIDER	LC1-F185-M7-LAD-N40	
K10	1			SCHNEIDER	LC1-F185-M7-LAD-N40	
K11	1			SCHNEIDER	LC1-D95-M7	
K12	1			SCHNEIDER	LC1-D95-M7	
K13	1			SCHNEIDER	LC1-D95-M7	
K14	1			SCHNEIDER	LC1-D38-M7	
K15	1			SCHNEIDER	LC1-D38-M7	
L1	1			AGPLUS	100KVAR 400VAC	
5F1	1			ABB	XLP1-6BC	
5F1	3			ABB	OFAF1H200	
5F2	1			ABB	XLP1-6BC	
5F2	3			ABB	OFAF1H200	
6F1	1			ABB	XLP1-6BC	
6F1	3			ABB	OFAF1H200	
6F2	1			ABB	XLP1-6BC	
6F2	3			ABB	OFAF1H200	
7F1	1			ABB	XLP1-6BC	
7F1	3			ABB	OFAF1H200	
7F2	1			ABB	XLP1-6BC	
7F2	3			ABB	OFAF1H200	
8F1	1			ABB	XLP1-6BC	
8F1	3			ABB	OFAF1H200	
8F2	1			ABB	XLP1-6BC	
8F2	3			ABB	OFAF1H200	
9F1	1			ABB	XLP1-6BC	
9F1	3			ABB	OFAF1H200	
9F2	1			ABB	XLP1-6BC	
9F2	3			ABB	OFAF1H200	
10F1	1			ABB	XLP 000-6CC	
10F1	3			ABB	OFAF000H100	
10F2	1			ABB	XLP 000-6CC	

